
SAMARKAND

Covered terrace · Layout R12 · rev. 8

Tajik & Uzbek national cuisine · 254 Võ Nguyên Giáp, Đà Nẵng

R12

2026-11-04

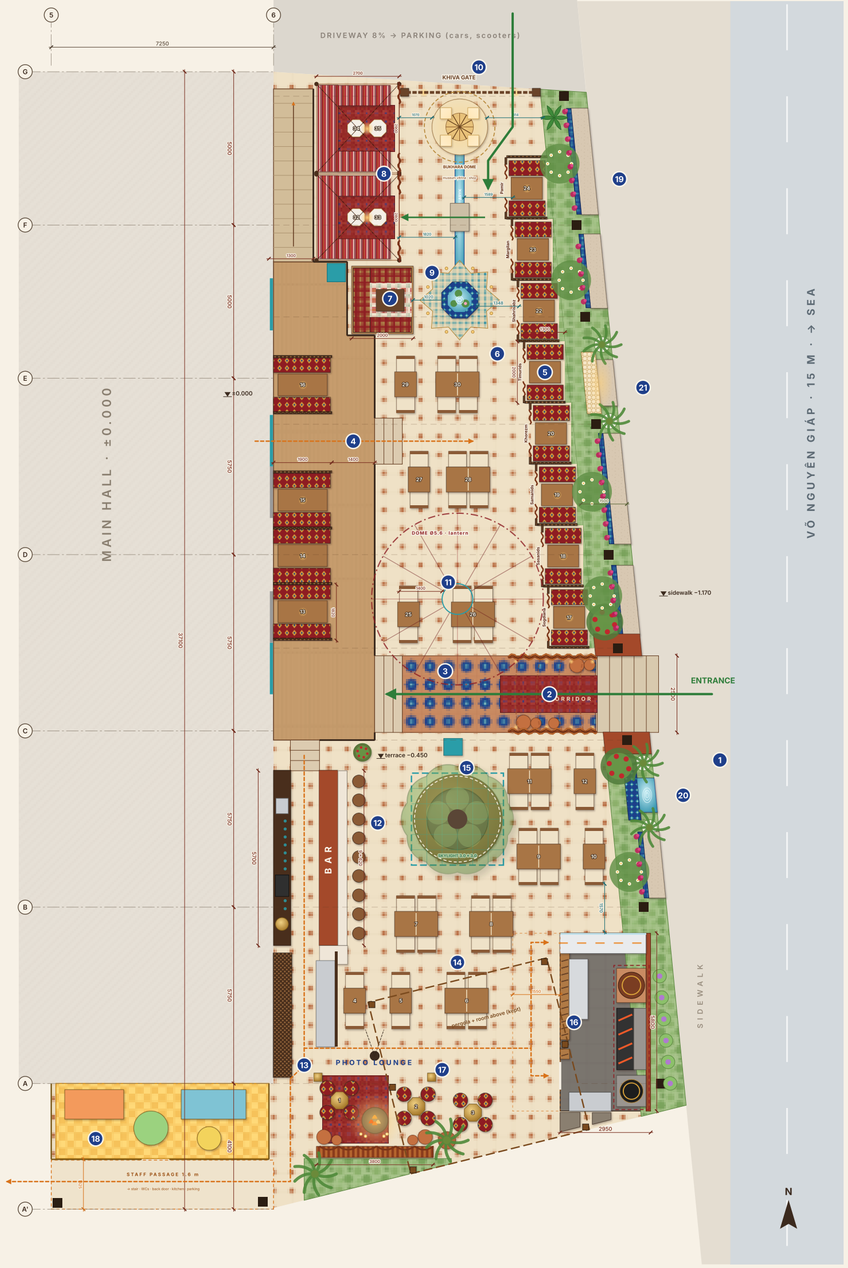

Scale 1:100 · A2

0 5 m

ZONES

1. **Street entrance · pishtaq portal** — 2.5 m opening, 4 steps from the sidewalk
2. **Draped corridor** — crossed velvet swags, layered rugs, terracotta jars, pillar candles
3. **Alley to the hall** — girih paving, 2.5 m, host at the exit
4. **Aivan platform ±0.000** — 4 sedir booths for 6, carved screens, 65° display to the alley
5. **Themed booths** — 8 closed rooms, epochs and cities, curtained portals
6. **Tables by the fountain** — a 4-top + a 2-top, where the north chinar stood
7. **Tapchan 2.0 × 2.2 m** — 6 guests, balustrade, kurpacha, turned-leg table
8. **Two majlis tents 2.6 × 2.75 m** — 8 guests each, floor majlis seating, octagonal tables
9. **Hauz fountain and aryk** — hauz Ø1.2 m, 0.3 m aryk leads from the north entrance
10. **North entrance · "Khiva gate"** — 4.1 m gate, Bukhara dome — vitrine and shop, ramp 1:12
11. **Dining north** — rows of a 4-top + a 2-top, the space under the dome kept open
12. **Bar** — tea, samovar, coffee · 9 stools
13. **Staff station** — shelving, POS, water, ice, dishes
14. **Dining south** — row 4 + 2 + 4 and row 4 + 4
15. **Chinar under the lantern + entrance tables** — tree under the roof, 3 × 3 m skylight; 4 tables by the mangal
16. **Mangal kitchen 3.3 × 5.8 m** — tandoor · mangal · kazan · pass · SAMARKAND sign
17. **Photo lounge "Ochag"** — drapes, carpets, fire bowl, 3 low tables, 12 poufs
18. **Kids zone** — against the hall glazing — seen from inside; soft floor
19. **Street benches** — cast concrete in the planter wall, majolica
20. **Sebil fountain** — majolica wall, brass spout, basin
21. **Street photo arch** — bench niche, uplight, palms

SEATS

Entrance tables	12
Chinar bench south	10
Dining south	16
Photo lounge (poufs)	12
Bar counter	9
Aivan: sedir booths (4 × 6)	24
Dining north + tables by the hauz	18
Themed booths	32
Tapchan	6
Majlis tents (2 × 8)	16
Total restaurant seats	**155**
+ street benches (not counted)	~31

Tables: 7 two-tops, 8 four-tops (all split into 2-top modules; no six-tops), 4 booths for 6

ERGONOMICS · standard / as planned

Main path / alley	≥1500	**2500**
Path to the booths	≥1200	**1348**
Path tapchan ⇔ fountain	≥900	**932**
Aivan aisle	≥1200	**1400**
Table module: per guest / depth	600–700 / 750–800	**700 / 800**
Table edge → armchair back	450–600	**525**
Chair back to back (no path)	≥450	**600**
Armchair 580: gap between arms	≥100	**120**
Bar counter: height / overhang	1050 / 250–300	**1050 / 300**
Bar stool pitch	600–650	**620**
Cook work aisle	≥1200	**2450**
Pass → guests	≥1500	**1570**
Ramp: slope / width	1:12 / ≥1200	**1:12 / 1300**
Tapchan: height / per guest	400–450 / ≥600	**450 / 700**
Staff passage (clear at the columns)	≥1200	**1275**
Seat / table / armrest	450–500 / 740–760	**500 / 760 / 660**

KEY


- Roof column (steel, wood-clad)
- Building axis
- Staff route
- Hall door, closed
- Dimension, mm
- Skylight over the chinar
- Roof beam
- Guest entrance
- Hall door, open
- Exhaust hood
- Table no.
- Table module joint

- Base: as-built DWG (Long House, 10-07-2024) 1:1. Levels: sidewalk −1170, terrace −0.450, aivan and hall ±0.000.
- Roof: steel beams on the grid, Klip-Lok standing-seam sheet + insulation, 3.5% fall to the street, one sheet length (no end laps), gutter along the street; balcony soffit +3.850. The existing pergola at the south wall, with a closed room on top of it, is kept: the new roof stops 300 off its walls (box gutter along the west wall, cover flashings).
- One roof dome — the central Ø5.6 karbandi dome with a glazed lantern. The chinar by the bar stays under the roof: crown trained at 2.2–3.0 m, a 3.0 × 3.0 m skylight with a carved panjara grille above it. The north chinar is removed.
- Every loose table is a 700 × 800 module: pairs split into 2-tops or push together into tables for 6–8 (rows are aligned).
- Doors: C–D south open; C–D north and D–E south closed (banquette); D–E north and E–F by the lift open.


PLANTING

- **Pomegranate (anor), symbol of Samarkand** — at the entrance and in a pot by the bar
- **Plumeria (frangipani)** — street planter, evening scent
- **Bougainvillea and jasmine sambac** — on the street bench backs
- **Areca palm** — pots in the photo lounge
- **Banana, Strelitzia nicolai** — green frame of the Khiva gate
- **Reyhan, mint, basil** — herb bed by the mangal, to the table
- **Lotus, water lily** — in the hauz
- **Chinar by the bar (existing)** — under the skylight, trained crown, uplit

MANGAL KITCHEN · 1:100

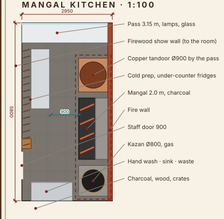

MAJLIS TENT (×2) · 1:75

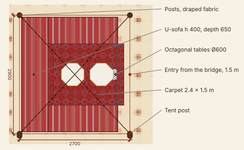

AIVAN: SEDIR BOOTHS · 1:75


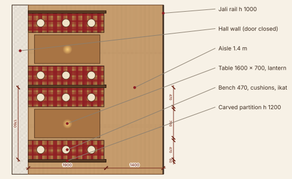


TABLE MODULES · 1:100

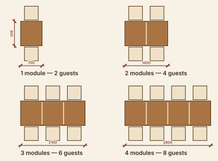

Top 700 × 800, h 760, zellige inlay; joined with hidden clamps

Concept for client review · dimensions to verify on site