
SAMARKAND

R12

Крытая терраса · планировка R12 · ред. 8

2026-11-04

Таджикская и узбекская кухня · Võ Nguyên Giáp, 254, Дананг

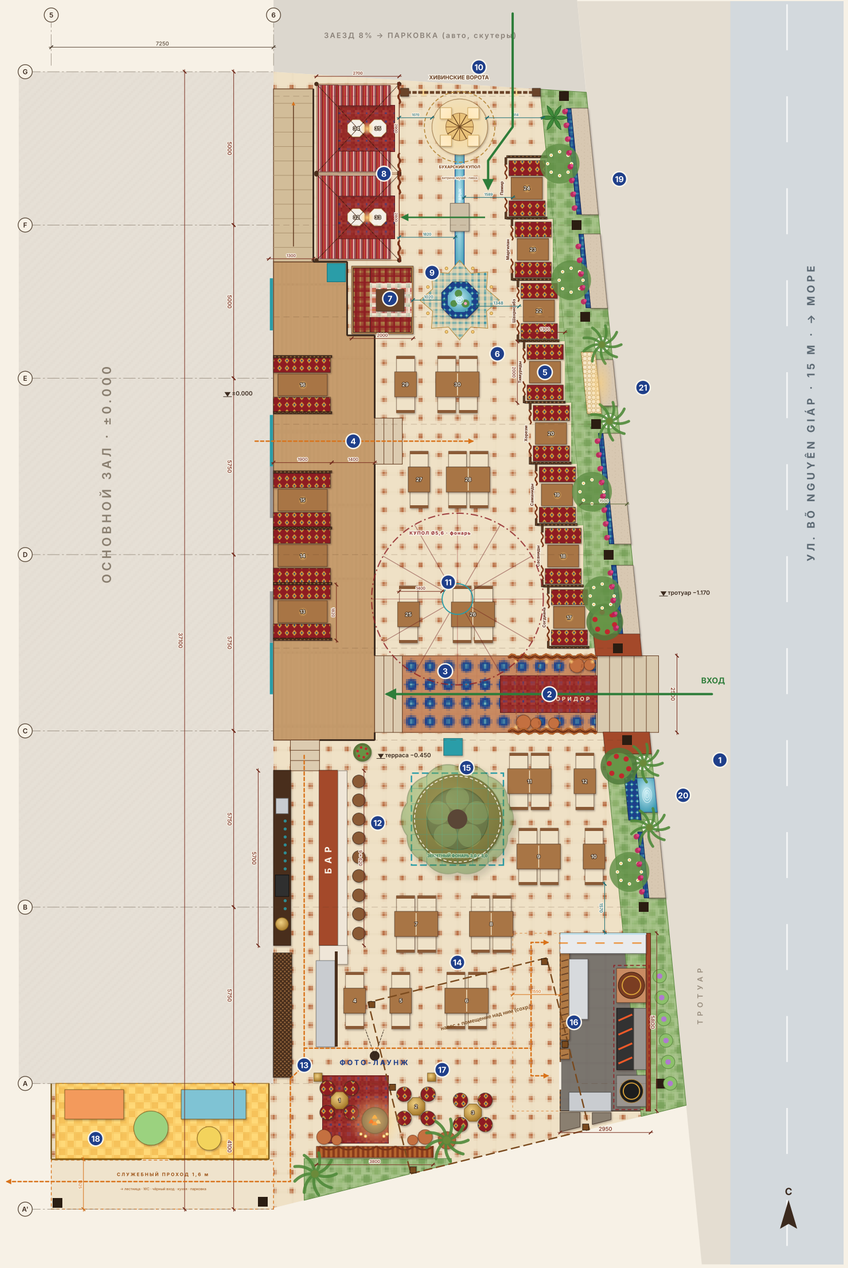

Масштаб 1:100 · A2

0 5 м

ЗОНЫ

1. **Главный вход · портал-пештак** — проём 2,5 м, 4 ступени с тротуара
2. **Коридор-драпировка** — бархатные свали крест-накрест, ковры анхалёт, кувшины, свечи
3. **Аллея к залу** — гирих, 2,5 м, хостес у выхода
4. **Айван-платформа ±0.000** — 4 седир-кабинки на 6, резные экраны, монитор 65″ к аллее
5. **Тематические кабинки** — 8 закрытых залов: этюки и города, шторы-порталы
6. **Столы у фонтана** — на 4 + на 2, на мосте северного чинара
7. **Топчан 2,0 × 2,2 м** — 6 гостей, балясины, курпачи, столик на точёных ножках
8. **Два шатра-маджлиса 2,6 × 2,75 м** — на 8 гостей, напольный маджлис, восьмигранные столики
9. **Фонтан-хауз и арык** — хауз Ø1,2 м, арык 0,3 м ведёт от северного входа
10. **Северный вход · «Хивинские ворота»** — ворота 4,1 м, бухарский купол — витрина и лавка, пандус 1:12
11. **Зал север** — ряды 4 + 2, центр под куполом свободен
12. **Бар** — чай, самовар, кофе · 9 стульев
13. **Станция персонала** — стеллаж, касса, вода, лёд, посуда
14. **Зал юг** — ряд 4 + 2 + 4 и ряд 4 + 4
15. **Чинар под фонарём + столы у входа** — дерево под навесом, зенитный фонарь 3 × 3 м; 4 стола у мангала
16. **Мангальная 3,3 × 5,8 м** — тандыр · мангал · казан · раздача · вывеска SAMARKAND
17. **Фото-лаунж «Очаг»** — драпировки, ковры, огонь-чаша, 3 столика, 12 пуфов
18. **Детская зона** — у стекла зала — дети видны из зала; мягкое покрытие
19. **Уличные скамьи** — литой бетон в стенке клумбы, майолика
20. **Фонтан-себиль** — майоликовая стена, латунный носик, чаша
21. **Уличная фото-арка** — ниша со скамьёй, подсветка, пальмы

ПОСАДКА

Столы у входа	12
Скамья у чинара (юг)	10
Зал юг	16
Фото-лаунж (пуфы)	12
Барная стойка	9
Айван: седир-кабинки (4 × 6)	24
Зал север + столы у фонтана	18
Тематические кабинки	32
Топчан	6
Шатры-маджлисы (2 × 8)	16
Итого мест в ресторане	**155**
+ уличные скамьи (вне счёта)	~31

Столы: на 2 — 7, на 4 — 8 (все делятся на модули 2-местные; столов на 6 нет), кабинки на 6 — 4

ЭРГОНОМИКА · норма / по плану

Главный проход / аллея	≥1500	**2500**
Проход к кабинкам	≥1200	**1348**
Проход топчан ↔ фонтан	≥900	**932**
Проход на айване	≥1200	**1400**
Модуль стола: на 1 гостя / глубина	600–700 / 750–800	**700 / 800**
Край стола → спинка кресла	450–600	**525**
Спинка-спинка (без прохода)	≥450	**600**
Кресло 580: зазор между подлокотниками	≥100	**120**
Барная стойка: высота / вынос	1050 / 250–300	**1050 / 300**
Шаг барных стульев	600–650	**620**
Рабочая зона повара	≥1200	**2450**
Раздача → гости	≥1500	**1570**
Пандус: уклон / ширина	1:12 / ≥1200	**1:12 / 1300**
Топчан: высота / на 1 гостя	400–450 / ≥600	**450 / 700**
Служебный проход (в свету у колонн)	≥1200	**1275**
Сиденье / стол / подлокотник	450–500 / 740–760	**500 / 760 / 660**

ОБОЗНАЧЕНИЯ


- Колонна навеса (сталь, обшивка деревом)
- Ось здания
- Маршрут персонала
- Дверь зала закрыта
- Размер, мм
- Зенитный фонарь над чинаром
- Балка навеса
- Вход гостей
- Дверь зала открыта
- Вытяжной зонт
- № стола
- Стык модулей стола

- Основа: исполнительный DWG (Long House, 10.07.2024) 1:1. Отметки: тротуар −1.170, терраса −0.450, айван и зал ±0.000.
- Кровля: стальные балки по осям, фальцевый лист Klip-Lok + утеплитель, уклон 3.5% к улице, один лист без нахлёстов, желоб вдоль улицы; низ плиты балкона +3.850. Существующий навес у южной стены с закрытым помещением над ним сохраняется: новая кровля обходит его (отступ 300 от стен, желоб вдоль западной стены, примыкания с фартуками).
- Купол в кровле один — центральный Ø5,6 (карбанди, остеклённый фонарь). Чинар у бара остаётся под навесом: крона формируется на высоте 2,2–3,0 м, над ним зенитный фонарь 3,0 × 3,0 м с резной решёткой-паньджарой. Северный чинар удаляется.
- Все отдельно стоящие столы — модули 700 × 800: пары разъединяются на 2-местные или сдвигаются в столы на 6–8 (ряды выровнены).
- Двери: C–D южная открыта; C–D северная и D–E южная закрыты (банкетка); D–E северная и E–F у лифта открыты.


ОЗЕЛЕНЕНИЕ

- **Гранат (анор) — символ Самарканда** — у входа в клумбе и в кадке у бара
- **Пеломерия (франжипани)** — в уличной клумбе, аромат вечером
- **Бугенвиллея и жасмин самбак** — по спинкам уличных скамей
- **Пальма арека** — кадки в фото-лаунже
- **Банан, стрелиция Николая** — зелёная рамка Хивинских ворот
- **Райхон, мята, базилик** — грядка у мангальной — к столу
- **Лотос, кувшинка** — в хаузе
- **Чинар у бара (существующий)** — под зенитным фонарём, формовка кроны, подсветка снизу


МАНГАЛЬНАЯ · 1:100

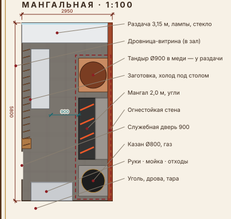


ШАТЁР-МАДЖЛИС (×2) · 1:75

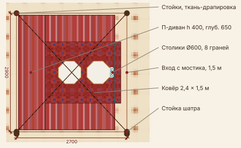

АЙВАН: СЕДИР-КАБИНКИ · 1:75

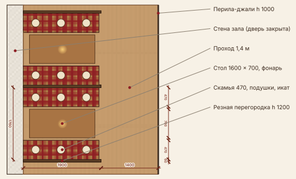

СТОЛЫ-МОДУЛИ · 1:100

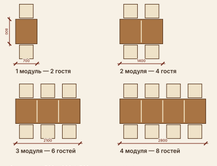

Столешница 700 × 800, h 760, вставка-зеллидж; стык на скрытых стяжках

Концепция для согласования с заказчиком · размеры уточнить на месте

designed by Nomad Group