
SAMARKAND

Covered terrace · Layout R2 · presentation plan

Tajik & Uzbek national cuisine · 254 Võ Nguyên Giáp, Đà Nẵng

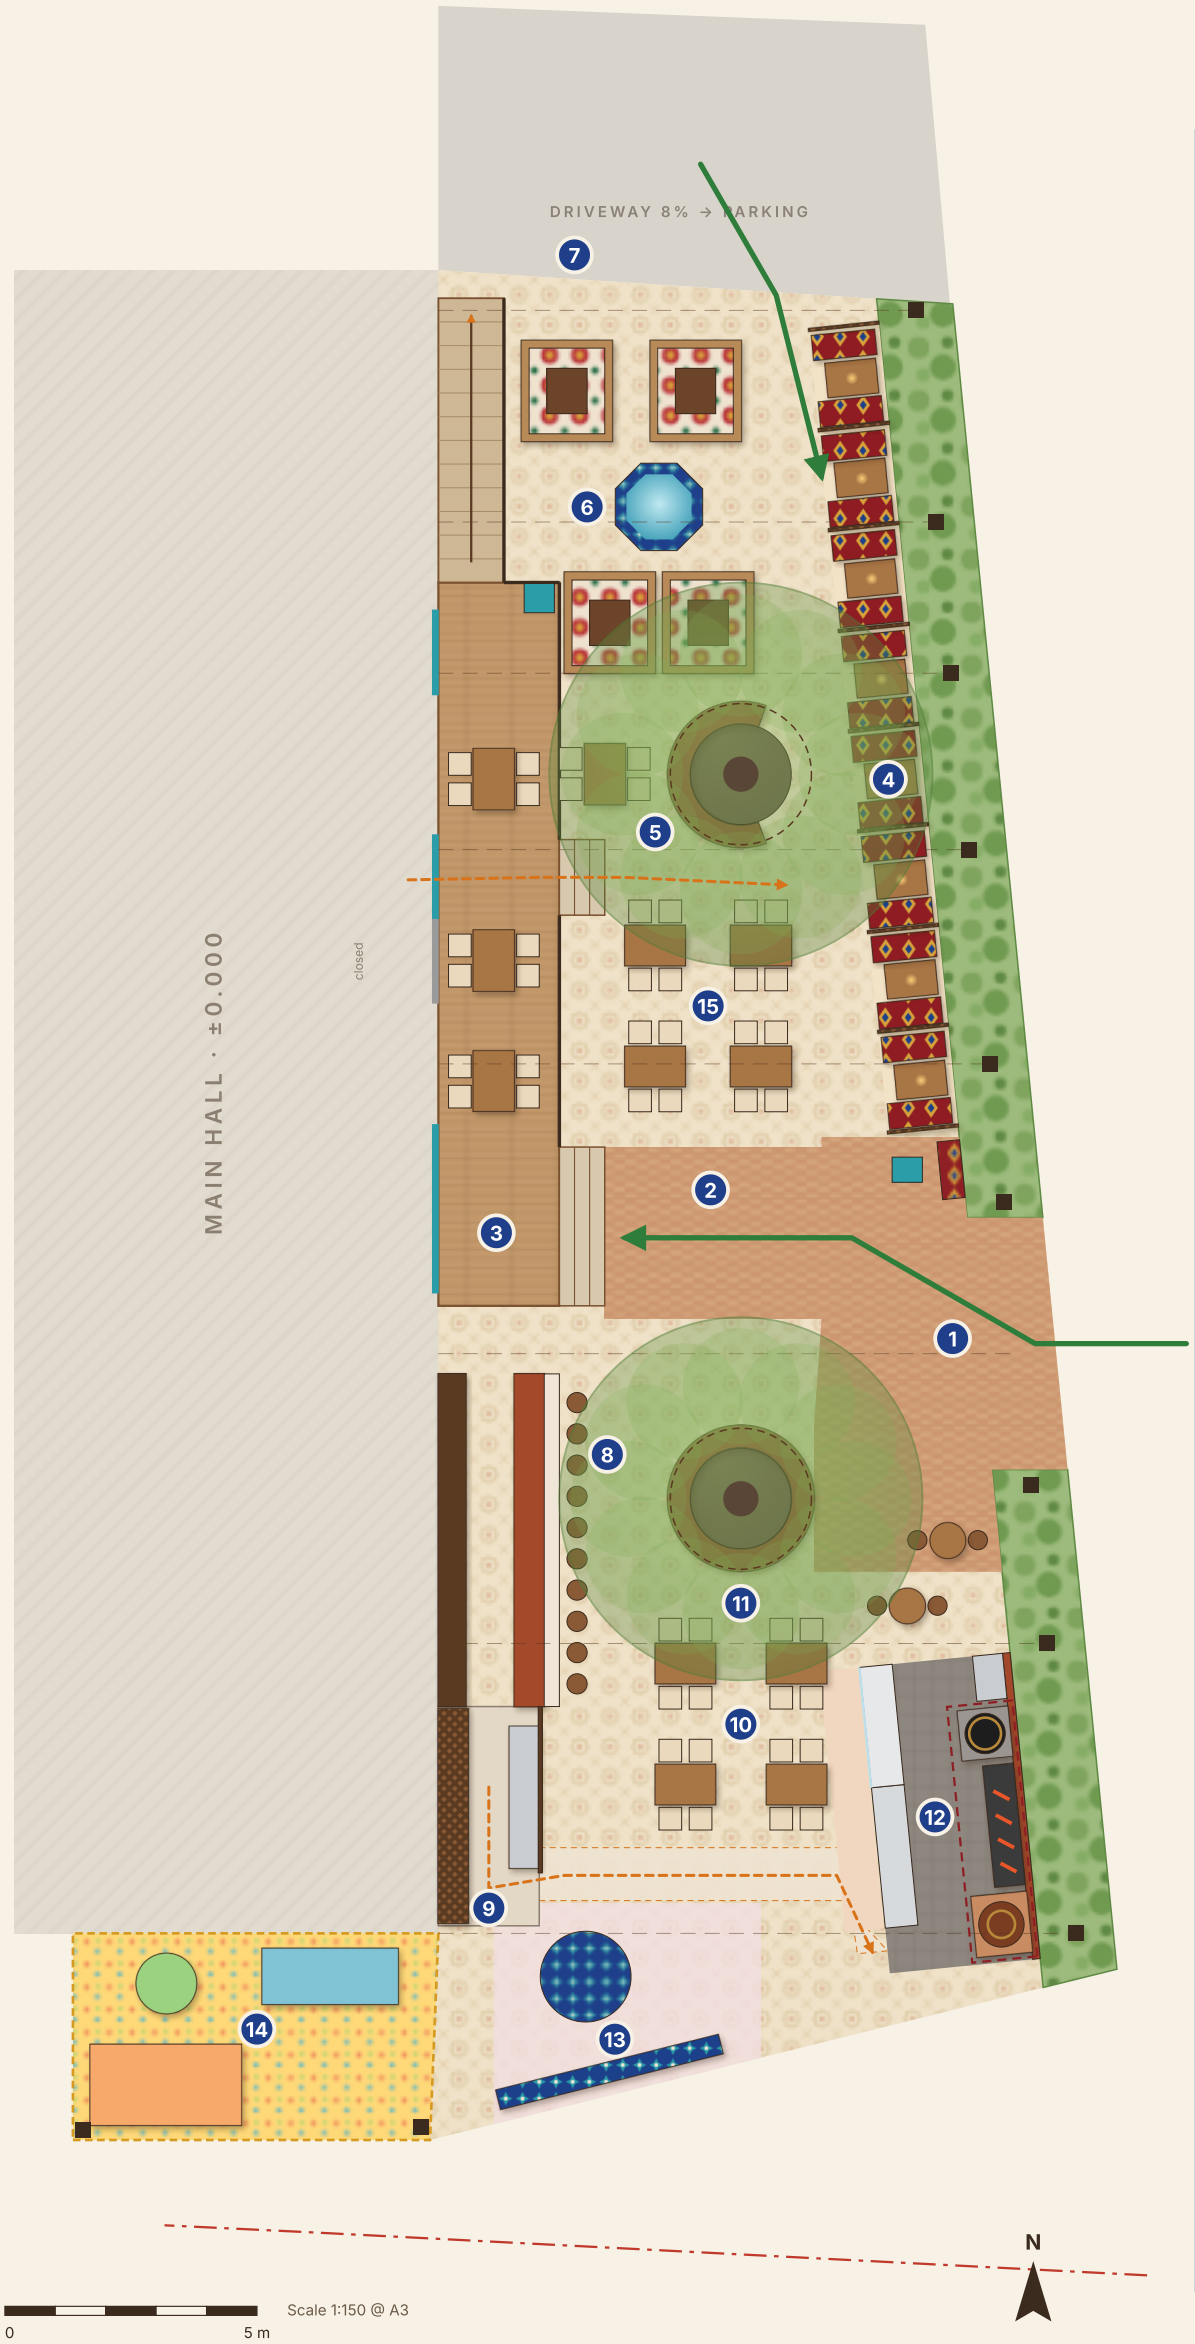

ZONES

1. **East entrance & host**
   street stair, plaza under the chinar
2. **Alley**
   patterned paving to the hall doors
3. **Raised aivan platform ±0.000**
   filled steps + extension, 3 tables, rail
4. **Sea-view booths**
   8 enclosed booths, carved screens, lanterns
5. **Chinar court north**
   tree kept, bench around it, roof oculus
6. **Lyabi-Hauz tapchan court**
   4 hybrid tapchans around a fountain
7. **North entrance + ramp 1:12**
   from parking, step-free to the hall
8. **Bar**
   tea, samovar, coffee · 10 stools
9. **Staff service station**
   shelving, POS, water, ice, dish drop
10. **Dining south**
    4 tables for 4
11. **Chinar court south**
    tree kept, round bench
12. **Mangal kitchen**
    tandoor · mangal · kazan · prep · pass
13. **Photo zone**
    majolica pishtaq + floor rosette
14. **Kids zone**
    fenced, soft floor, play
15. **Dining north**
    5 tables for 4


SEATS

Aivan platform	12
Sea-view booths	32
Chinar bench north	7
Chinar bench south	10
Dining north	20
Tapchans around the hauz	24
Bar counter	10
Dining south	16
High tables by the BBQ	4
Total	**135**

KEY

- Roof column (steel, wood-clad)
- Roof truss line
- Guest entrance
- Staff route
- Hall door, open
- Hall door, closed
- Exhaust hood

MANGAL KITCHEN · 1:100

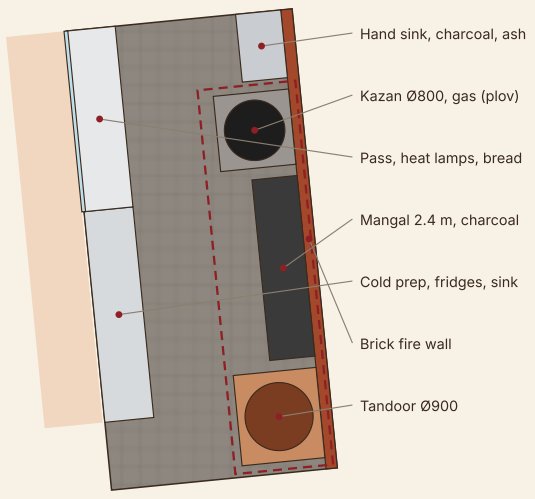

Cook aisle 1.1–1.6 m · hood + stack above the roof
Extinguisher + blanket · gas shut-off · floor drain
Glass screen to guests · non-slip slate floor

Base: as-built DWG (Long House, 10-07-2024), measured 1:1. Origin = axis 6 × axis A'. Terrace floor −0.470, platform and hall ±0.000.

Roof: steel trusses on the building grid, supported by columns hidden in the street planters and a ledger on the façade columns (engineer to confirm).

No columns inside the dining. Two trees are kept and grow through roof oculi Ø2.8. The driveway ramp and street planters are kept.

Booths face the sea over the planter. Carved panjara screens h 2.1 m, lanterns over each table, suzani and ikat textiles.

One D–E door stays closed (tables in front). The D–E north door and the back door by the lift open onto the platform.