SAMARKAND

Крытая терраса · планировка R8

Таджикская и узбекская кухня · Võ Nguyên Giáp, 254, Дананг

R6

2026-10-26

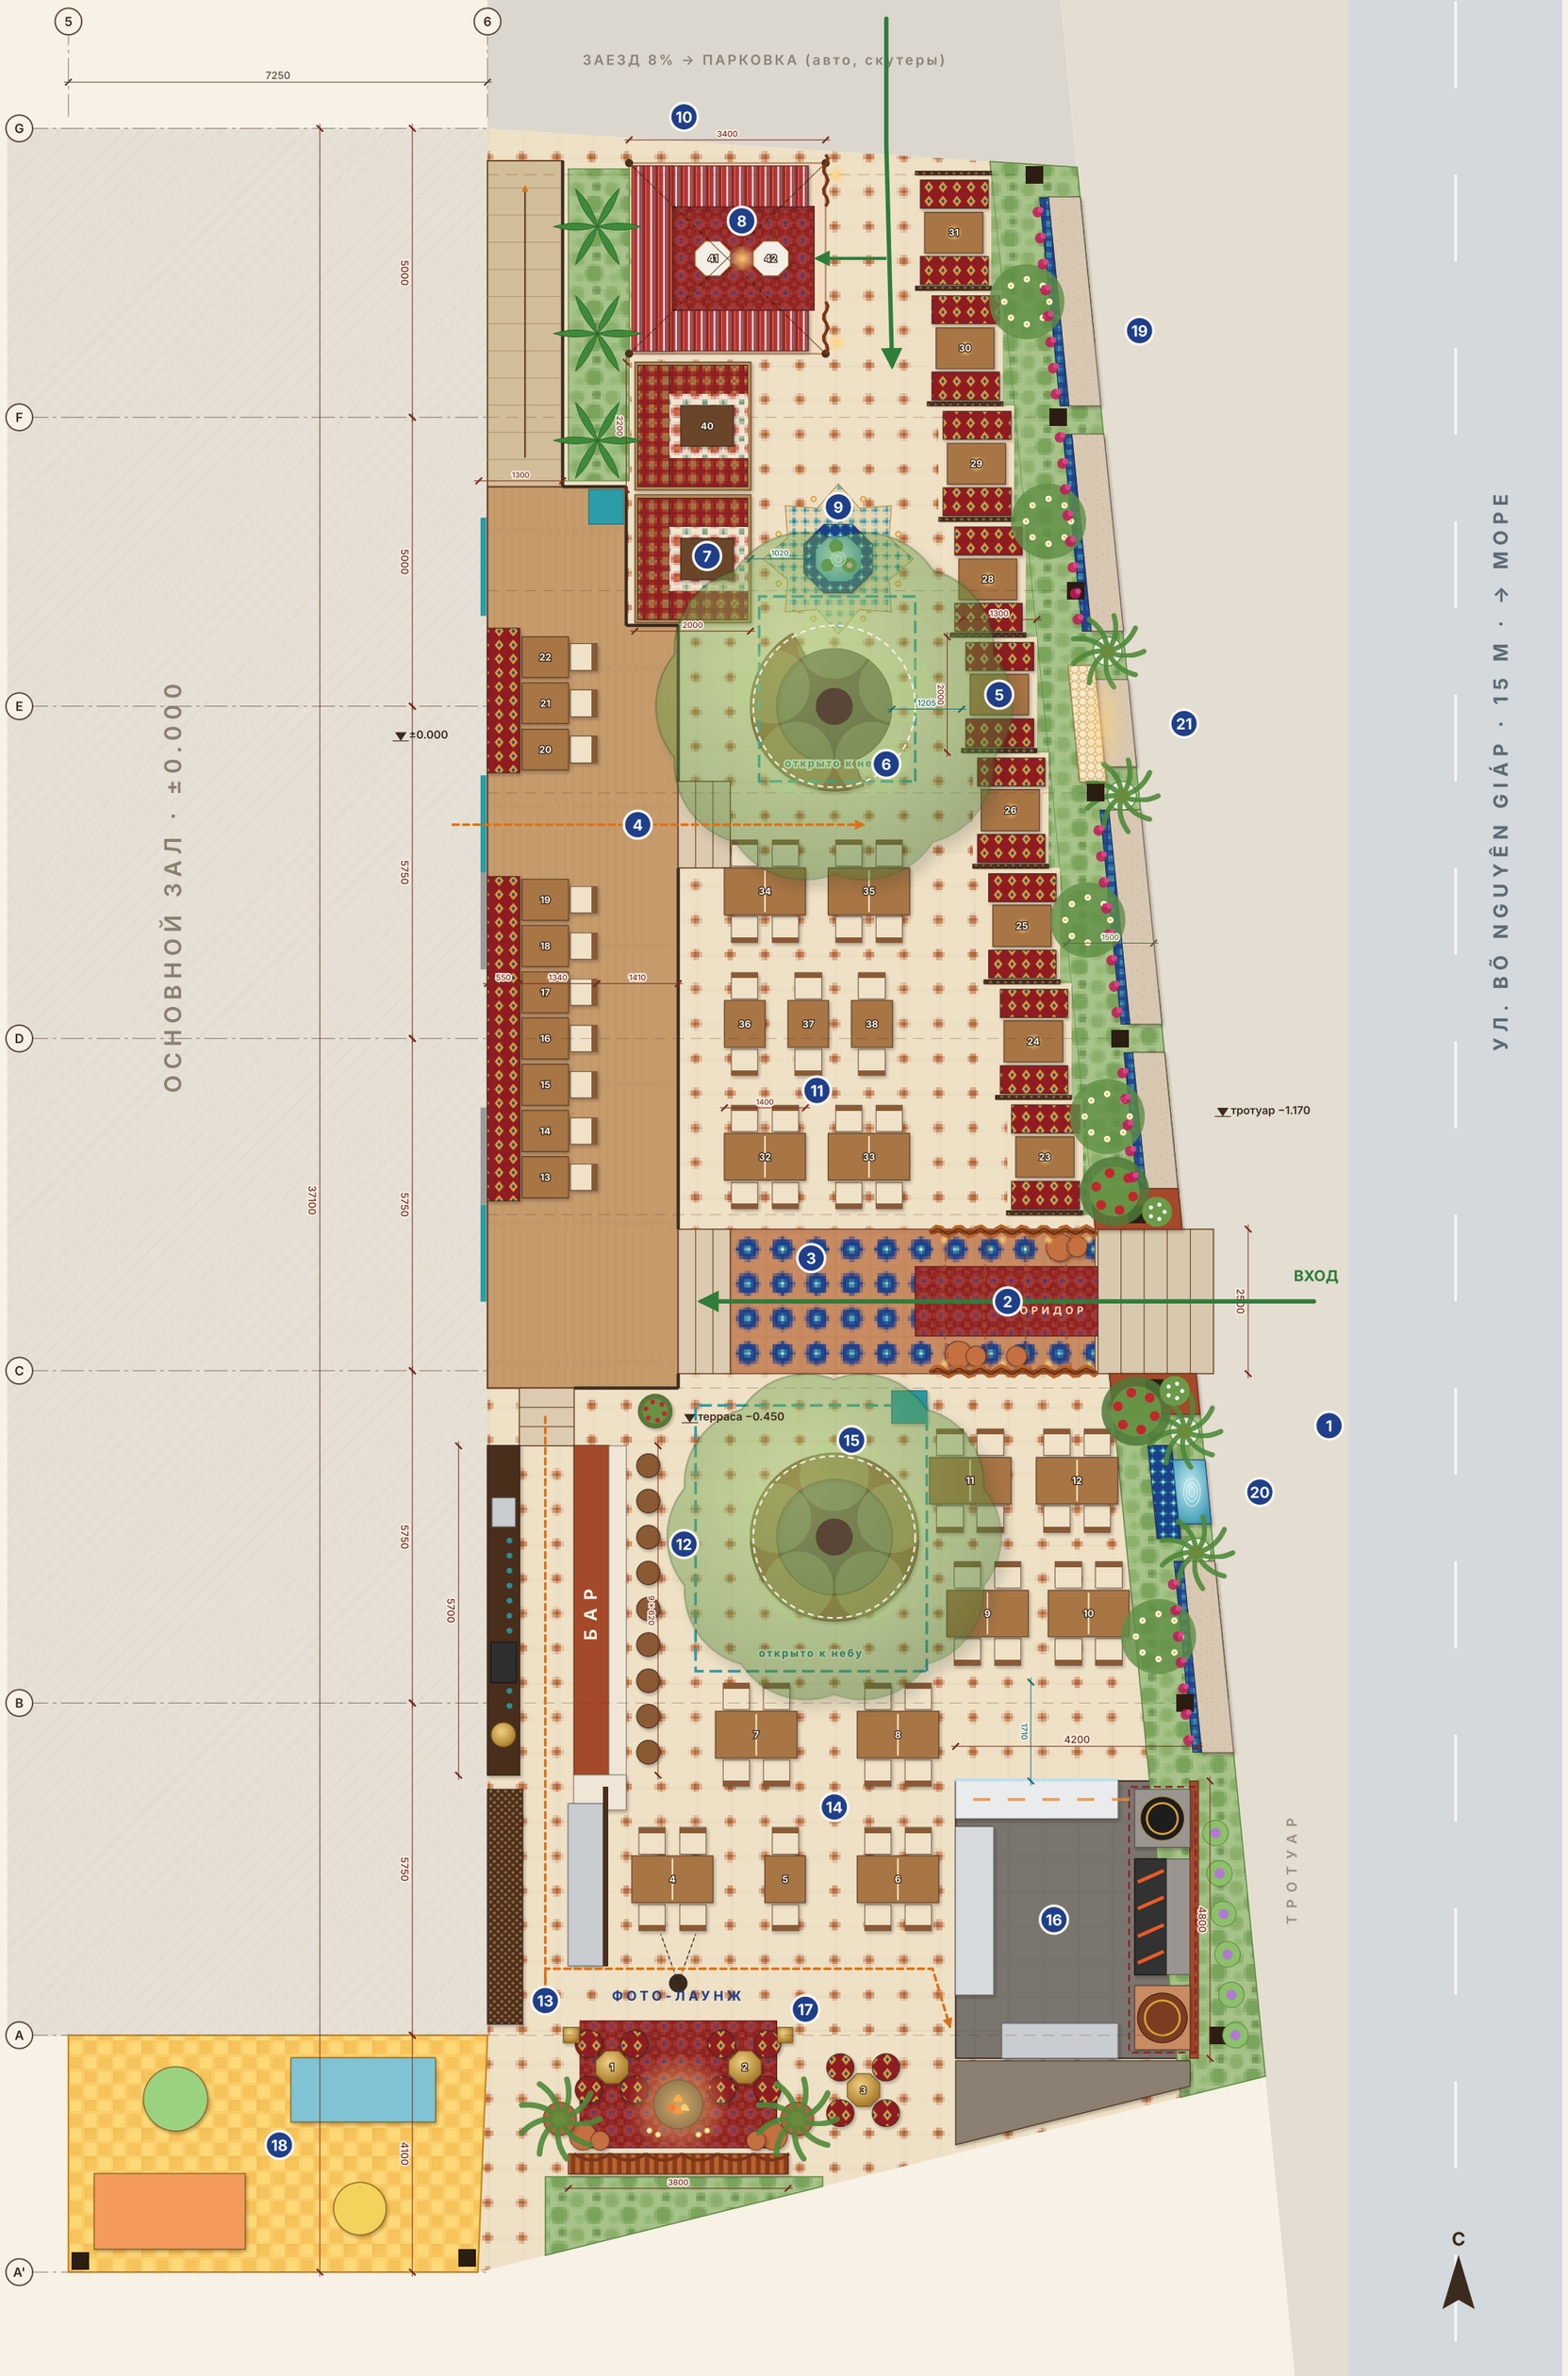

Масштаб 1:100 · А2

0 — 5 м

ЗОНЫ

1. **Главный вход · портал-пештак** — проём 2,5 м, 4 ступени с тротуара
2. **Коридор-драпировка** — бархат, ковровая дорожка, хумы, фонари
3. **Аллея к залу** — гирих, 2,5 м, хостес у выхода
4. **Айван-платформа ±0.000** — банкетка + 10 столов на 2 (сдвигаются в 4–8)
5. **Кабинки вдоль улицы** — 9 кабинок на 4, резные ширмы, фонари
6. **Чинар-дворик (север)** — открыт к небу, скамья-полукольцо
7. **Топчаны 2,0 × 2,2 м** — по 6 гостей, курпачи с 3 сторон, вход с прохода
8. **Шатёр-маджлис** — вход с востока 1,8 м, П-диван, 10 гостей
9. **Фонтан-хауз Ø1,2 м** — борт-скамья, мозаика-звезда, лотосы, подсветка
10. **Северный вход + пандус 1:12** — с парковки, без ступеней
11. **Зал север** — ряды по 4 + средний ряд из 3 столов на 2
12. **Бар** — чай, самовар, кофе · 9 стульев
13. **Станция персонала** — стеллажи, касса, вода, лёд, посуда
14. **Зал юг** — ряд 4 + 2 + 4 и ряд 4 + 4
15. **Чинар-дворик (юг) + столы у входа** — открыт к небу; 4 стола напротив мангала
16. **Мангальная 4,2 × 4,8 м** — тандыр · мангал · казан · раздача к гостям
17. **Фото-лаунж «Очаг»** — драпировки, ковры, огонь-чаша, 3 столика, 12 пуфов
18. **Детская зона** — ограждение, мягкое покрытие
19. **Уличные скамьи** — литой бетон в стенке клумбы, майолика
20. **Фонтан-себибь** — майоликовая стена, латунный носик, чаша
21. **Уличная фото-арка** — ниша со скамьёй, подсветка, пальмы

ПОСАДКА

Столы у входа	16
Скамья у чинара (юг)	10
Зал юг	18
Фото-лаунж (пуфы)	12
Барная стойка	9
Айван-платформа	20
Зал север	22
Скамья у чинара (север)	6
Кабинки	36
Топчаны (2 × 6)	12
Шатёр-маджлис	10
Итого мест в ресторане	**171**
+ уличные скамьи (вне счёта)	~35

Столы: на 2 — 14 шт., на 4 — 12 шт. (модулей 38)

ЭРГОНОМИКА · норма / по плану

Главный проход / аллея	≥1500	2500
Проход к кабинкам	≥1200	1205
Проход топчан ↔ фонтан	≥900	932
Проход на айване	≥1200	1410
Модуль стола: на 1 гостя / глубина	600–700 / 750–800	700 / 800
Край стола → спинка стула	450–600	490
Спинка–спинка (без прохода)	≥450	520
Барная стойка: высота / вынос	1050 / 250–300	1050 / 300
Шаг барных стульев	600–650	620
Рабочая зона повара	≥1200	2450
Раздача → гости	≥1500	2010
Пандус: уклон / ширина	1:12 / ≥1200	1:12 / 1300
Топчан: высота / на 1 гостя	400–450 / ≥600	450 / 700

ОБОЗНАЧЕНИЯ

- Колонна навеса (сталь, обшивка деревом)
- Ось здания
- Маршрут персонала
- Дверь зала закрыта
- Размер, мм
- Проём в кровле — открыто к небу
- Балка навеса
- Вход гостей
- Дверь зала открыта
- Вытяжной зонт
- № стола
- Стык модулей стола

· Основа: исполнительный DWG (Long House, 10.07.2024) 1:1. Отметки: тротуар −1.170, терраса −0.450, айван и зал ±0.000.

· Навес: стальные балки по осям, сэндвич-панель 50 мм, уклон 5% к улице, желоб вдоль улицы; низ плиты балкона +3.850, волна-ламели демонтируются.

· Над чинарами — открытые дворики (проём в кровле с желобом по периметру): юг 4,0 × 4,6 м, север 2,7 × 3,2 м. Под ними только всепогодные скамьи.

· Все отдельно стоящие столы — модули 700 × 800: пары разъединяются на 2-местные или сдвигаются в столы на 6–8 (ряды выровнены).

· Двери: C–D южная открыта; C–D северная и D–E южная закрыты (банкетка); D–E северная и E–F у лифта открыты.

ОЗЕЛЕНЕНИЕ

- **Гранат (анор) — символ Самарканда** — у входа в клумбе и в кадке у бара
- **Плюмерия (франжипани)** — в уличной клумбе, аромат вечером
- **Бугенвиллия** — по спинкам скамей и колоннам
- **Жасмин самбак** — у портала входа
- **Пальма арека** — кадки в фото-лаунже
- **Банан, стрелиция Николая** — зелёная стена за топчанами и шатром
- **Райхон, мята, базилик** — грядка у мангальной — к столу
- **Лотос, кувшинка** — в хаузе
- **Чинары (существующие)** — открытые дворики, подсветка снизу

МАНГАЛЬНАЯ · 1:75

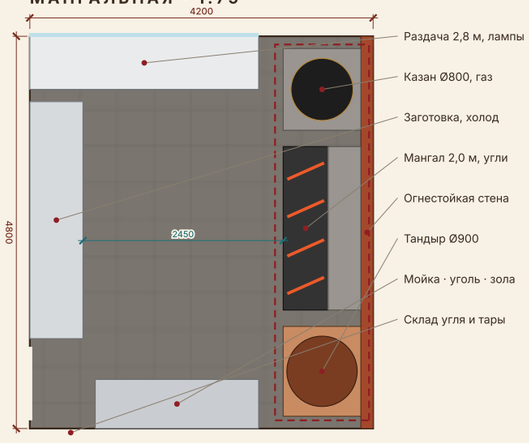

ШАТЁР-МАДЖЛИС · 1:75

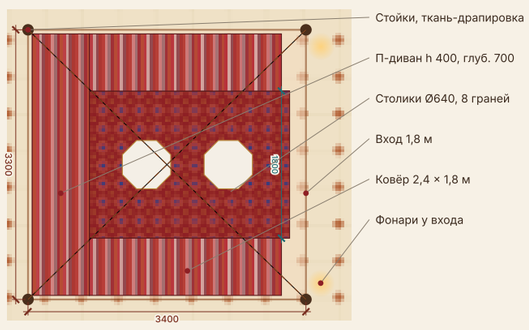

УЛИЧНАЯ СКАМЬЯ · РАЗРЕЗ 1:60

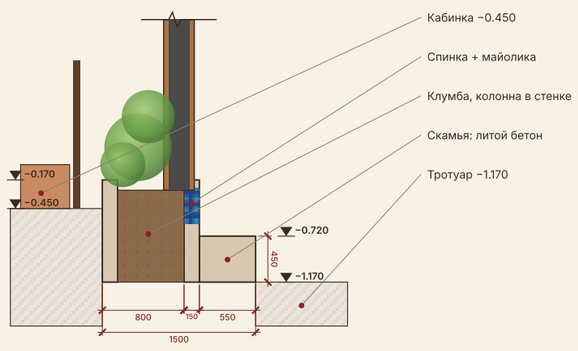

СТОЛЫ-МОДУЛИ · 1:100

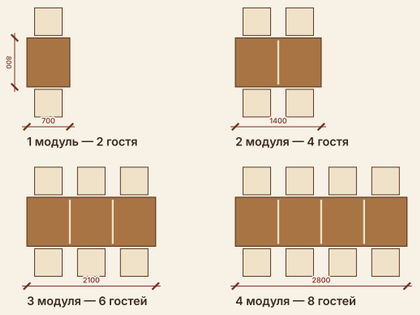

Столешница 700 × 800, h 750; стык на скрытых стяжках

Концепция для согласования с заказчиком · размеры уточнить на месте