CÔNG TY TNHH THIẾT KẾ VÀ XÂY DỰNG
LONG HOUSE

Add: 348 Nguyễn Hữu Thọ - Q.Hải Châu - TP. Đà Nẵng
Tel: 0905.768.505
Mst: 0402159230
Email: longhouseart@gmail.com

BẢN VẼ HOÀN CÔNG

DỰ ÁN: NHÀ HÀNG HẢI SẢN


GÓI THẦU: THI CÔNG XÂY DỰNG

CHỦ ĐẦU TƯ: CÔNG TY TNHH MTV NGỌC QUANG ĐĂNG

NHÀ THẦU THI CÔNG: CÔNG TY TNHH XD VŨ ANH KHOA

ĐỊA CHỈ: 254 VÕ NGUYÊN GIÁP - P. PHƯỚC MỸ - Q. SƠN TRÀ - TP.ĐÀ NẴNG

ĐÀ NẴNG: 10-07-2024

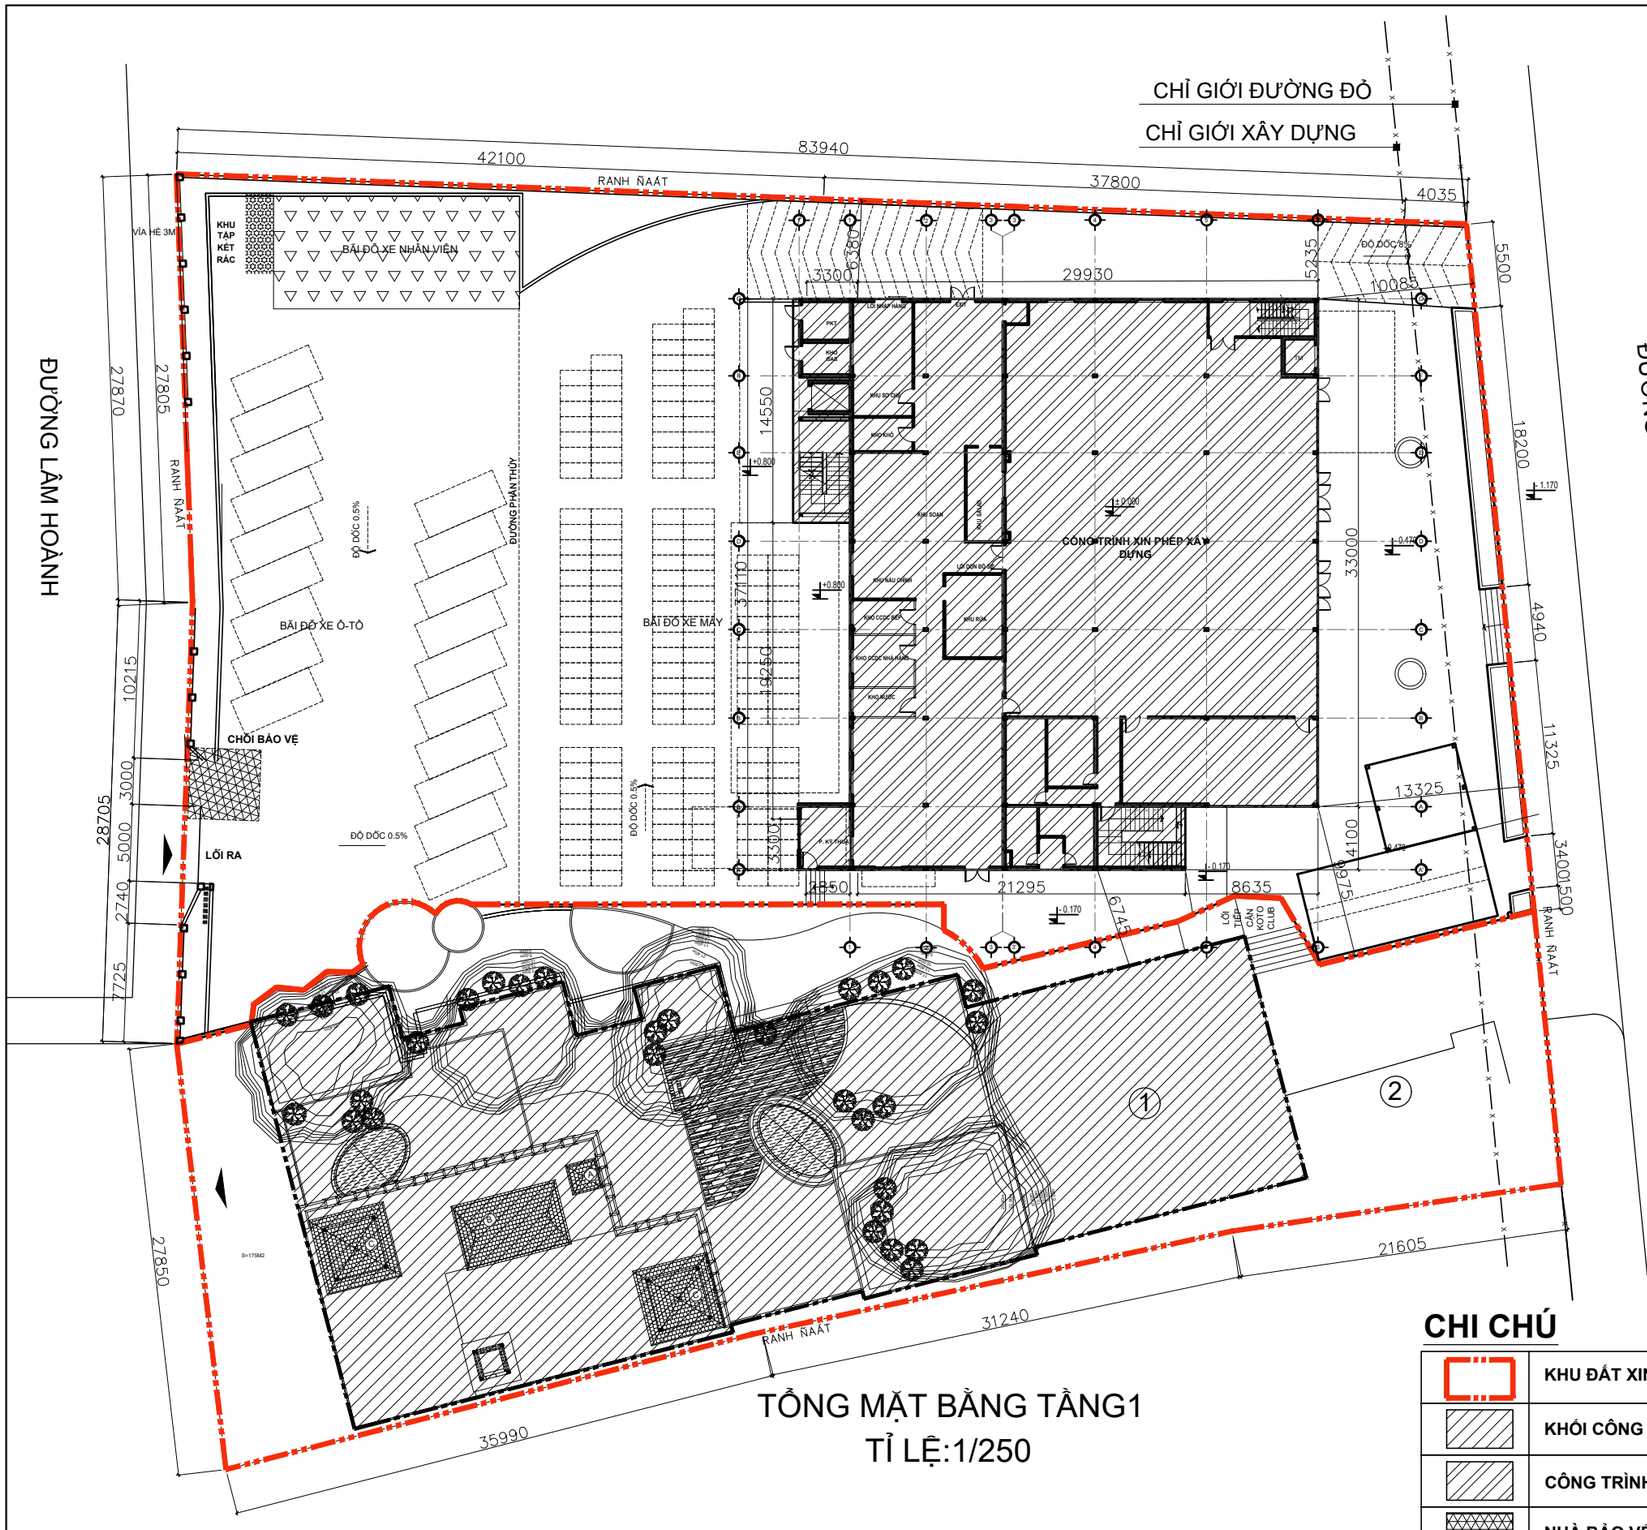

TỔNG MẶT BẰNG TẦNG1
TỈ LỆ:1/250

CHI CHÚ

	KHU ĐẤT XIN PHÉP XÂY DỰNG
	KHỐI CÔNG TRÌNH HIỆN TRẠNG
	CÔNG TRÌNH XIN PHÉP
	NHÀ BẢO VỆ
	NHÀ XE NHÂN VIÊN
	KHU TẬP KẾT RÁC
	KHU HẢI SẢN

MÔ TẢ ĐỊA ĐIỂM: 254 VÕ NGUYÊN GIÁP - P. PHƯỚC MỸ - Q SƠN TRÀ - TP ĐÀ NẴNG.

1. PHÍA ĐÔNG: GIÁP ĐƯỜNG VÕ NGUYÊN GIÁP
2. PHÍA NAM: GIÁP KHU ĐẤT QUÂN ĐỘI T20
3. PHÍA TÂY: GIÁP TỔ 14 KHU DÂN CƯ PHƯỜNG PHƯỚC MỸ
4. PHÍA BẮC: GIÁP KHU ĐẤT QUÂN ĐỘI QUÂN KHU 5

GHI CHÚ:

- TRƯỚC KHI THI CÔNG TẤT CẢ CÁC KÍCH THƯỚC ĐỀU PHẢI ĐƯỢC KIỂM TRA THỰC TẾ TẠI CÔNG TRƯỜNG. KHÔNG SỬ DỤNG THƯỚC ĐỂ ĐO KÍCH THƯỚC TRỰC TIẾP TRÊN BẢN VẼ.
- BẢN VẼ NÀY PHẢI ĐƯỢC KẾT HỢP CÙNG VỚI CÁC BẢN VẼ KHÁC CÓ LIÊN QUAN. TRONG TRƯỜNG HỢP CÓ SỰ MÂU THUẪN GIỮA CÁC BẢN VẼ THÌ ĐƠN VỊ THI CÔNG PHẢI THÔNG BÁO CHO ĐƠN VỊ QUẢN LÝ XÂY DỰNG VÀ ĐƠN VỊ THIẾT KẾ BẰNG VĂN BẢN.
- CAO ĐỘ TRONG BẢN VẼ LÀ CAO ĐỘ HOÀN THIỆN.

CHỦ ĐẦU TƯ

CT TNHH MTV NGỌC QUANG ĐĂNG

TP. ĐÀ NẴNG

CÔNG TY TNHH THIẾT KẾ VÀ XÂY DỰNG
LONG HOUSE
Add: 348 Nguyễn Hữu Thọ - Q.Hải Châu - TP. Đà Nẵng
Tel: 0905.768.505
Mst: 0402159230
Email: longhouseart@gmail.com

GIÁM ĐỐC	NGUYỄN THÀNH Ý	
CHỦ TRÌ KIẾN TRÚC	KTS. TRƯƠNG QUANG PHÙNG	
THIẾT KẾ	KTS. NGUYỄN KHOA TRƯỜNG	
QUẢN LÝ KỸ THUẬT	KTS. TRƯƠNG QUANG PHÙNG	


CÔNG TRÌNH : NHÀ HÀNG VÀ COFFEE

ĐỊA CHỈ : 254 VÕ NGUYÊN GIÁP - TP ĐÀ NẴNG

TEÂN BAÛN VEÕ :

TỔNG MẶT BẰNG TẦNG1
TỈ LỆ:1/250

TYÛ LEÄ 1/100 NGAØY THAØNH 2024 BAÛN VEÕ

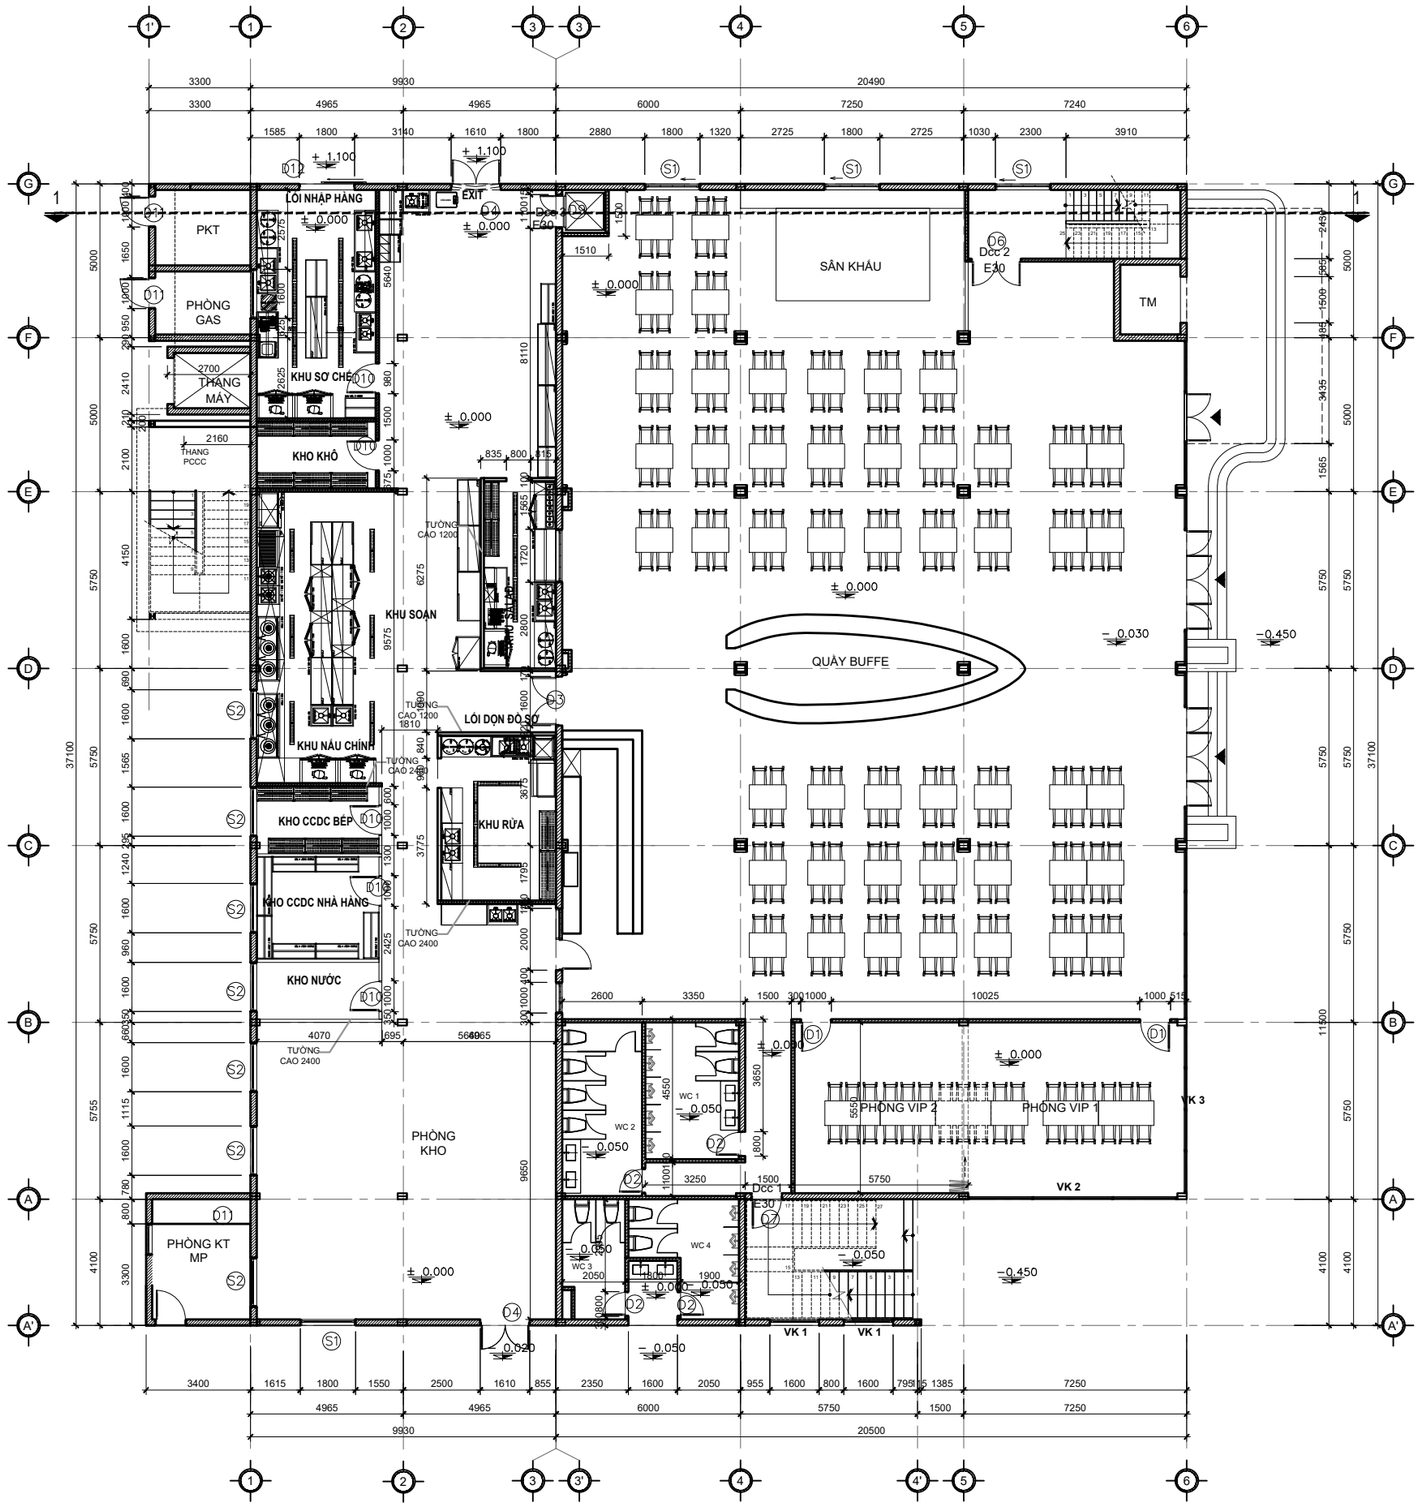

MẶT BẰNG BỐ TRÍ TẦNG 1

GHI CHÚ

– TRƯỚC KHI THI CÔNG TẤT CẢ CÁC KÍCH THƯỚC ĐỀU PHẢI ĐƯỢC KIỂM TRA THỰC TẾ TẠI CÔNG TRƯỜNG. KHÔNG SỬ DỤNG THƯỚC ĐỂ ĐO KÍCH THƯỚC TRỰC TIẾP TRÊN BẢN VẼ.
– BẢN VẼ NÀY PHẢI ĐƯỢC KẾT HỢP CÙNG VỚI CÁC BẢN VẼ KHÁC CÓ LIÊN QUAN. TRONG TRƯỜNG HỢP CÓ SỰ MÂU THUẪN GIỮA CÁC BẢN VẼ THÌ ĐƠN VỊ THI CÔNG PHẢI THÔNG BÁO CHO ĐƠN VỊ QUẢN LÝ XÂY DỰNG VÀ ĐƠN VỊ THIẾT KẾ BẰNG VĂN BẢN.
– CAO ĐỘ TRONG BẢN VẼ LÀ CAO ĐỘ HOÀN THIỆN.

CHUÛ ÑAÀU TÖ :

CT TNHH MTV NGỌC QUANG ĐĂNG

TP. ĐÀ NẴNG

CÔNG TY TNHH THIẾT KẾ VÀ XÂY DỰNG
LONG HOUSE
Add: 348 Nguyễn Hữu Thọ - Q.Hải Châu - TP. Đà Nẵng
Tel: 0905.768.505
Mst: 0402159230
Email: longhouseart@gmail.com

GIÁM ĐỐC	NGUYỄN THÀNH Ý	
CHỦ TRÌ KIẾN TRÚC	KTS. TRƯƠNG QUANG PHÙNG	
THIẾT KẾ	KTS. NGUYỄN KHOA TRƯỜNG	
QUẢN LÝ KỸ THUẬT	KTS. TRƯƠNG QUANG PHÙNG	


CÔNG TRÌNH : NHÀ HÀNG VÀ COFFEE

ĐỊA CHỈ : 254 VÕ NGUYÊN GIÁP - TP ĐÀ NẴNG

TEÂN BAÛN VEÕ :

MẶT BẰNG BỐ TRÍ TẦNG 1

TYÛ LEÄ 1/100 | ÑAØN THAØNH 2024 | BAÛN VEÕ

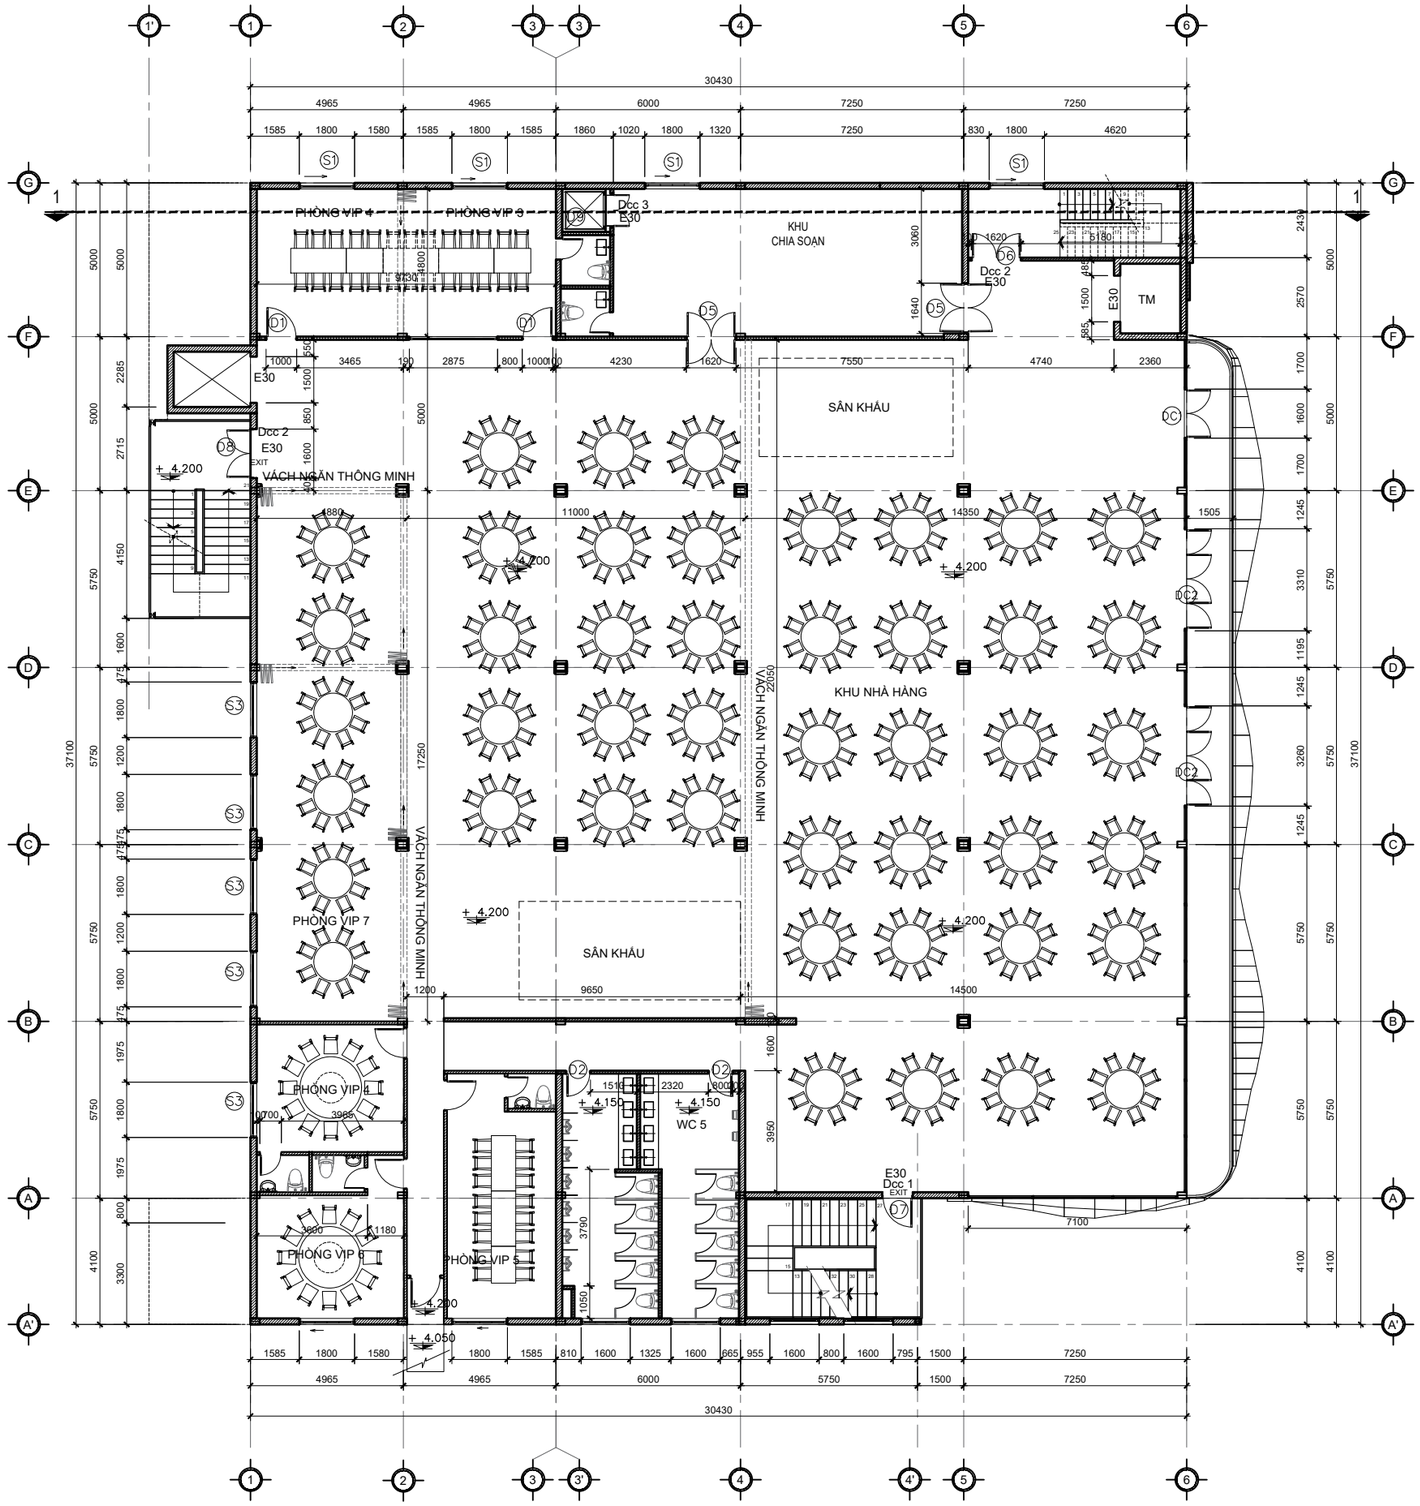

MẶT BẰNG BỐ TRÍ TẦNG 2

GHI CHÚ :

– TRƯỚC KHI THI CÔNG TẤT CẢ CÁC KÍCH THƯỚC ĐỀU PHẢI ĐƯỢC KIỂM TRA THỰC TẾ TẠI CÔNG TRƯỜNG. KHÔNG SỬ DỤNG THƯỚC ĐỂ ĐO KÍCH THƯỚC TRỰC TIẾP TRÊN BẢN VẼ.
– BẢN VẼ NÀY PHẢI ĐƯỢC KẾT HỢP CÙNG VỚI CÁC BẢN VẼ KHÁC CÓ LIÊN QUAN. TRONG TRƯỜNG HỢP CÓ SỰ MÂU THUẪN GIỮA CÁC BẢN VẼ THÌ ĐƠN VỊ THI CÔNG PHẢI THÔNG BÁO CHO ĐƠN VỊ QUẢN LÝ XÂY DỰNG VÀ ĐƠN VỊ THIẾT KẾ BẰNG VĂN BẢN.
– CAO ĐỘ TRONG BẢN VẼ LÀ CAO ĐỘ HOÀN THIỆN.

CHỦ ĐẦU TƯ :

CT TNHH MTV NGỌC QUANG ĐĂNG

TP. ĐÀ NẴNG

CÔNG TY TNHH THIẾT KẾ VÀ XÂY DỰNG
LONG HOUSE
Add: 348 Nguyễn Hữu Thọ - Q.Hải Châu - TP. Đà Nẵng
Tel: 0905.768.505
Mst: 0402159230
Email: longhouseart@gmail.com

GIÁM ĐỐC	NGUYỄN THÀNH Ý	
CHỦ TRÌ KIẾN TRÚC	KTS. TRƯƠNG QUANG PHÙNG	
THIẾT KẾ	KTS. NGUYỄN KHOA TRƯỜNG	
QUẢN LÝ KỸ THUẬT	KTS. TRƯƠNG QUANG PHÙNG	


CÔNG TRÌNH : NHÀ HÀNG VÀ COFFEE

ĐỊA CHỈ : 254 VÕ NGUYÊN GIÁP - TP ĐÀ NẴNG

TEÂN BAÛN VEÕ :

MẶT BẰNG BỐ TRÍ TẦNG 2

TYÛ LEÄ 1/100 | NGAØY THAØNH 2024 | BAÛN VEÕ

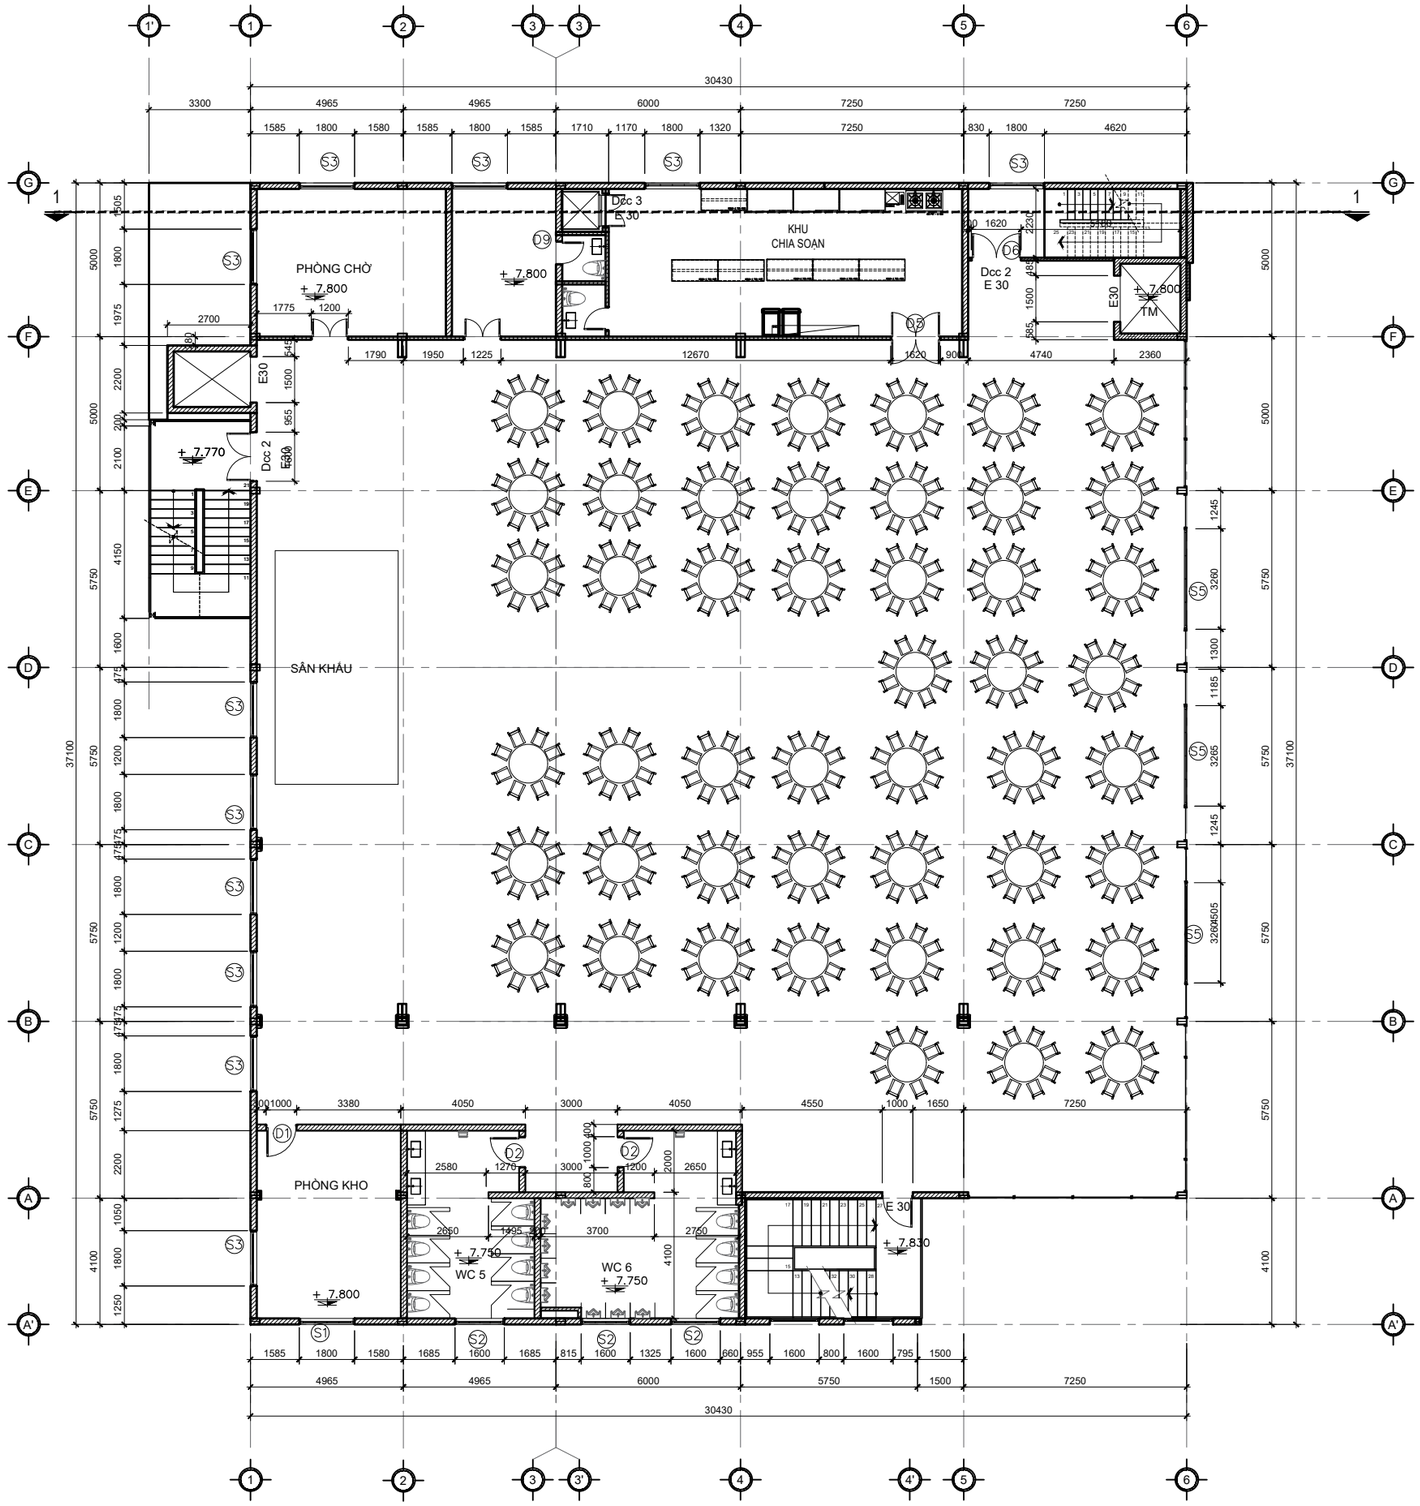

MẶT BẰNG BỐ TRÍ TẦNG 3

GHI CHÚ

– TRƯỚC KHI THI CÔNG TẤT CẢ CÁC KÍCH THƯỚC ĐỀU PHẢI ĐƯỢC KIỂM TRA THỰC TẾ TẠI CÔNG TRƯỜNG. KHÔNG SỬ DỤNG THƯỚC ĐỂ ĐO KÍCH THƯỚC TRỰC TIẾP TRÊN BẢN VẼ.
– BẢN VẼ NÀY PHẢI ĐƯỢC KẾT HỢP CÙNG VỚI CÁC BẢN VẼ KHÁC CÓ LIÊN QUAN. TRONG TRƯỜNG HỢP CÓ SỰ MÂU THUẪN GIỮA CÁC BẢN VẼ THÌ ĐƠN VỊ THI CÔNG PHẢI THÔNG BÁO CHO ĐƠN VỊ QUẢN LÝ XÂY DỰNG VÀ ĐƠN VỊ THIẾT KẾ BẰNG VĂN BẢN.
– CAO ĐỘ TRONG BẢN VẼ LÀ CAO ĐỘ HOÀN THIỆN.

CHỦ ĐẦU TƯ:

CT TNHH MTV NGỌC QUANG ĐĂNG

TP. ĐÀ NẴNG

CÔNG TY TNHH THIẾT KẾ VÀ XÂY DỰNG
LONG HOUSE
Add: 348 Nguyễn Hữu Thọ - Q.Hải Châu - TP. Đà Nẵng
Tel: 0905.768.505
Mst: 0402159230
Email: longhouseart@gmail.com

GIÁM ĐỐC	NGUYỄN THÀNH Ý	
CHỦ TRÌ KIẾN TRÚC	KTS. TRƯƠNG QUANG PHÙNG	
THIẾT KẾ	KTS. NGUYỄN KHOA TRƯỜNG	
QUẢN LÝ KỸ THUẬT	KTS. TRƯƠNG QUANG PHÙNG	


CÔNG TRÌNH : NHÀ HÀNG VÀ COFFEE

ĐỊA CHỈ : 254 VÕ NGUYÊN GIÁP - TP ĐÀ NẴNG

TEÂN BAÛN VEÕ :

MẶT BẰNG BỐ TRÍ TẦNG 3

TYÛ LEÄ 1/100 NGAØY THAØNH 2024 BAÛN VEÕ

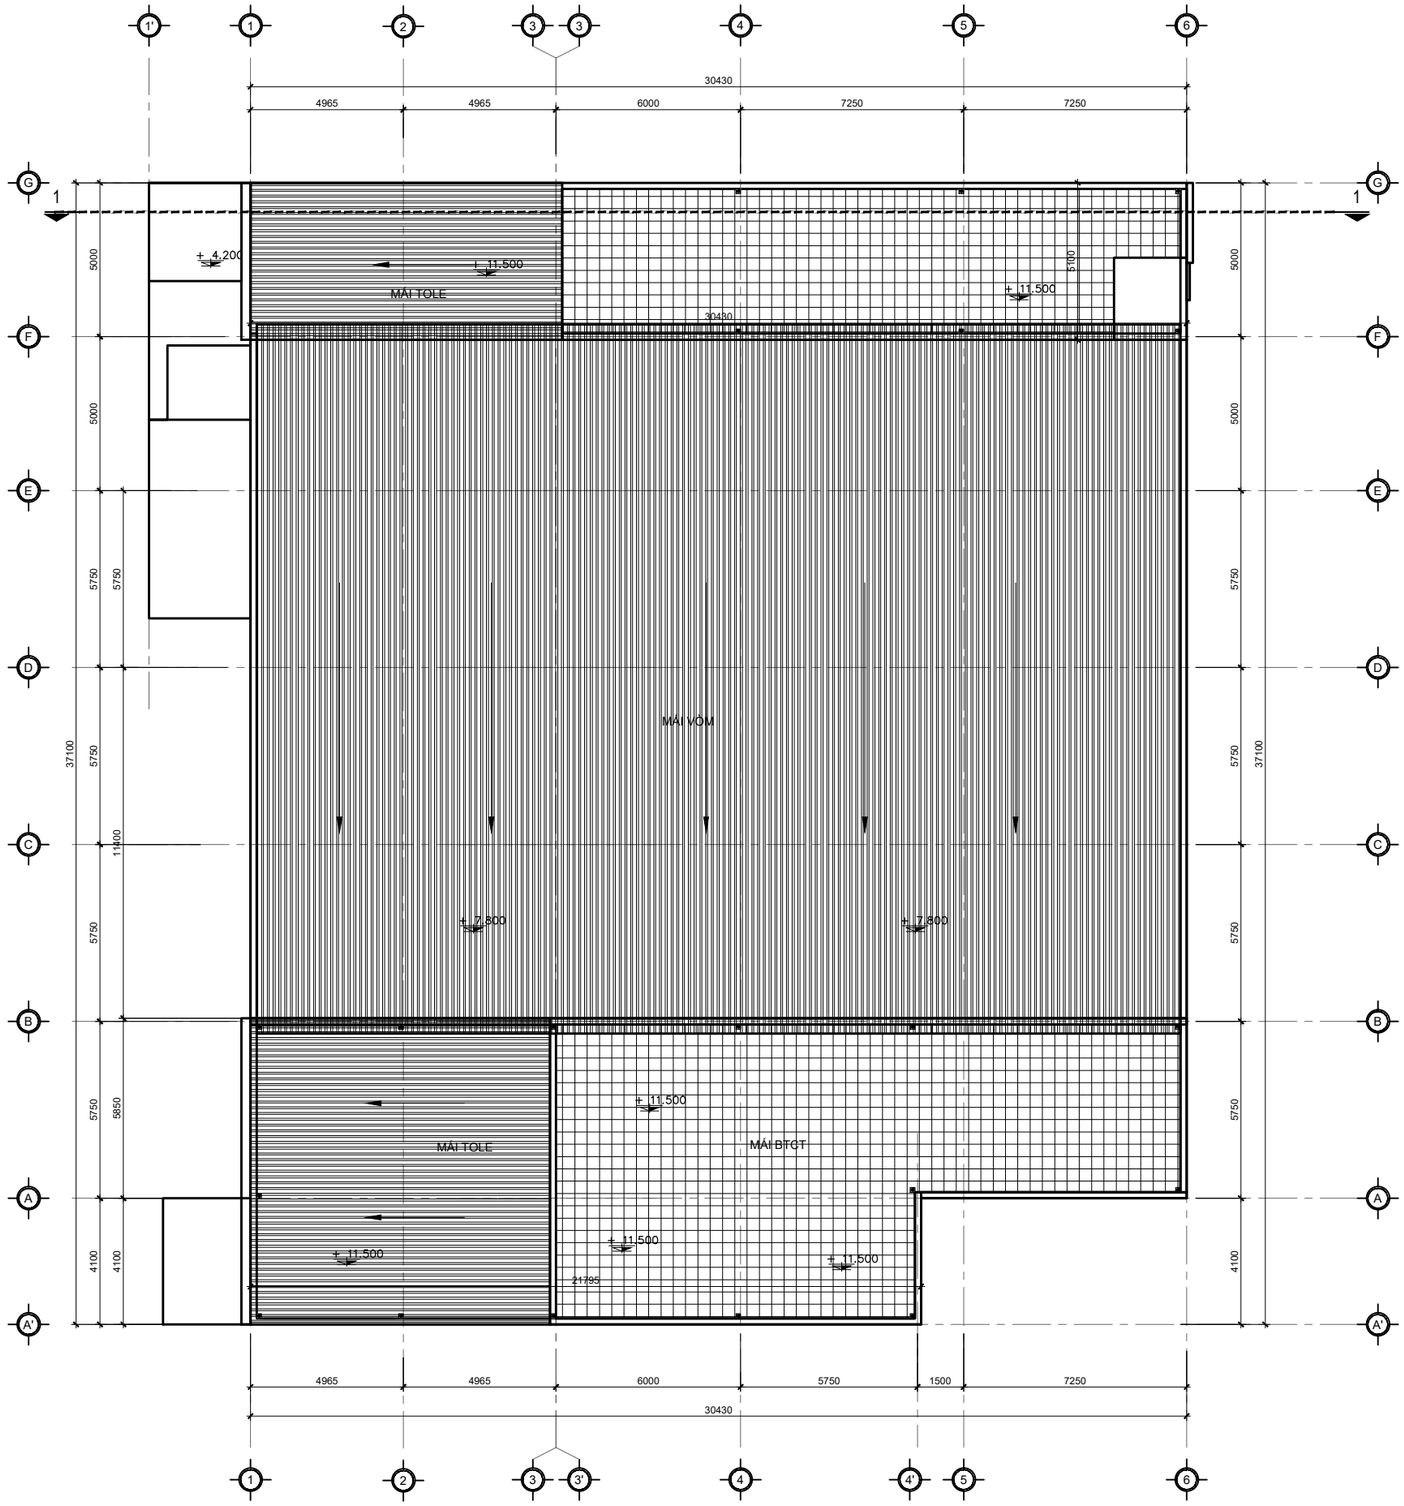

MẶT BẰNG MÁI

GHI CHÚ

– TRƯỚC KHI THI CÔNG TẤT CẢ CÁC KÍCH THƯỚC ĐỀU PHẢI ĐƯỢC KIỂM TRA THỰC TẾ TẠI CÔNG TRƯỜNG. KHÔNG SỬ DỤNG THƯỚC ĐỂ ĐO KÍCH THƯỚC TRỰC TIẾP TRÊN BẢN VẼ.
– BẢN VẼ NÀY PHẢI ĐƯỢC KẾT HỢP CÙNG VỚI CÁC BẢN VẼ KHÁC CÓ LIÊN QUAN. TRONG TRƯỜNG HỢP CÓ SỰ MÂU THUẪN GIỮA CÁC BẢN VẼ THÌ ĐƠN VỊ THI CÔNG PHẢI THÔNG BÁO CHO ĐƠN VỊ QUẢN LÝ XÂY DỰNG VÀ ĐƠN VỊ THIẾT KẾ BẰNG VĂN BẢN.
– CAO ĐỘ TRONG BẢN VẼ LÀ CAO ĐỘ HOÀN THIỆN.

CHỦ ĐẦU TƯ:

CT TNHH MTV NGỌC QUANG ĐĂNG

TP. ĐÀ NẴNG

CÔNG TY TNHH THIẾT KẾ VÀ XÂY DỰNG
LONG HOUSE
Add: 348 Nguyễn Hữu Thọ - Q.Hải Châu - TP. Đà Nẵng
Tel: 0905.768.505
Mst: 0402159230
Email: longhouseart@gmail.com

GIÁM ĐỐC	NGUYỄN THÀNH Ý	
CHỦ TRÌ KIẾN TRÚC	KTS. TRƯƠNG QUANG PHÙNG	
THIẾT KẾ	KTS. NGUYỄN KHOA TRƯỜNG	
QUẢN LÝ KỸ THUẬT	KTS. TRƯƠNG QUANG PHÙNG	


CÔNG TRÌNH : NHÀ HÀNG VÀ COFFEE

ĐỊA CHỈ : 254 VÕ NGUYÊN GIÁP - TP ĐÀ NẴNG

TEÂN BAÛN VEÕ :

MẶT BẰNG MÁI

TYÛ LEÄ 1/100	NGAØY THAØNG 2024	BAÛN VEÕ

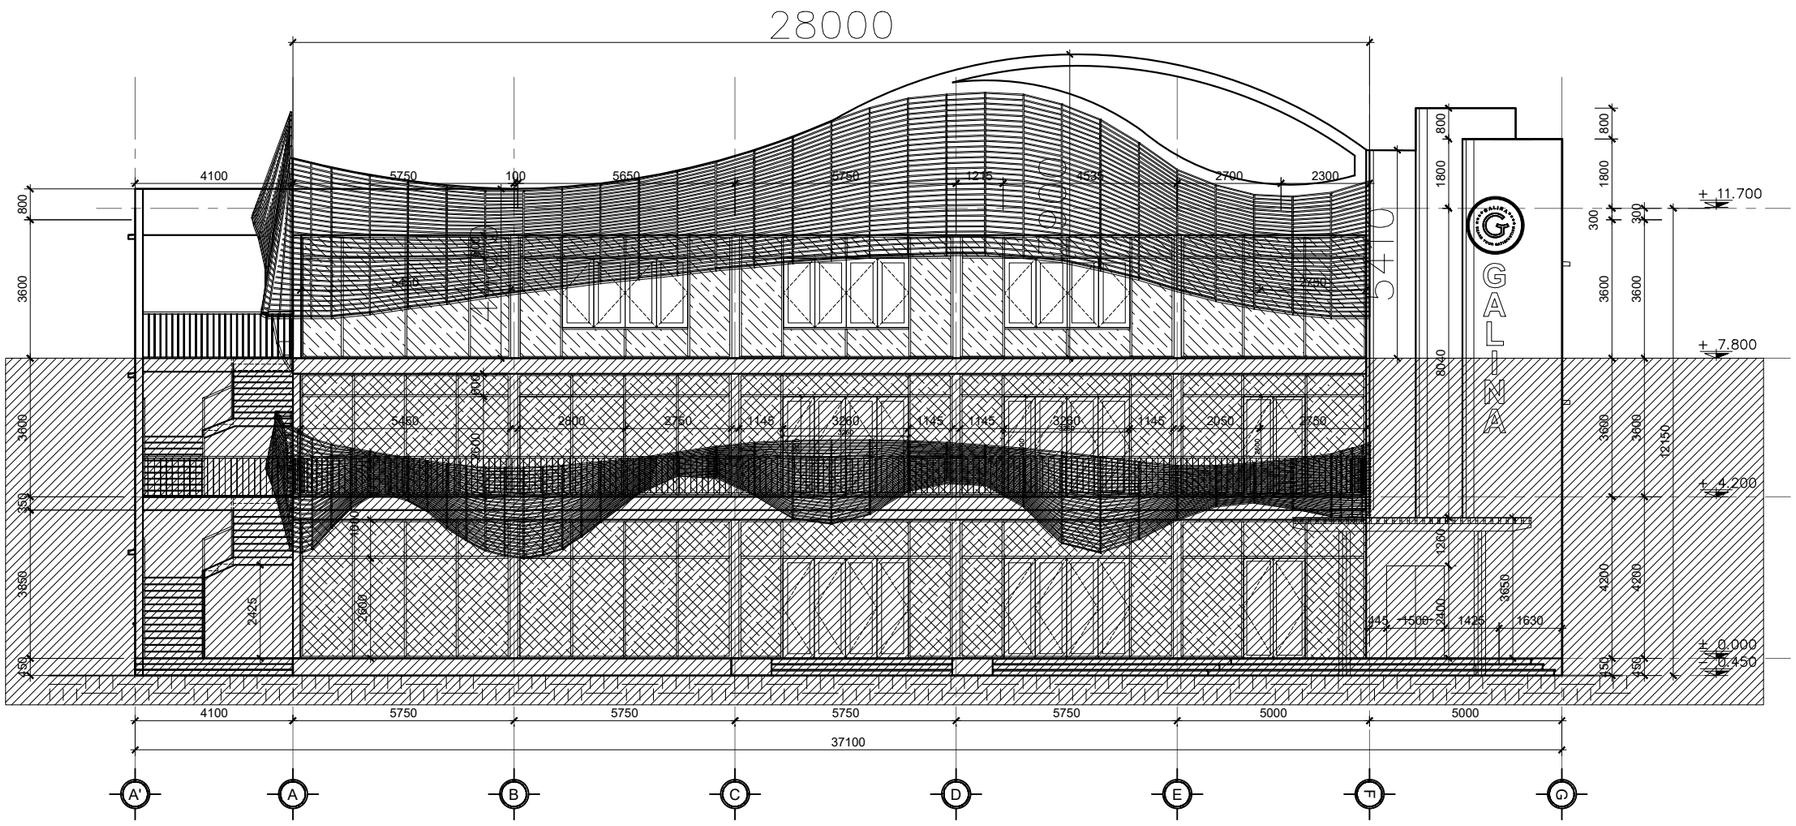

MẶT ĐỨNG A'-H

GHI CHUÙ :

– TRƯỚC KHI THI CÔNG TẤT CẢ CÁC KÍCH THƯỚC ĐỀU PHẢI ĐƯỢC KIỂM TRA THỰC TẾ TẠI CÔNG TRƯỜNG. KHÔNG SỬ DỤNG THƯỚC ĐỂ ĐO KÍCH THƯỚC TRỰC TIẾP TRÊN BẢN VẼ.
– BẢN VẼ NÀY PHẢI ĐƯỢC KẾT HỢP CÙNG VỚI CÁC BẢN VẼ KHÁC CÓ LIÊN QUAN. TRONG TRƯỜNG HỢP CÓ SỰ MÂU THUẪN GIỮA CÁC BẢN VẼ THÌ ĐƠN VỊ THI CÔNG PHẢI THÔNG BÁO CHO ĐƠN VỊ QUẢN LÝ XÂY DỰNG VÀ ĐƠN VỊ THIẾT KẾ BẰNG VĂN BẢN.
– CAO ĐỘ TRONG BẢN VẼ LÀ CAO ĐỘ HOÀN THIỆN.

CHỦ ĐẦU TƯ:

CT TNHH MTV NGỌC QUANG ĐĂNG

TP. ĐÀ NẴNG

CÔNG TY TNHH THIẾT KẾ VÀ XÂY DỰNG
LONG HOUSE
Add: 348 Nguyễn Hữu Thọ - Q.Hải Châu - TP. Đà Nẵng
Tel: 0905.768.505
Mst: 0402159230
Email: longhouseart@gmail.com

GIÁM ĐỐC	NGUYỄN THÀNH Ý	
CHỦ TRÌ KIẾN TRÚC	KTS. TRƯƠNG QUANG PHÙNG	
THIẾT KẾ	KTS. NGUYỄN KHOA TRƯỜNG	
QUẢN LÝ KỸ THUẬT	KTS. TRƯƠNG QUANG PHÙNG	


CÔNG TRÌNH : NHÀ HÀNG VÀ COFFEE

ĐỊA CHỈ : 254 VÕ NGUYÊN GIÁP - TP ĐÀ NẴNG

TEÂN BAÛN VEÕ :

MẶT ĐỨNG A'-H

TYÛ LEÄ	NGAØY THAØNH	BAÛN VEÕ
1/100	2024	KT-06

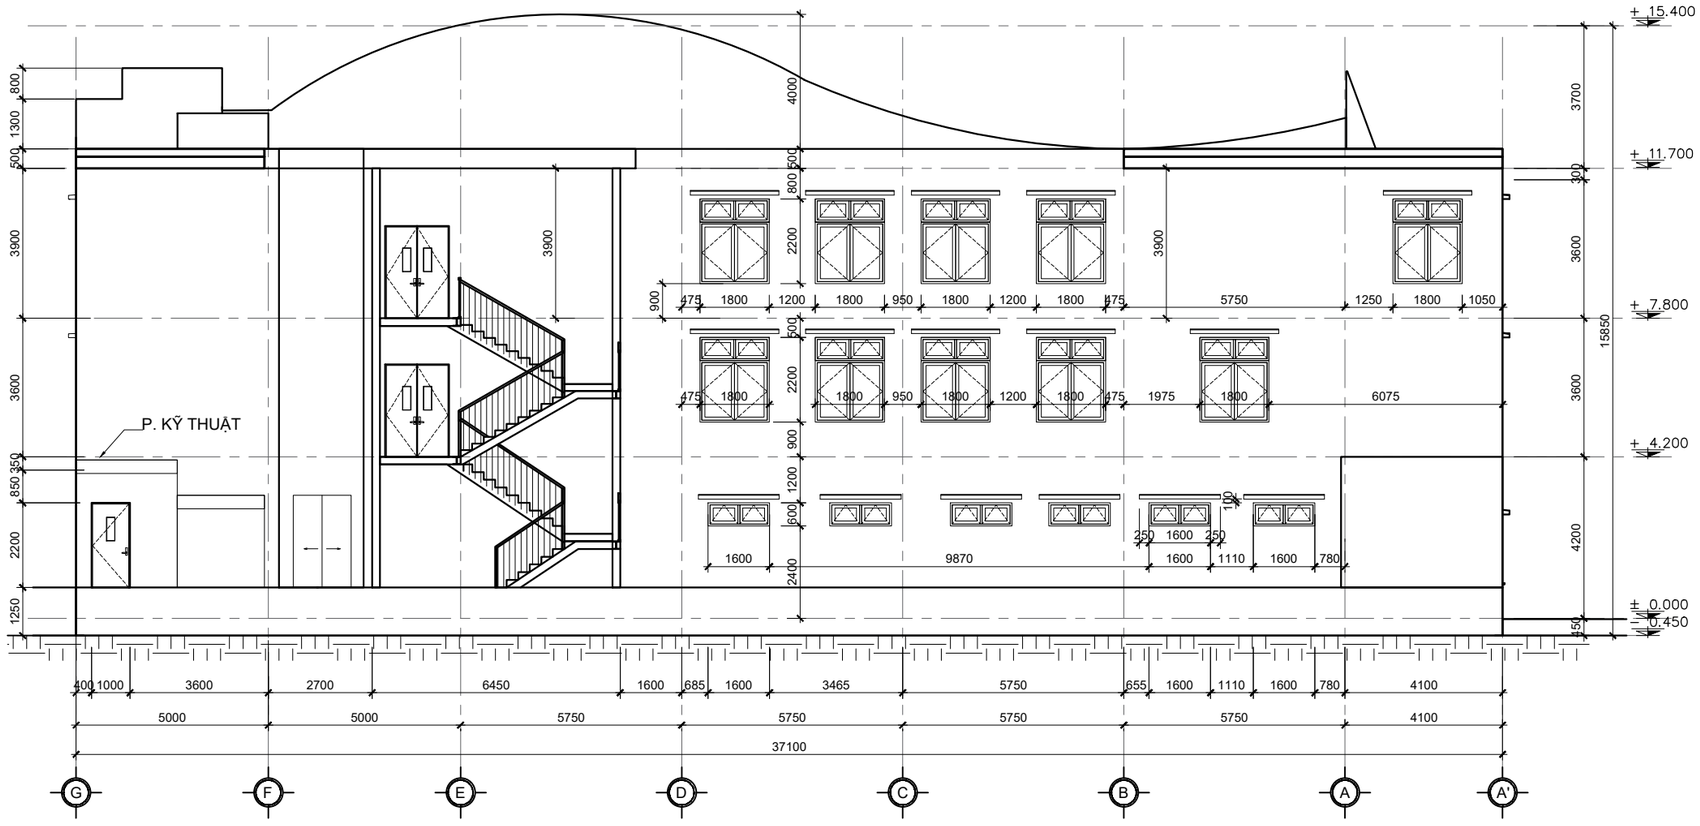

MẶT ĐỨNG H-A'

GHI CHÚ:

– TRƯỚC KHI THI CÔNG TẤT CẢ CÁC KÍCH THƯỚC ĐỀU PHẢI ĐƯỢC KIỂM TRA THỰC TẾ TẠI CÔNG TRƯỜNG. KHÔNG SỬ DỤNG THƯỚC ĐỂ ĐO KÍCH THƯỚC TRỰC TIẾP TRÊN BẢN VẼ.
– BẢN VẼ NÀY PHẢI ĐƯỢC KẾT HỢP CÙNG VỚI CÁC BẢN VẼ KHÁC CÓ LIÊN QUAN. TRONG TRƯỜNG HỢP CÓ SỰ MÂU THUẪN GIỮA CÁC BẢN VẼ THÌ ĐƠN VỊ THI CÔNG PHẢI THÔNG BÁO CHO ĐƠN VỊ QUẢN LÝ XÂY DỰNG VÀ ĐƠN VỊ THIẾT KẾ BẰNG VĂN BẢN.
– CAO ĐỘ TRONG BẢN VẼ LÀ CAO ĐỘ HOÀN THIỆN.

CHỦ ĐẦU TƯ:

CT TNHH MTV NGỌC QUANG ĐĂNG

TP. ĐÀ NẴNG

CÔNG TY TNHH THIẾT KẾ VÀ XÂY DỰNG
LONG HOUSE
Add: 348 Nguyễn Hữu Thọ - Q.Hải Châu - TP. Đà Nẵng
Tel: 0905.768.505
Mst: 0402159230
Email: longhouseart@gmail.com

GIÁM ĐỐC	NGUYỄN THÀNH Ý	
CHỦ TRÌ KIẾN TRÚC	KTS. TRƯƠNG QUANG PHÙNG	
THIẾT KẾ	KTS. NGUYỄN KHOA TRƯỜNG	
QUẢN LÝ KỸ THUẬT	KTS. TRƯƠNG QUANG PHÙNG	


CÔNG TRÌNH : NHÀ HÀNG VÀ COFFEE

ĐỊA CHỈ : 254 VÕ NGUYÊN GIÁP - TP ĐÀ NẴNG

TEÂN BAÛN VEÕ :

MẶT ĐỨNG H-A'

TYÛ LEÄ 1/100	NGAØY THAØNH 2024	BAÛN VEÕ

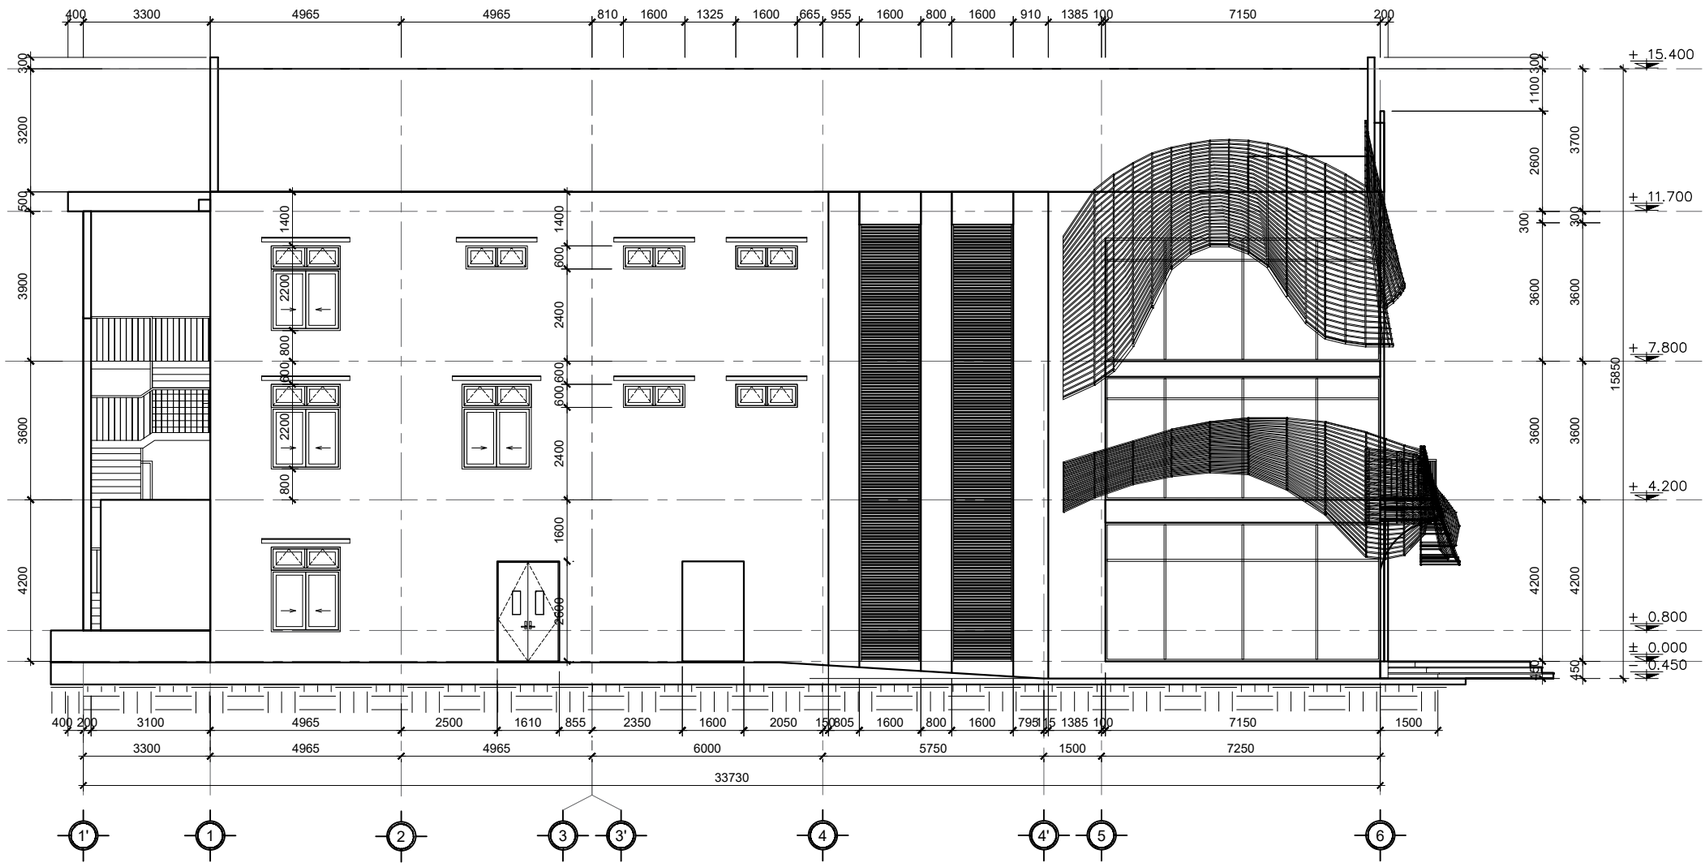

MẶT ĐỨNG 1-6

GHI CHÚ:

– TRƯỚC KHI THI CÔNG TẤT CẢ CÁC KÍCH THƯỚC ĐỀU PHẢI ĐƯỢC KIỂM TRA THỰC TẾ TẠI CÔNG TRƯỜNG. KHÔNG SỬ DỤNG THƯỚC ĐỂ ĐO KÍCH THƯỚC TRỰC TIẾP TRÊN BẢN VẼ.
– BẢN VẼ NÀY PHẢI ĐƯỢC KẾT HỢP CÙNG VỚI CÁC BẢN VẼ KHÁC CÓ LIÊN QUAN. TRONG TRƯỜNG HỢP CÓ SỰ MÂU THUẪN GIỮA CÁC BẢN VẼ THÌ ĐƠN VỊ THI CÔNG PHẢI THÔNG BÁO CHO ĐƠN VỊ QUẢN LÝ XÂY DỰNG VÀ ĐƠN VỊ THIẾT KẾ BẰNG VĂN BẢN.
– CAO ĐỘ TRONG BẢN VẼ LÀ CAO ĐỘ HOÀN THIỆN.

CHỦ ĐẦU TƯ:

CT TNHH MTV NGỌC QUANG ĐĂNG

TP. ĐÀ NẴNG

CÔNG TY TNHH THIẾT KẾ VÀ XÂY DỰNG
LONG HOUSE
Add: 348 Nguyễn Hữu Thọ - Q.Hải Châu - TP. Đà Nẵng
Tel: 0905.768.505
Mst: 0402159230
Email: longhouseart@gmail.com

GIÁM ĐỐC	NGUYỄN THÀNH Ý	
CHỦ TRÌ KIẾN TRÚC	KTS. TRƯƠNG QUANG PHÙNG	
THIẾT KẾ	KTS. NGUYỄN KHOA TRƯỜNG	
QUẢN LÝ KỸ THUẬT	KTS. TRƯƠNG QUANG PHÙNG	


CÔNG TRÌNH : NHÀ HÀNG VÀ COFFEE

ĐỊA CHỈ : 254 VÕ NGUYÊN GIÁP - TP ĐÀ NẴNG

TEÂN BAÛN VEÕ :

MẶT ĐỨNG 1-6

TYÛ LEÄ 1/100 NGAØY THAØNH 2024 BAÛN VEÕ

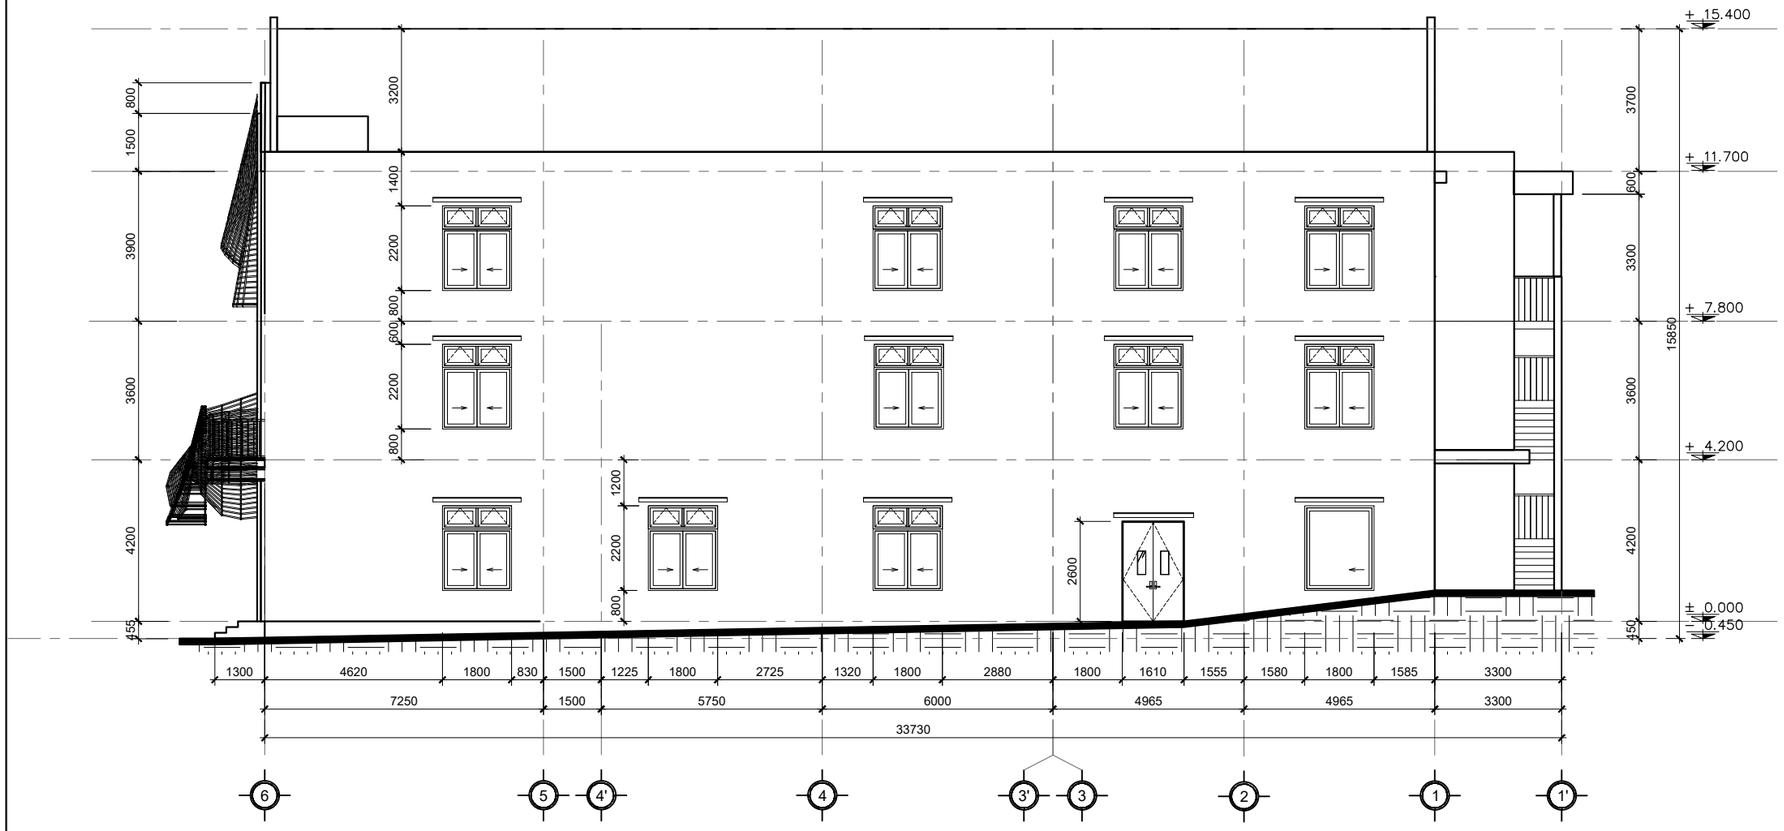

MẶT ĐỨNG 6-1

GHI CHÚ:

– TRƯỚC KHI THI CÔNG TẤT CẢ CÁC KÍCH THƯỚC ĐỀU PHẢI ĐƯỢC KIỂM TRA THỰC TẾ TẠI CÔNG TRƯỜNG. KHÔNG SỬ DỤNG THƯỚC ĐỂ ĐO KÍCH THƯỚC TRỰC TIẾP TRÊN BẢN VẼ.
– BẢN VẼ NÀY PHẢI ĐƯỢC KẾT HỢP CÙNG VỚI CÁC BẢN VẼ KHÁC CÓ LIÊN QUAN. TRONG TRƯỜNG HỢP CÓ SỰ MÂU THUẪN GIỮA CÁC BẢN VẼ THÌ ĐƠN VỊ THI CÔNG PHẢI THÔNG BÁO CHO ĐƠN VỊ QUẢN LÝ XÂY DỰNG VÀ ĐƠN VỊ THIẾT KẾ BẰNG VĂN BẢN.
– CAO ĐỘ TRONG BẢN VẼ LÀ CAO ĐỘ HOÀN THIỆN.

CHUÛ ÑAÀU TÖ :

CT TNHH MTV NGỌC QUANG ĐĂNG

TP. ĐÀ NẴNG

CÔNG TY TNHH THIẾT KẾ VÀ XÂY DỰNG
LONG HOUSE
Add: 348 Nguyễn Hữu Thọ - Q.Hải Châu - TP. Đà Nẵng
Tel: 0905.768.505
Mst: 0402159230
Email: longhouseart@gmail.com

GIÁM ĐỐC	NGUYỄN THÀNH Ý	
CHỦ TRÌ KIẾN TRÚC	KTS. TRƯƠNG QUANG PHÙNG	
THIẾT KẾ	KTS. NGUYỄN KHOA TRƯỜNG	
QUẢN LÝ KỸ THUẬT	KTS. TRƯƠNG QUANG PHÙNG	


CÔNG TRÌNH : NHÀ HÀNG VÀ COFFEE

ĐỊA CHỈ : 254 VÕ NGUYÊN GIÁP - TP ĐÀ NẴNG

TEÂN BAÛN VEÕ :

MẶT ĐỨNG 6-1

TYÛ LEÄ 1/100	NGAØY THAØNH 2024	BAÛN VEÕ

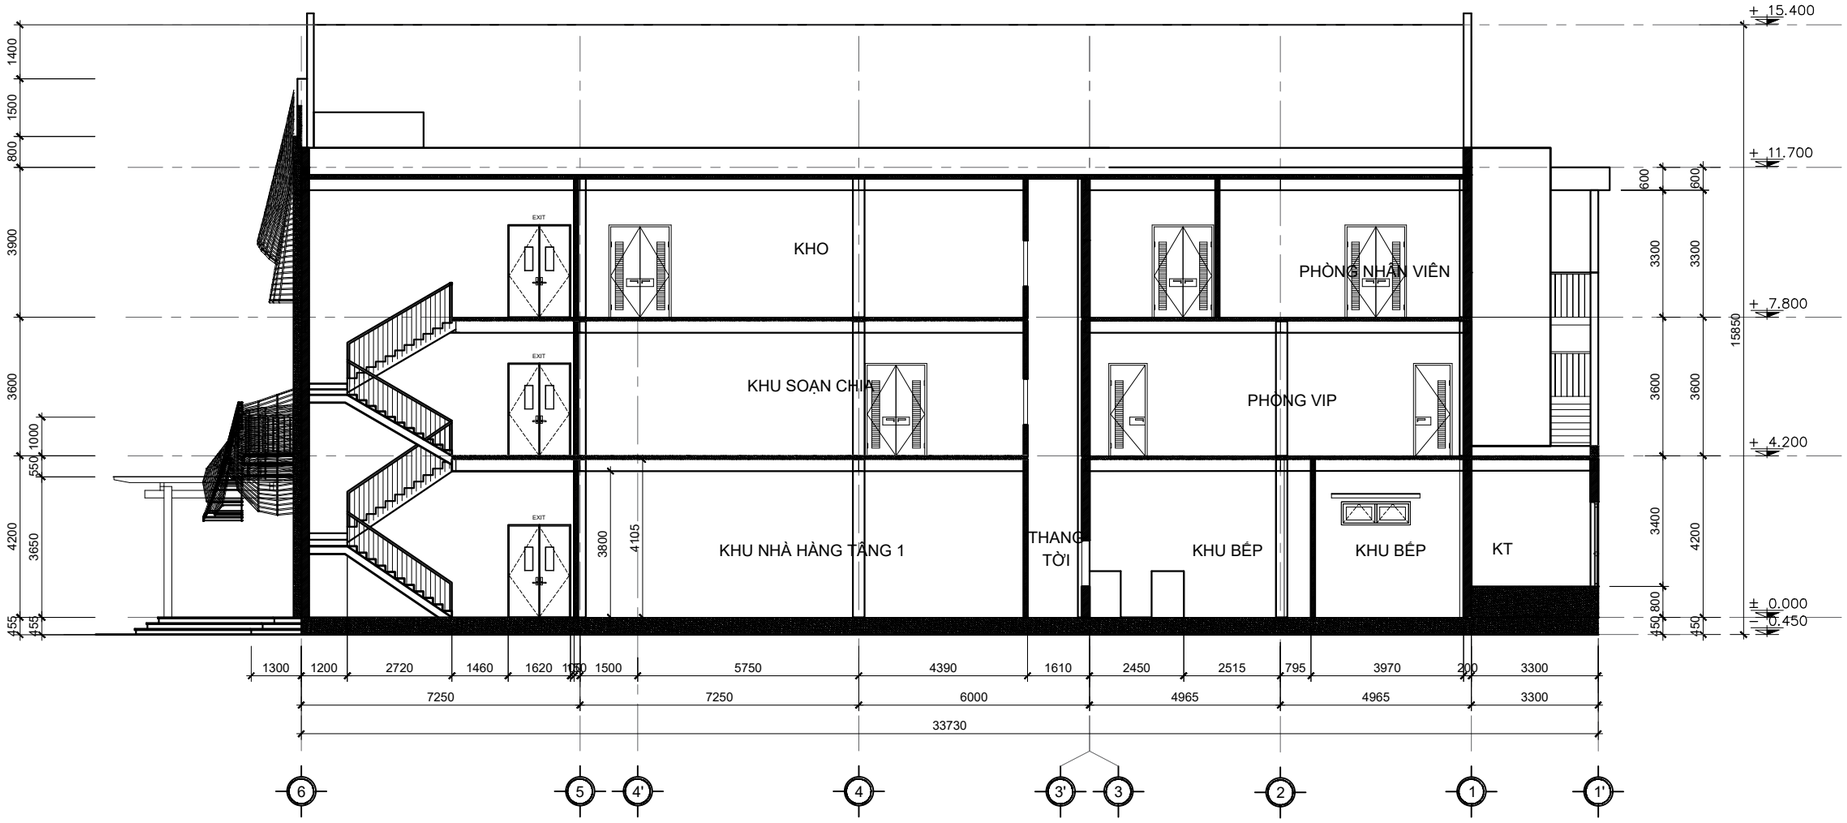

MẶT CẮT 1-1

GHI CHÚ:

– TRƯỚC KHI THI CÔNG TẤT CẢ CÁC KÍCH THƯỚC ĐỀU PHẢI ĐƯỢC KIỂM TRA THỰC TẾ TẠI CÔNG TRƯỜNG. KHÔNG SỬ DỤNG THƯỚC ĐỂ ĐO KÍCH THƯỚC TRỰC TIẾP TRÊN BẢN VẼ.
– BẢN VẼ NÀY PHẢI ĐƯỢC KẾT HỢP CÙNG VỚI CÁC BẢN VẼ KHÁC CÓ LIÊN QUAN. TRONG TRƯỜNG HỢP CÓ SỰ MÂU THUẪN GIỮA CÁC BẢN VẼ THÌ ĐƠN VỊ THI CÔNG PHẢI THÔNG BÁO CHO ĐƠN VỊ QUẢN LÝ XÂY DỰNG VÀ ĐƠN VỊ THIẾT KẾ BẰNG VĂN BẢN.
– CAO ĐỘ TRONG BẢN VẼ LÀ CAO ĐỘ HOÀN THIỆN.

CHỦ ĐẦU TƯ:

CT TNHH MTV NGỌC QUANG ĐĂNG

TP. ĐÀ NẴNG

CÔNG TY TNHH THIẾT KẾ VÀ XÂY DỰNG
LONG HOUSE
Add: 348 Nguyễn Hữu Thọ - Q.Hải Châu - TP. Đà Nẵng
Tel: 0905.768.505
Mst: 0402159230
Email: longhouseart@gmail.com

GIÁM ĐỐC	NGUYỄN THÀNH Ý	
CHỦ TRÌ KIẾN TRÚC	KTS. TRƯƠNG QUANG PHÙNG	
THIẾT KẾ	KTS. NGUYỄN KHOA TRƯỜNG	
QUẢN LÝ KỸ THUẬT	KTS. TRƯƠNG QUANG PHÙNG	

CÔNG TRÌNH : NHÀ HÀNG VÀ COFFEE

ĐỊA CHỈ : 254 VÕ NGUYÊN GIÁP - TP ĐÀ NẴNG

TEÂN BAÛN VEÕ :

MẶT CẮT 1 - 1

TYÛ LEÄ	1/100	BAÛN VEÕ