# SAMARKAND

R12

## Covered terrace · Layout R12 · rev. 8

2026-11-04

Tajik & Uzbek national cuisine · 254 Võ Nguyên Giáp, Đà Nẵng

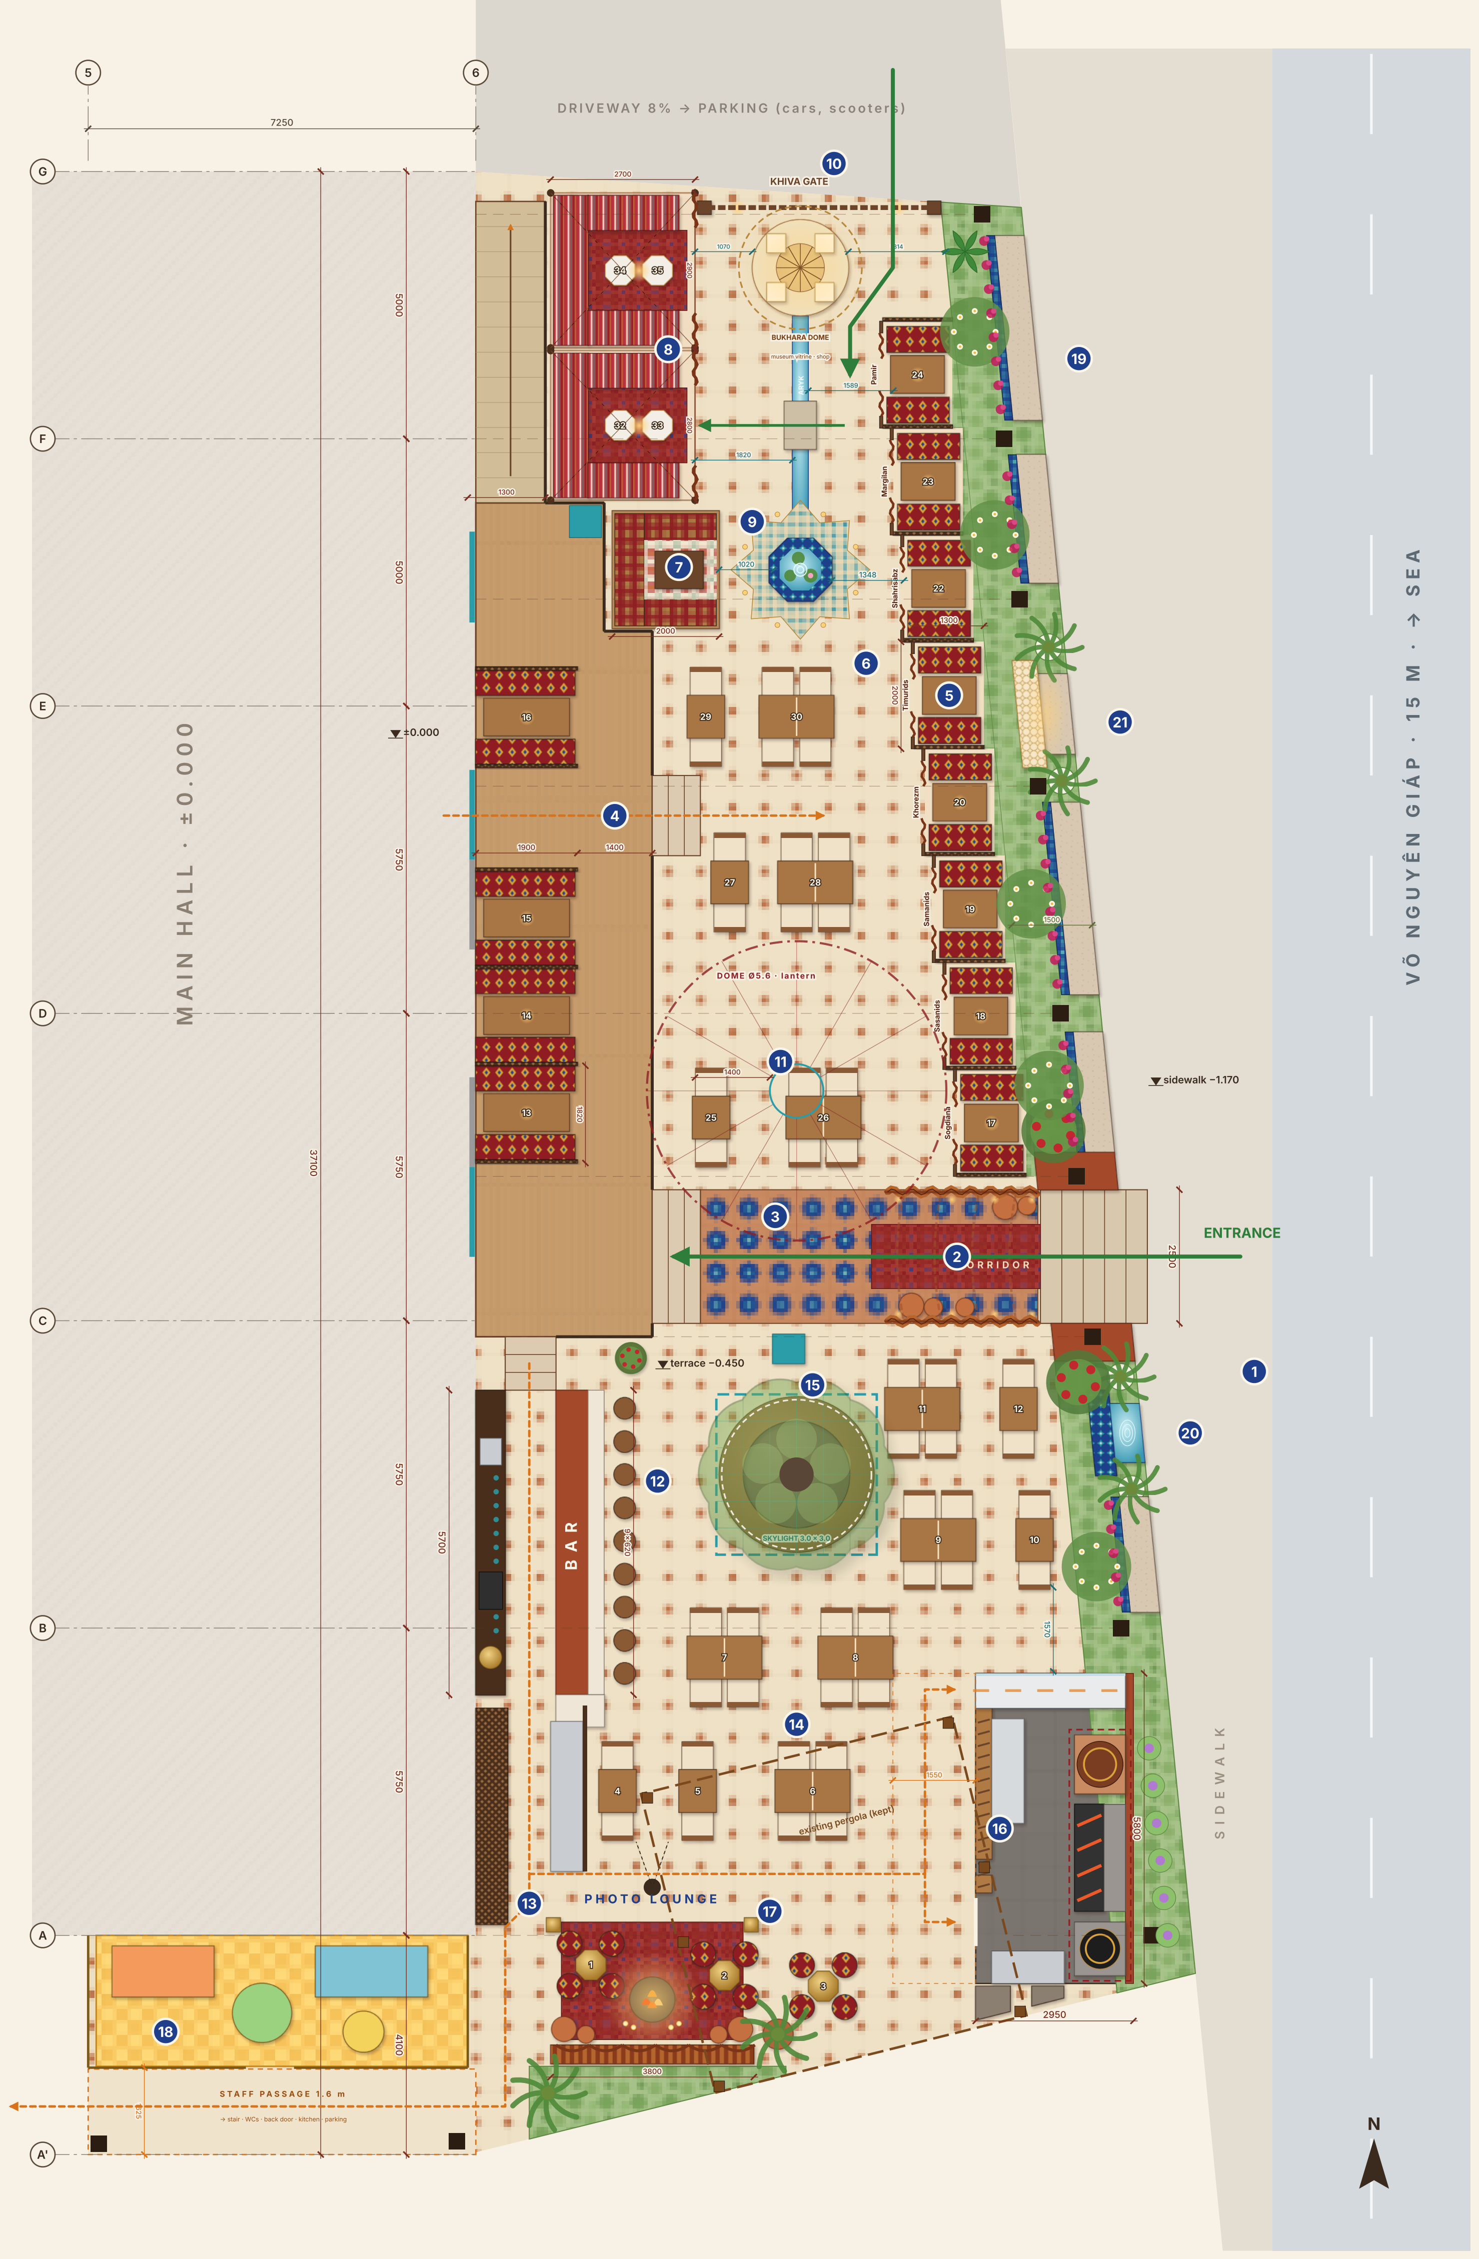

Scale 1:100 · A2

0 5 m

## ZONES

1. **Street entrance · pishtaq portal**
   2.5 m opening, 4 steps from the sidewalk
2. **Draped corridor**
   crossed velvet swags, layered rugs, terracotta jars, pillar candles
3. **Alley to the hall**
   girih paving, 2.5 m, host at the exit
4. **Aivan platform ±0.000**
   4 sedir booths for 6, carved screens, 65" display to the alley
5. **Themed booths**
   8 closed rooms: epochs and cities, curtained portals
6. **Tables by the fountain**
   a 4-top + a 2-top, where the north chinar stood
7. **Tapchan 2.0 × 2.2 m**
   6 guests, balustrade, kurpacha, turned-leg table
8. **Two majlis tents 2.6 × 2.75 m**
   8 guests each, floor majlis seating, octagonal tables
9. **Hauz fountain and aryk**
   hauz Ø1.2 m, 0.3 m aryk leads from the north entrance
10. **North entrance · "Khiva gate"**
    4.1 m gate, Bukhara dome — vitrine and shop, ramp 1:12
11. **Dining north**
    rows of a 4-top + a 2-top, the space under the dome kept open
12. **Bar**
    tea, samovar, coffee · 9 stools
13. **Staff station**
    shelving, POS, water, ice, dishes
14. **Dining south**
    row 4 + 2 + 4 and row 4 + 4
15. **Chinar under the lantern + entrance tables**
    tree under the roof, 3 × 3 m skylight; 4 tables by the mangal
16. **Mangal kitchen 3.3 × 5.8 m**
    tandoor · mangal · kazan · pass · SAMARKAND sign
17. **Photo lounge "Ochag"**
    drapes, carpets, fire bowl, 3 low tables, 12 poufs
18. **Kids zone**
    against the hall glazing — seen from inside; soft floor
19. **Street benches**
    cast concrete in the planter wall, majolica
20. **Sebil fountain**
    majolica wall, brass spout, basin
21. **Street photo arch**
    bench niche, uplight, palms

## SEATS

| | |
|---|---|
| Entrance tables | 12 |
| Chinar bench south | 10 |
| Dining south | 16 |
| Photo lounge (poufs) | 12 |
| Bar counter | 9 |
| Aivan: sedir booths (4 × 6) | 24 |
| Dining north + tables by the hauz | 18 |
| Themed booths | 32 |
| Tapchan | 6 |
| Majlis tents (2 × 8) | 16 |
| **Total restaurant seats** | **155** |
| + street benches (not counted) | ~31 |

Tables: 7 two-tops, 8 four-tops (all split into 2-top modules; no six-tops), 4 booths for 6

## ERGONOMICS · standard / as planned

| | | |
|---|---|---|
| Main path / alley | ≥1500 | **2500** |
| Path to the booths | ≥1200 | **1348** |
| Path tapchan ↔ fountain | ≥900 | **932** |
| Aivan aisle | ≥1200 | **1400** |
| Table module: per guest / depth | 600–700 / 750–800 | **700 / 800** |
| Table edge → armchair back | 450–600 | **525** |
| Chair back to back (no path) | ≥450 | **600** |
| Armchair 580: gap between arms | ≥100 | **120** |
| Bar counter: height / overhang | 1050 / 250–300 | **1050 / 300** |
| Bar stool pitch | 600–650 | **620** |
| Cook work aisle | ≥1200 | **2450** |
| Pass → guests | ≥1500 | **1570** |
| Ramp: slope / width | 1:12 / ≥1200 | **1:12 / 1300** |
| Tapchan: height / per guest | 400–450 / ≥600 | **450 / 700** |
| Staff passage (clear at the columns) | ≥1200 | **1275** |
| Seat / table / armrest | 450–500 / 740–760 | **500 / 760 / 660** |

## KEY

| | | | |
|---|---|---|---|
| ■ | Roof column (steel, wood-clad) | – – | Roof beam |
| –·– | Building axis | ➔ | Guest entrance |
| - - - | Staff route | ▬ | Hall door, open |
| ▬ | Hall door, closed | – – | Exhaust hood |
| ⟋—⟋ | Dimension, mm | 12 | Table no. |
| ⬚ | Skylight over the chinar | ▮ | Table module joint |

- Base: as-built DWG (Long House, 10-07-2024) 1:1. Levels: sidewalk −1.170, terrace −0.450, aivan and hall ±0.000.
- Roof: steel beams on the grid, Klip-Lok standing-seam sheet + insulation, 3.5% fall to the street, one sheet length (no end laps), gutter along the street; balcony soffit +3.850. The existing pergola at the south wall is kept: the new roof runs over it on short purlins bolted to its beams.
- One roof dome — the central Ø5.6 karbandi dome with a glazed lantern. The chinar by the bar stays under the roof: crown trained at 2.2–3.0 m, a 3.0 × 3.0 m skylight with a carved panjara grille above it. The north chinar is removed.
- Every loose table is a 700 × 800 module: pairs split into 2-tops or push together into tables for 6–8 (rows are aligned).
- Doors: C–D south open; C–D north and D–E south closed (banquette); D–E north and E–F by the lift open.

## PLANTING

- **Pomegranate (anor), symbol of Samarkand**
  at the entrance and in a pot by the bar
- **Plumeria (frangipani)**
  street planter, evening scent
- **Bougainvillea and jasmine sambac**
  on the street bench backs
- **Areca palm**
  pots in the photo lounge
- **Banana, Strelitzia nicolai**
  green frame of the Khiva gate
- **Reyhan, mint, basil**
  herb bed by the mangal, to the table
- **Lotus, water lily**
  in the hauz
- **Chinar by the bar (existing)**
  under the skylight, trained crown, uplit

## MANGAL KITCHEN · 1:100

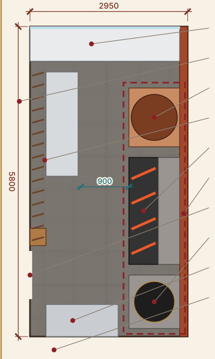
2950
5800
900
Pass 3.15 m, lamps, glass
Firewood show wall (to the room)
Copper tandoor Ø900 by the pass
Cold prep, under-counter fridges
Mangal 2.0 m, charcoal
Fire wall
Staff door 900
Kazan Ø800, gas
Hand wash · sink · waste
Charcoal, wood, crates

## MAJLIS TENT (×2) · 1:75

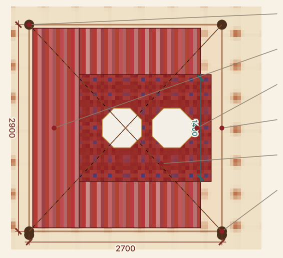

## AIVAN: SEDIR BOOTHS · 1:75

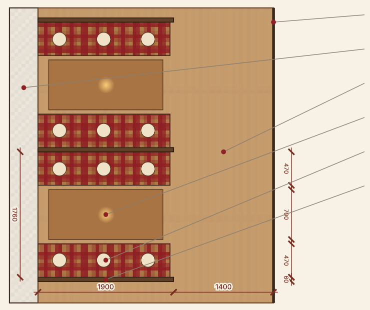

## TABLE MODULES · 1:100

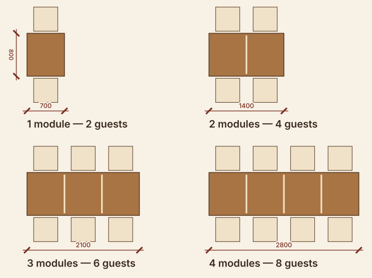

Top 700 × 800, h 760, zellige inlay; joined with hidden clamps

SAMARKAND · R12 · 2026-11-04

Concept for client review · dimensions to verify on site

*designed by Nomad Group*