SAMARKAND

NHÀ HÀNG ẨM THỰC TRUNG Á · CENTRAL ASIAN RESTAURANT

HỒ SƠ THIẾT KẾ THI CÔNG NỘI THẤT & KIẾN TRÚC CẢNH QUAN SÂN HIÊN · CONSTRUCTION DRAWING SET

Sân hiên 446 m² · 152 chỗ trong nhà · Đà Nẵng, Việt Nam

Phiên bản / Revision R12-v11.7 · Tháng 11 / 2026 · Khổ A3 — tỷ lệ in đúng khi in 100 % / print at 100 % on A3

Tài liệu dùng cho đội thi công: mọi kích thước bằng mm (cao độ bằng m), kiểm tra tại hiện trường trước khi gia công.

For the construction team: all dimensions in mm (levels in m) — verify on site before fabrication.

THÔNG TIN CHUNG & GHI CHÚ KỸ THUẬT

GENERAL INFORMATION, NOTES & DRAWING INDEX

THÔNG TIN DỰ ÁN / PROJECT DATA

Mục / Item	Thông số / Data
Dự án / Project	SAMARKAND — nhà hàng Trung Á
Địa điểm / Site	Sân hiên trệt, Đà Nẵng
Hạng mục / Scope	Nội thất, mái che, cảnh quan sân hiên
Diện tích / Area	446 m² (gồm sân hiên)
Chiều dài mặt tiền	37,1 m dọc phố
Sức chứa / Seats	152 trong nhà + ~30 ghế phố
Cao độ chuẩn / Datum	±0.000 = sàn hoàn thiện sân hiên
Aivan / Cabin	+0.450 / +0.150
Mái / Roof	Klip-Lok dốc 3,5 % ra phố
Đỉnh mái vòm / Dome	+5.94 (đỉnh alem +7.85)
Mô hình 3D / Model	R12-v11.7 (viewer + Blender)

GHI CHÚ CHUNG / GENERAL NOTES

1. Kích thước bằng mm, cao độ bằng m. Không đo trên bản vẽ — dùng số ghi.
   Dimensions in mm, levels in m. Do not scale — use written dimensions.
2. Nhà thầu kiểm tra hiện trạng (cột, dầm, sàn, cửa toà nhà) trước khi gia công.
   Verify existing building, slab and openings before fabrication.
3. Kết cấu thép (cột 150×150, dầm I300×150, xà gồ) — kỹ sư kết cấu
   duyệt tiết diện & liên kết trước khi thi công.
4. Gỗ: óc chó / gỗ tự nhiên sấy ≤12 %, xử lý chống mối mọt, sơn PU mờ.
   Walnut / kiln-dried hardwood ≤12 % MC, anti-termite, matt PU.
5. Gạch men / gạch ốp: keo dán C2TE, ron epoxy 2–3 mm.
   Glazed tiles & brick slips: C2TE adhesive, 2–3 mm epoxy grout.
6. Vải bọc & rèm: chống cháy (BS 5867 / tương đương), giặt được.
   Upholstery & curtains: flame-retardant, washable.
7. Điện: TCVN / IEC; ổ cắm sàn IP44, đèn ngoài trời IP65, RCBO 30 mA.
   Electrical to TCVN/IEC; floor boxes IP44, outdoor IP65.
8. PCCC: lối thoát ≥1,0 m, không cản trở bởi rèm / chậu cây.
   Escape routes ≥1.0 m clear of curtains & planters.
9. Mọi mẫu vật liệu được chủ đầu tư duyệt trước khi đặt hàng.
   All samples approved by the owner before ordering.

DANH MỤC BẢN VẼ / DRAWING INDEX

Số / No.	Tên bản vẽ / Title
KT-00	Bìa / Cover
KT-01	Thông tin chung, ghi chú, danh mục / General notes & index
KT-02	Mặt bằng phân khu & diện tích / Zoning & areas
KT-03	Mặt bằng bố trí nội thất & kích thước / Furniture & dimension plan
KT-04	Mặt bằng hoàn thiện sàn / Floor finishes plan
KT-05	Mặt bằng trần & chiếu sáng / Reflected ceiling & lighting
KT-06	Mặt bằng kết cấu mái / Roof framing plan
KT-07	Mặt đứng / Elevations
KT-08	Mặt cắt A-A, B-B, C-C / Sections
CT-01	Chi tiết cột Samarkand & cổng pishtaq / Column & pishtaq
CT-02	Chi tiết aivan / Aivan
CT-03	Chi tiết cabin VIP / Booths
CT-04	Chi tiết trần ô hộp / Ceiling coffers
CT-05	Chi tiết mái vòm / Dome
CT-06	Chi tiết quầy bar / Bar
CT-07	Chi tiết hành lang vòm / Arcade corridor
CT-08	Chi tiết diềm mái mặt tiền / Street eave
CT-09	Chi tiết khu mangal / Mangal
CT-10	Chi tiết sàn đá & gạch / Floor details
CT-11	Nội thất: ghế, sofa, bàn / Furniture
BV-01	Bảng vật liệu hoàn thiện / Finishes schedule
BV-02	Bảng chiếu sáng & điện / Lighting & power schedule
PC-01	Phối cảnh / Perspectives 1
PC-02	Phối cảnh / Perspectives 2

KÝ HIỆU / SYMBOLS

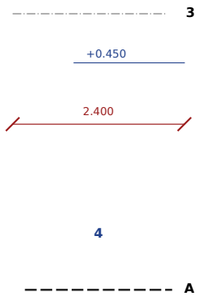

Trục định vị / Grid axis

Cao độ hoàn thiện / Finished level

Đường kích thước (mm) / Dimension

Phần bị cắt / Cut element (poché)

Số hiệu khu / Zone or item tag

Vị trí mặt cắt / Section mark

VIẾT TẮT / ABBREVIATIONS

FFL — cao độ sàn hoàn thiện / finished floor level

SHS — thép hộp vuông / square hollow section

MDF — ván sợi mật độ trung bình

LED 2700K — đèn ánh sáng vàng ấm

IP44 / IP65 — cấp bảo vệ thiết bị điện

CT — chi tiết / detail

TL — tỷ lệ / scale

VL — vật liệu / material

NGUYÊN TẮC THIẾT KẾ / DESIGN INTENT

«Con đường tơ lụa trên một bàn ăn» — gỗ chạm khắc, men lam, thảm dệt tay và ánh đồng ấm của Samarkand & Bukhara.

Mọi bề mặt hoa văn là VẬT LIỆU THẬT (gạch, gạch men, gỗ chạm), không dùng ảnh in / decal.

Every pattern is built from real material — brick, glazed tile, carved timber — never printed decals.

Ưu tiên công thái học: lối đi ≥ 930 mm, mép ghế — mép bàn 80–190 mm, chân bàn đặt giữa (bàn chân chữ T),

ghế sofa 700 mm / người trong cabin, chiều cao bàn 750 mm, ghế 450–500 mm.

Ergonomics: aisles ≥ 930, seat-to-table 80–190, centred trestle legs, 700 per sitter in booths.

Khí hậu biển Đà Nẵng: inox 316 cho phụ kiện ngoài trời, gỗ xử lý chống ẩm, vải ngoài trời giới hạn

(chỉ dài rèm buộc), mọi đèn ngoài trời IP65.

Coastal climate: SS316 outdoor fixings, sealed timber, minimal loose fabric, IP65 outdoors.

1 MẶT BẰNG PHÂN KHU
Zoning & circulation plan · TL / Scale 1:100

#	Khu / Zone	m²
1	Bar	24.0
2	Sảnh chính / Hall	107.8
3	Aivan	51.5
4	Cabin VIP	32.2
5	Lều & tapchan	26.2

#	Khu / Zone	m²
6	Majlis & pergola	46.0
7	Mangal	16.8
8	Hành lang vòm / Corridor	6.3
9	Khu trẻ em / Kids	26.4
10	Bukhara dome / lối ra	15.1

Tổng sân hiên / Terrace total ≈ 446 m²

1 MẶT BẰNG BỐ TRÍ NỘI THẤT

Furniture & dimension plan, cut at +1.20 · TL / Scale 1:100

CHÚ THÍCH KHU / ZONES

1 Quầy bar · 2 Sảnh ăn chính · 3 Mái vòm · 4 Cabin VIP · 5 Aivan +0.450
6 Lều / Tents · 7 Tapchan · 8 Majlis · 9 Khu trẻ em · 10 Mangal
11 Hành lang vòm · 12 Cổng Pishtaq · 13 Cây ô liu · 14 Ghế đường phố

Khu / Zone	Chỗ / Seats
Sảnh 19 bàn / Hall	58
Cabin 7 / Booths	28
Aivan 4 vịnh / bays	24
Bar / Lều / Majlis / Tapchan	10 / 16 / 10 / 6
TỔNG TRONG NHÀ / TOTAL INSIDE	152

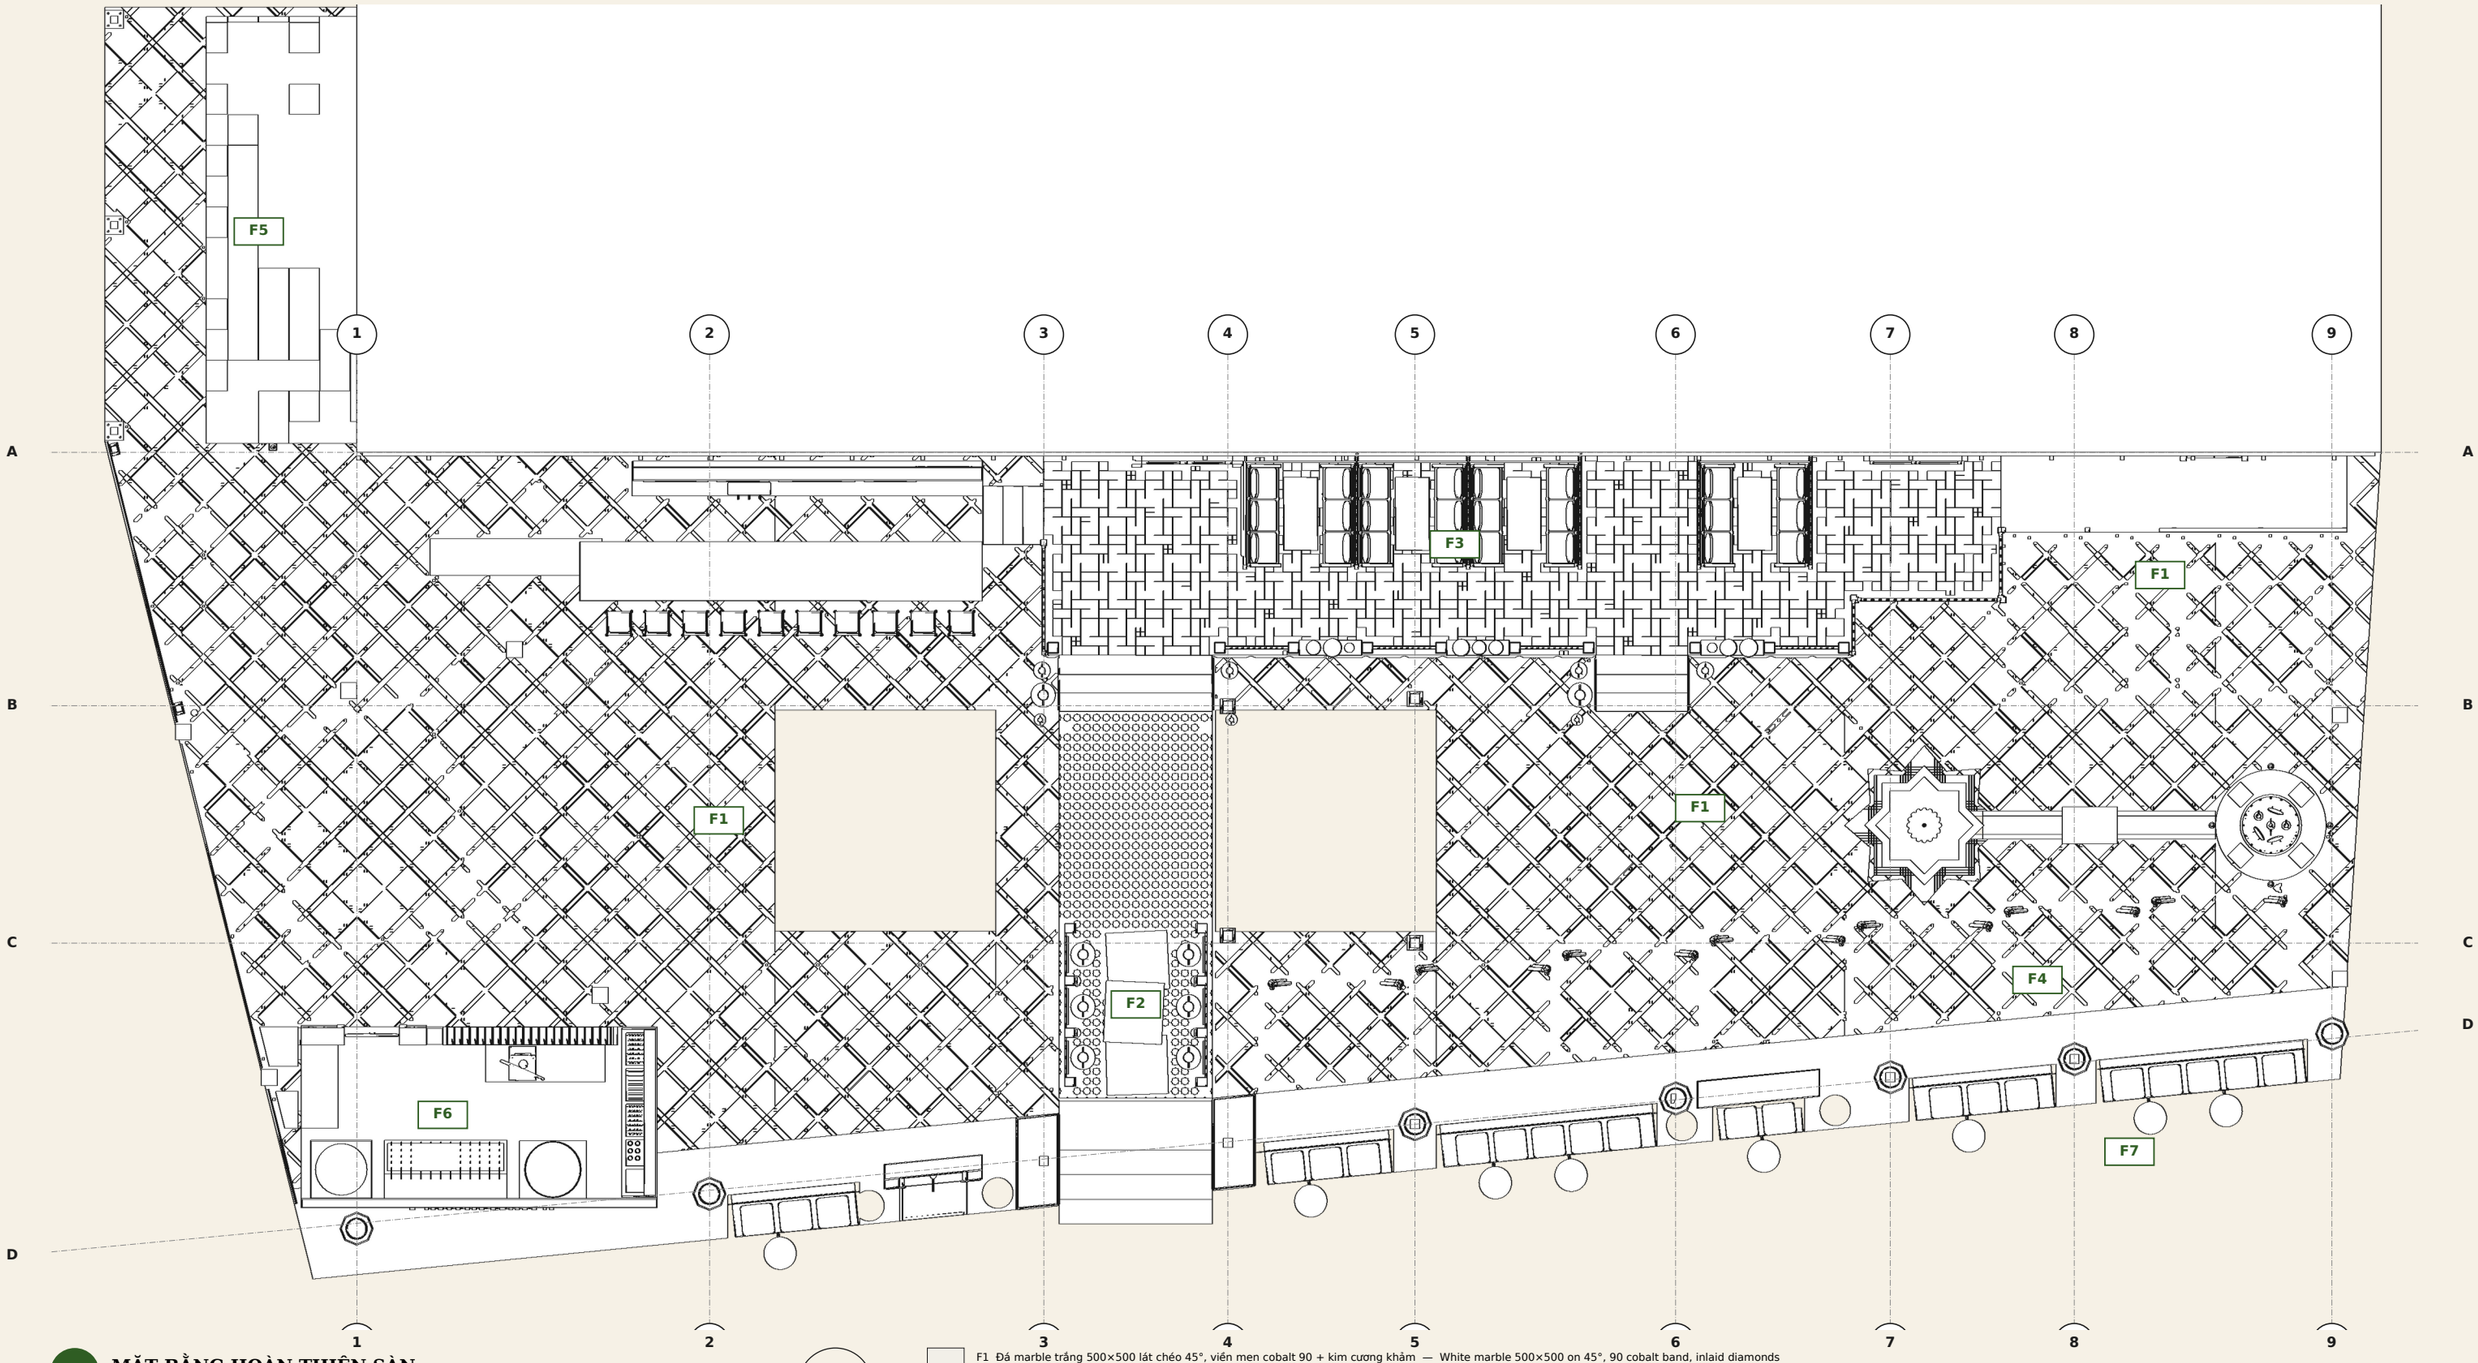

1 MẶT BẰNG HOÀN THIỆN SÀN
Floor finishes plan · TL / Scale 1:100

B / N

- F1 Đá marble trắng 500×500 lát chéo 45°, viền men cobalt 90 + kim cương khảm — White marble 500×500 on 45°, 90 cobalt band, inlaid diamonds
- F2 Gạch zellige sao 8 cánh (lối hành lang) 160 / 200 module — Zellige 8-point star runner (corridor path)
- F3 Gạch nung 300×150 xếp «chong chóng» + gạch men 150 — Terracotta 300×150 pinwheel + 150 glazed inserts (aivan)
- F4 Bục cabin: gỗ óc chó + thảm Ba Tư — Booth podium: walnut riser + Persian rug
- F5 Sàn cao su EPDM 500×500 (khu trẻ em) — EPDM rubber tiles 500×500 (kids)
- F6 Đá slate chống trơn (khu mangal) — Anti-slip slate (mangal)
- F7 Gạch terracotta & zellige (sân phố, hauz) — Terracotta & zellige (street court, hauz)

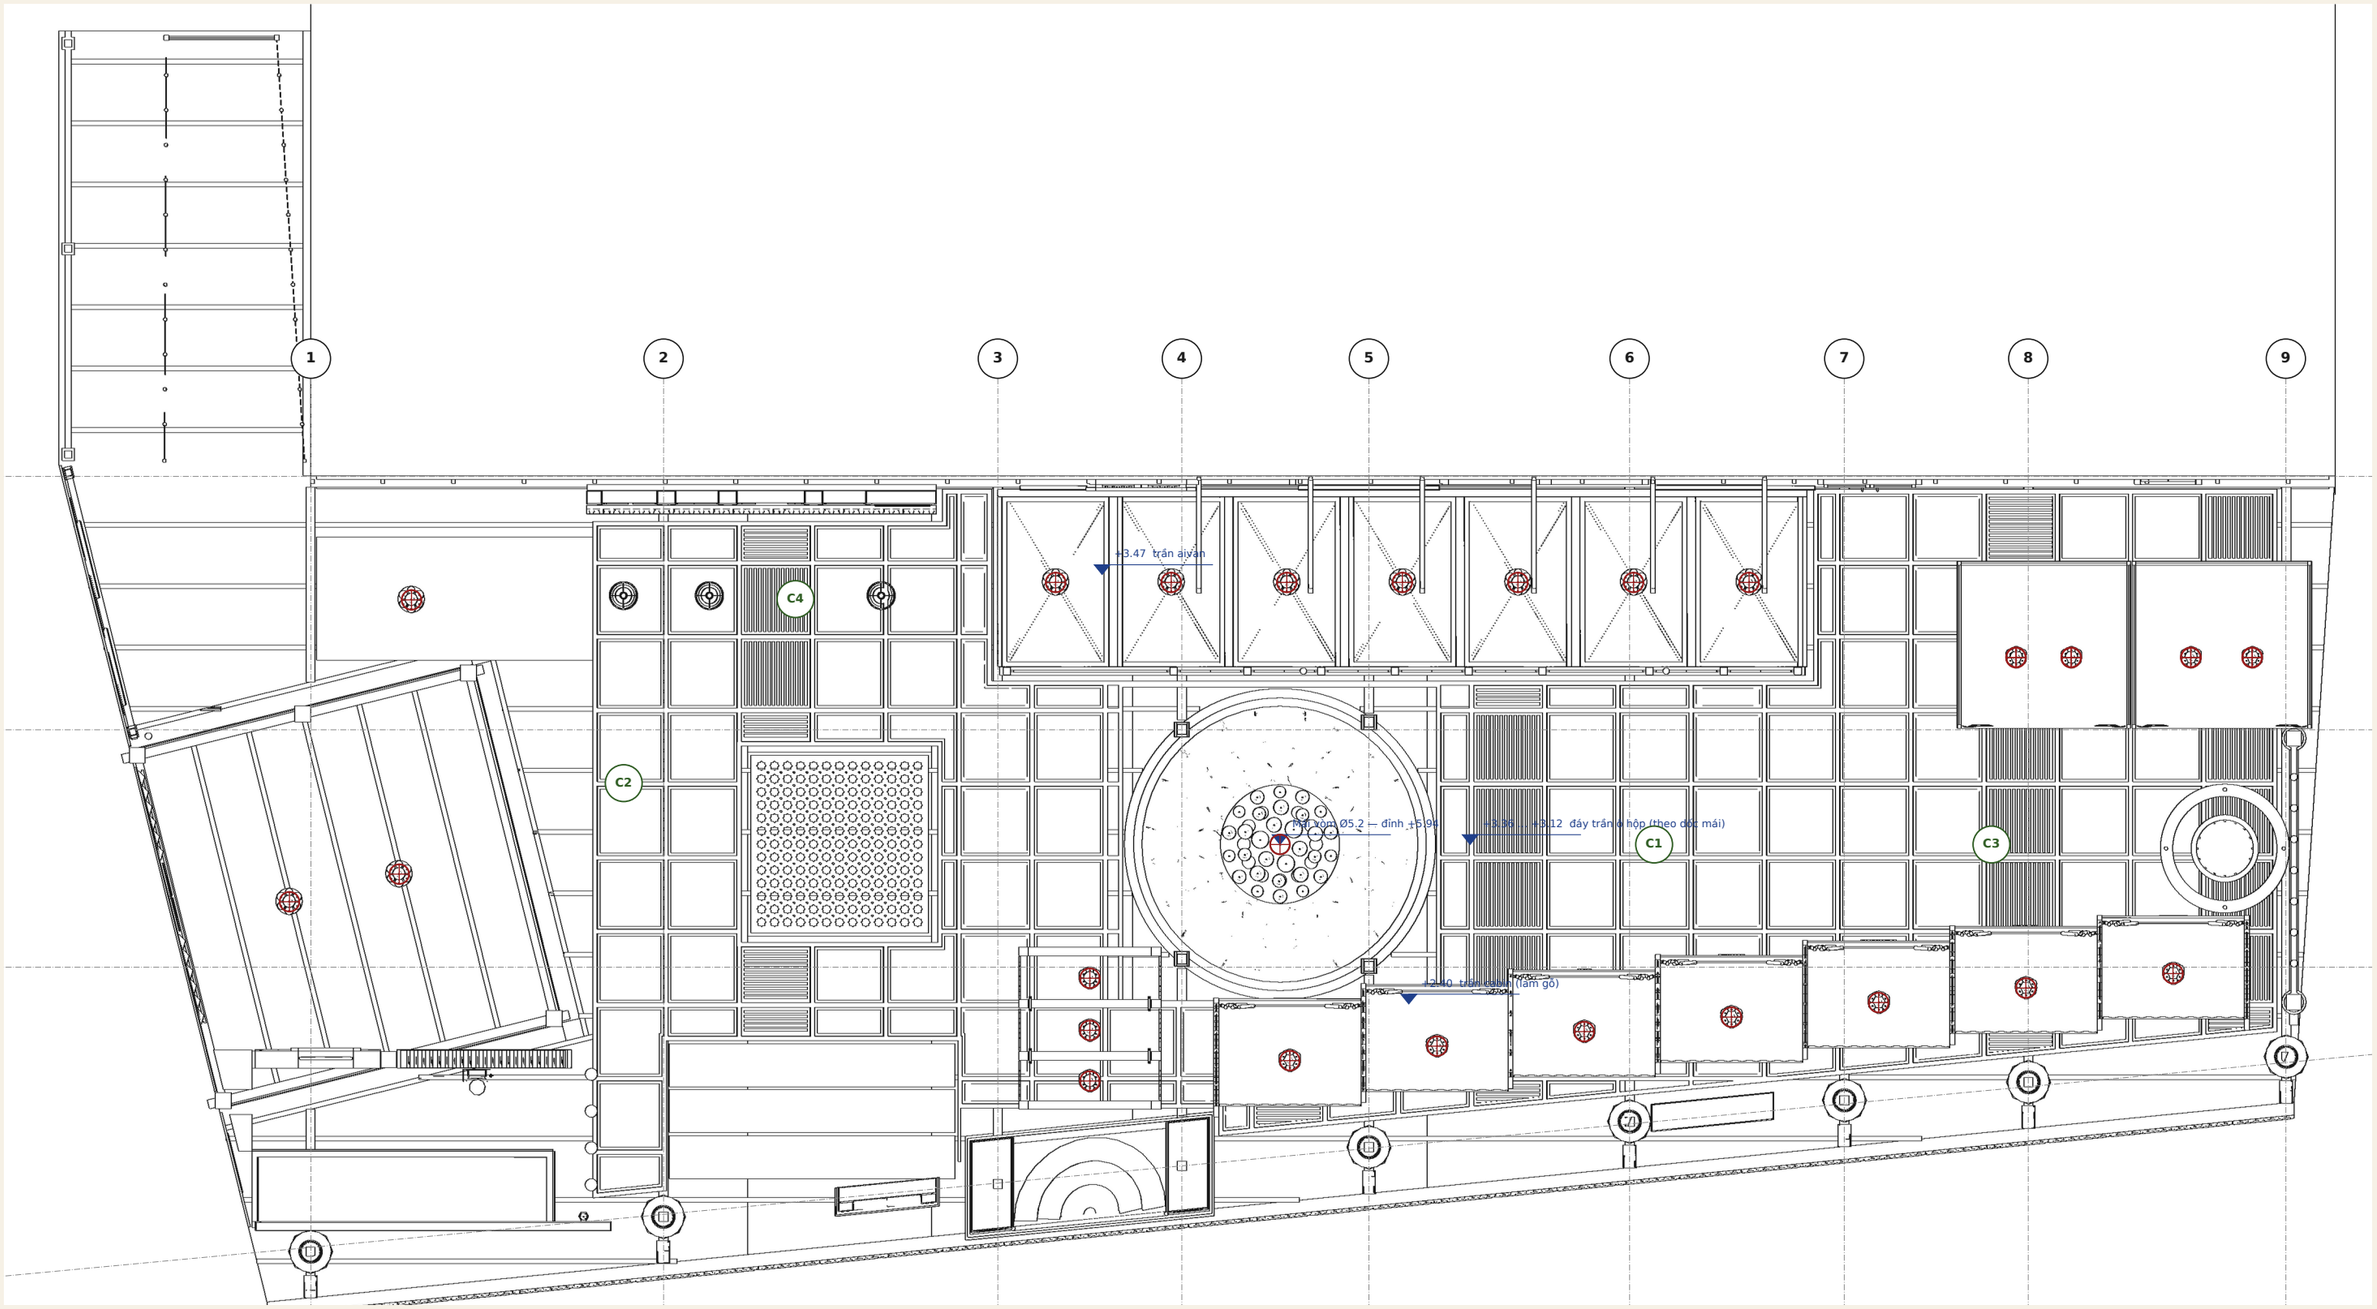

1 MẶT BẰNG TRẦN (NHÌN XUỐNG)
Reflected ceiling plan (looking down) · TL / Scale 1:100

Mã	Mô tả / Description (VI)	EN
C1	Ô hộp gỗ 1,2 × 1,2 m, thảm Ba Tư, LED hắt 2700K	Walnut coffer + carpet + hidden LED
C2	Hộp nan gỗ hạ 150, LED phía sau	Dropped timber slat box, back-lit
C3	Ô thảm + sườn chéo gỗ	Carpet coffer with diagonal ribs
C4	Ô sâu (khung hạ 100) + sườn chéo	Deep coffer + ribs
⊕	Đèn chùm kiểu mái vòm (cầu đồng đục lỗ)	Dome-style cascade chandelier

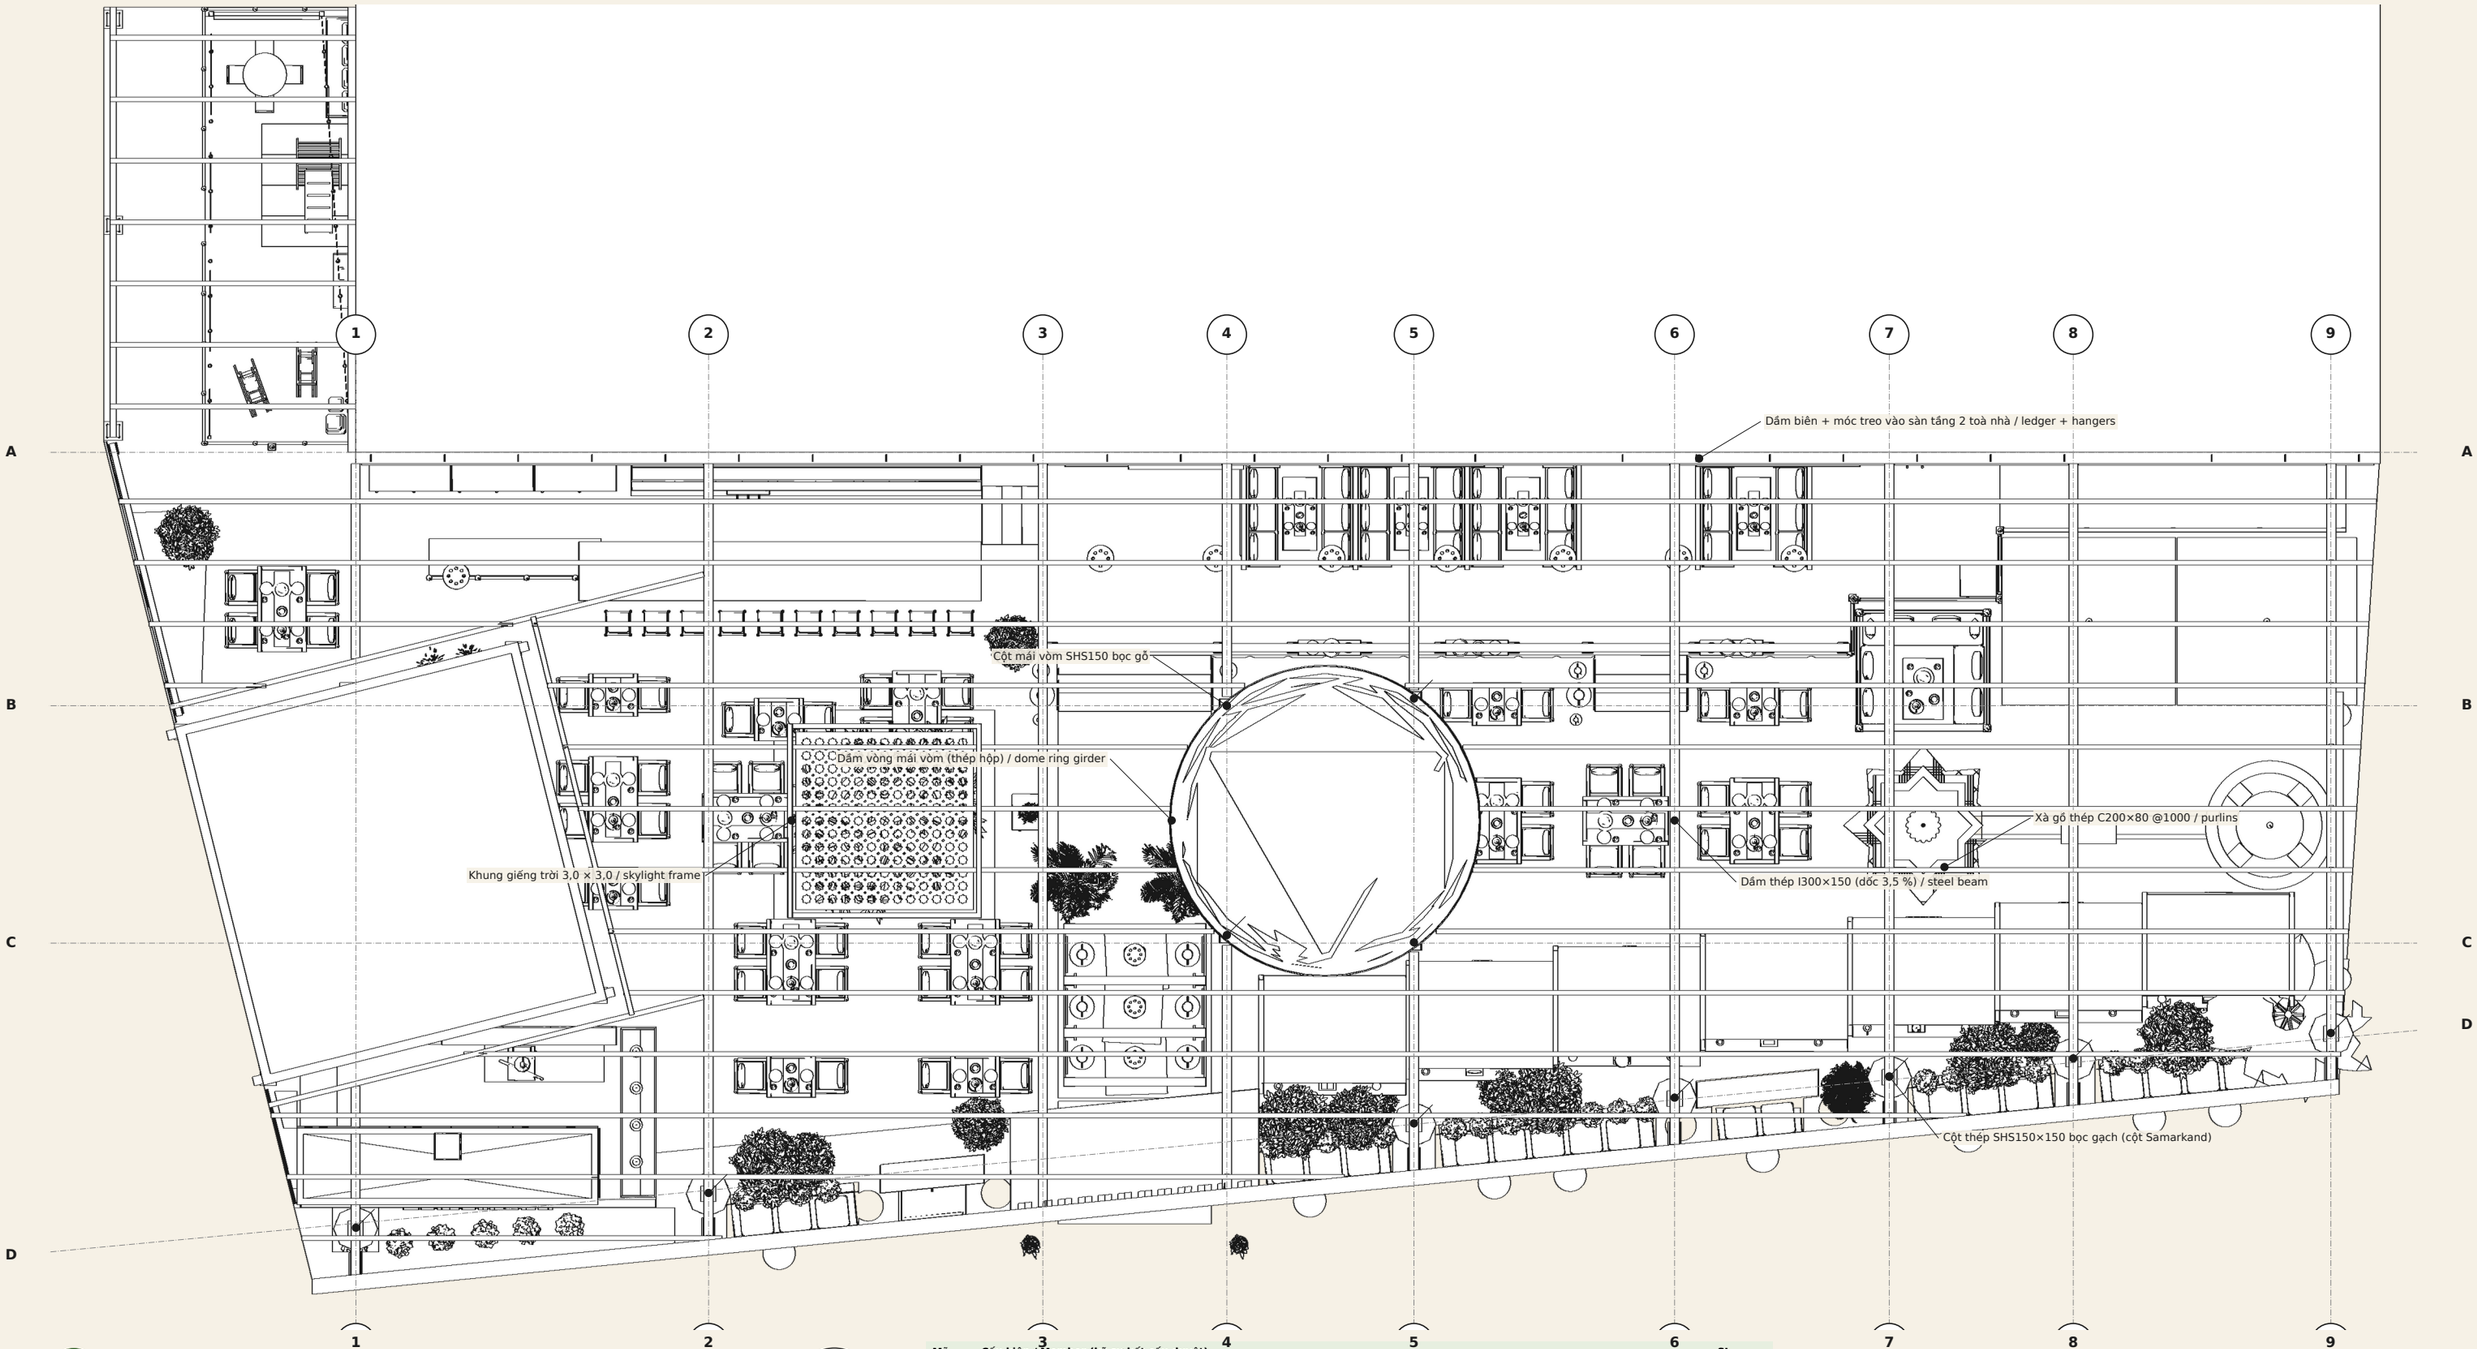

1 MẶT BẰNG KẾT CẤU MÁI
Roof framing plan (roof sheeting removed) · TL / Scale 1:100

B / N

Mã	Cấu kiện / Member (kỹ sư kết cấu duyệt)	SL
K1	Cột thép SHS 150×150×6, đế 300×300×16, 4 bu lông M16	7+4
K2	Dầm I300×150×6.5×9, liên kết bản mã 10	12
K3	Xà gồ C200×80×2.5 @1000	20
K4	Dầm vòng mái vòm SHS 200×100, 4 cột đỡ	1
K5	Tôn Klip-Lok 0.48, dốc 3,5 %, máng xối phố	—
K6	Dầm biên + móc treo M12 vào sàn L2 (khoan cấy hoá chất)	28

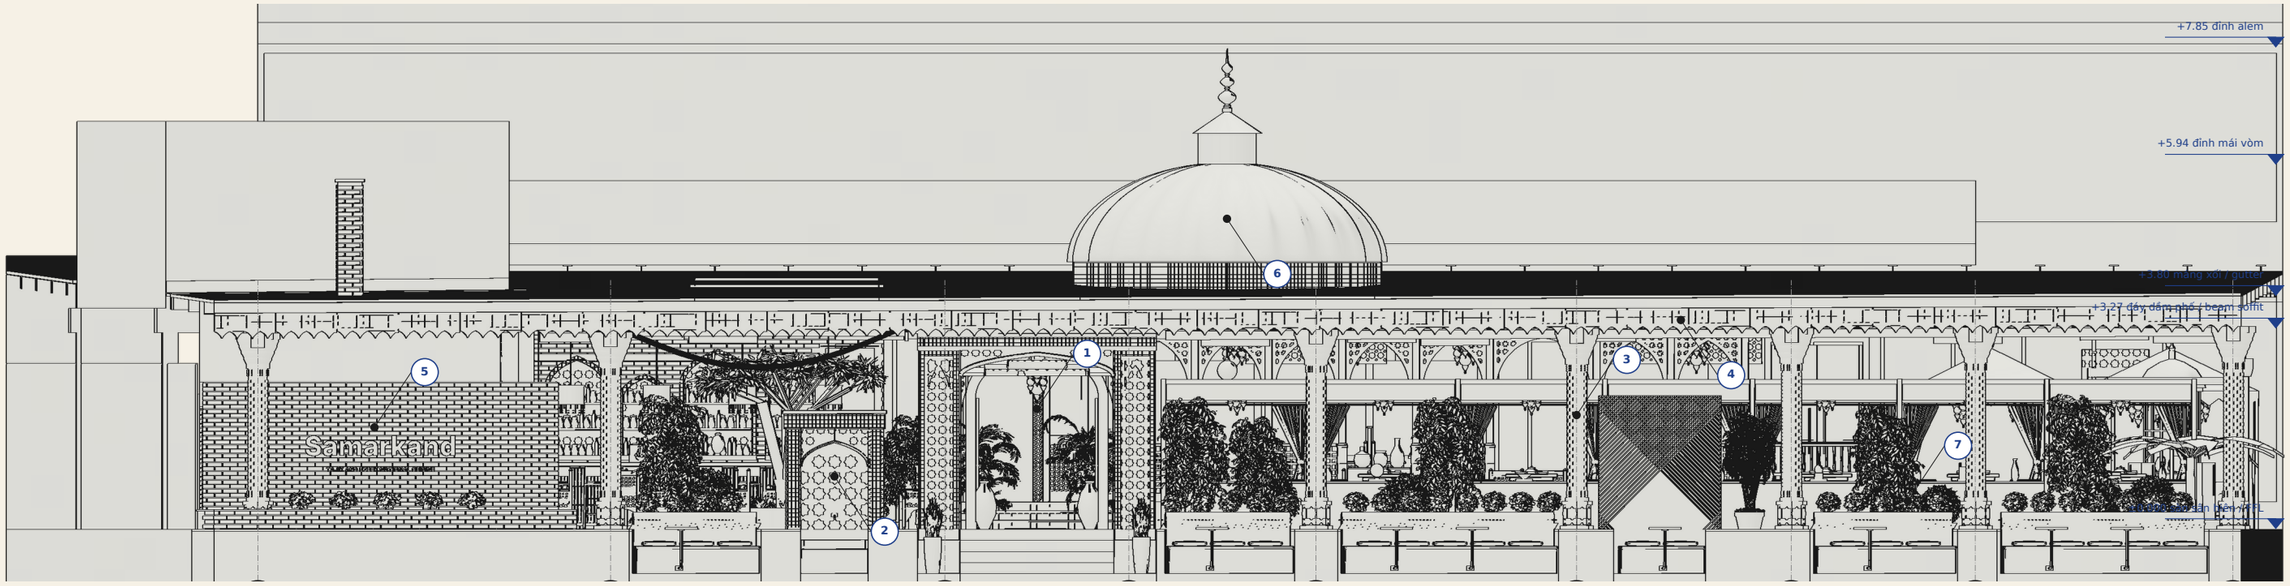

1 MẶT ĐỨNG HƯỚNG PHỐ (ĐÔNG)

Street elevation (East) · TL 1:100

#	Chú thích / Key
1	Cổng pishtaq — gạch men sao 8 cánh, vòm nhọn, muqarnas
2	Sebil — đài nước, vòi đồng
3	Cột Samarkand: lõi thép SHS150, bọc gạch cong + men
4	Diềm mái gỗ óc chó + 2 hàng gạch men 100 + diềm chạm nhọn
5	Mangal — tường gạch hazarbaf + men lam
6	Mái vòm: tráng men lam ngọc, đèn lồng, alem đồng
7	Ghế xây trát vữa vôi + đệm, bồn cây

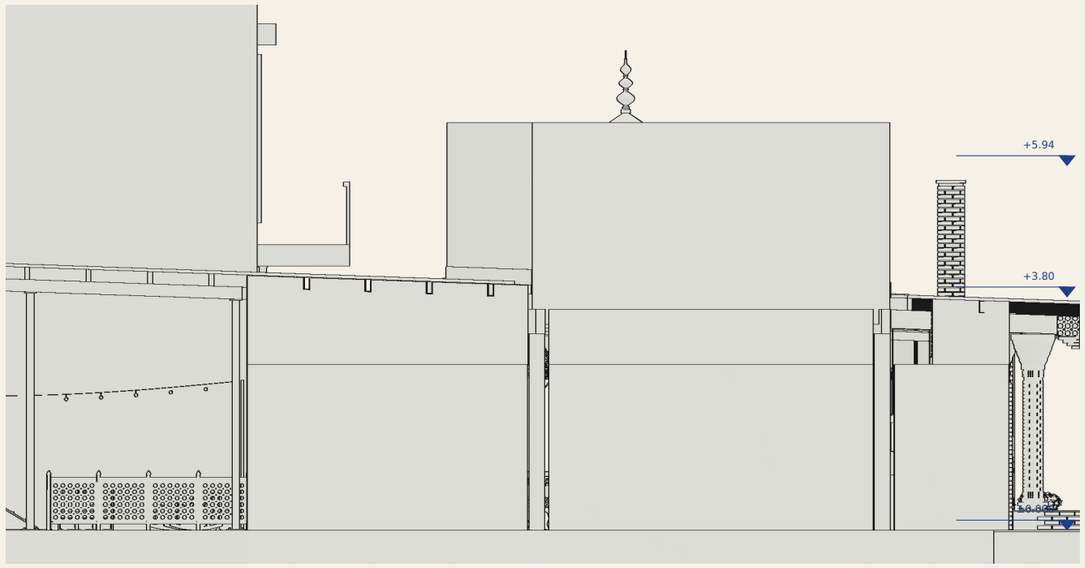

2 MẶT ĐỨNG HƯỚNG NAM

South elevation · TL 1:100

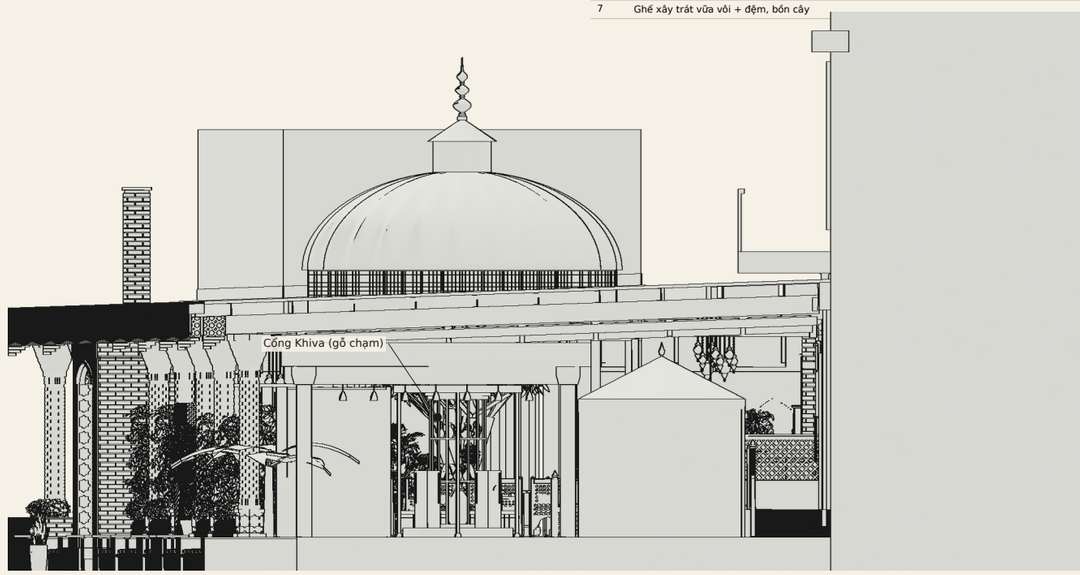

3 MẶT ĐỨNG HƯỚNG BẮC

North elevation · TL 1:100

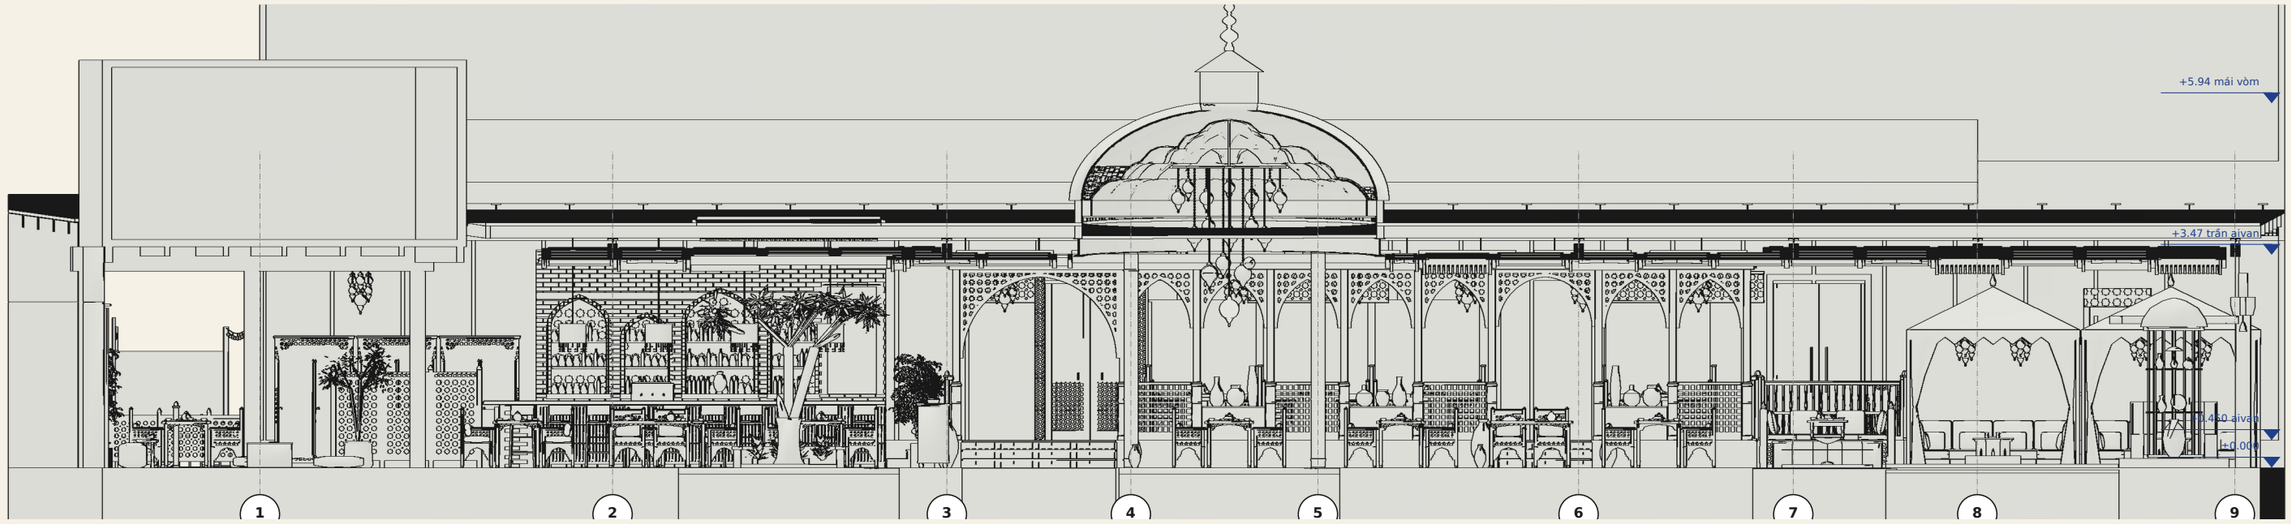

1 **MẶT CẮT A-A (DỌC, QUA MÁI VÒM & CÂY)**
Section A-A (longitudinal, looking to the hall) · TL 1:100

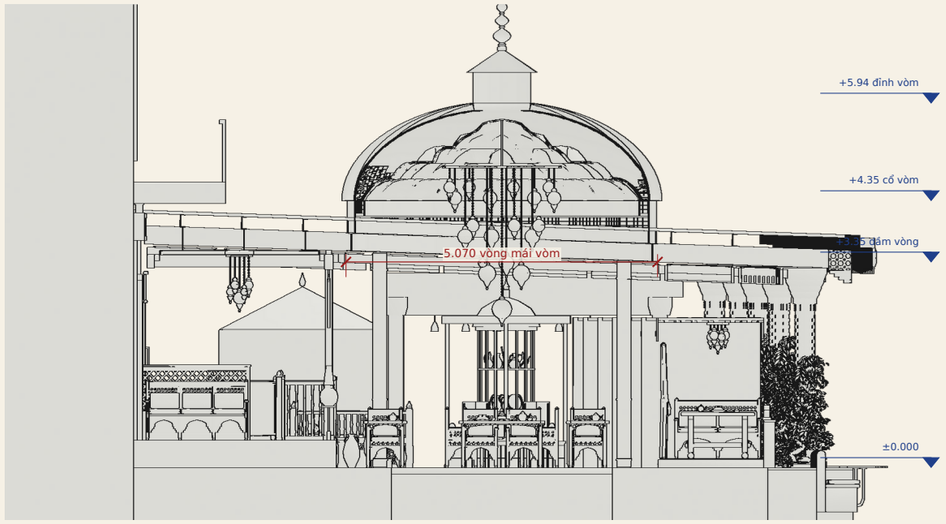

2 **MẶT CẮT B-B (NGANG QUA MÁI VÒM)**
Section B-B (transverse, dome) · TL 1:100

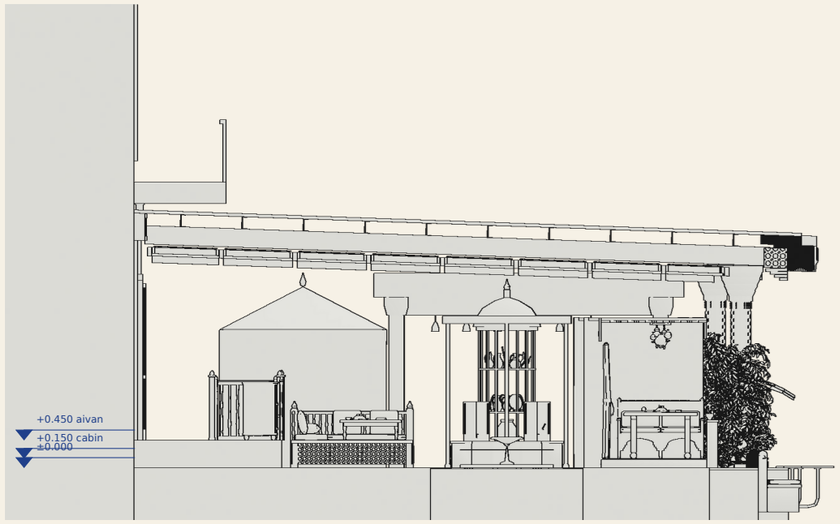

3 **MẶT CẮT C-C (NGANG QUA AIVAN, SẢNH, CABIN)**
Section C-C (aivan · hall · booth) · TL 1:100

Vị trí cắt: xem KT-03
Section marks on KT-03

CHI TIẾT CỘT SAMARKAND & CỔNG PISHTAQ

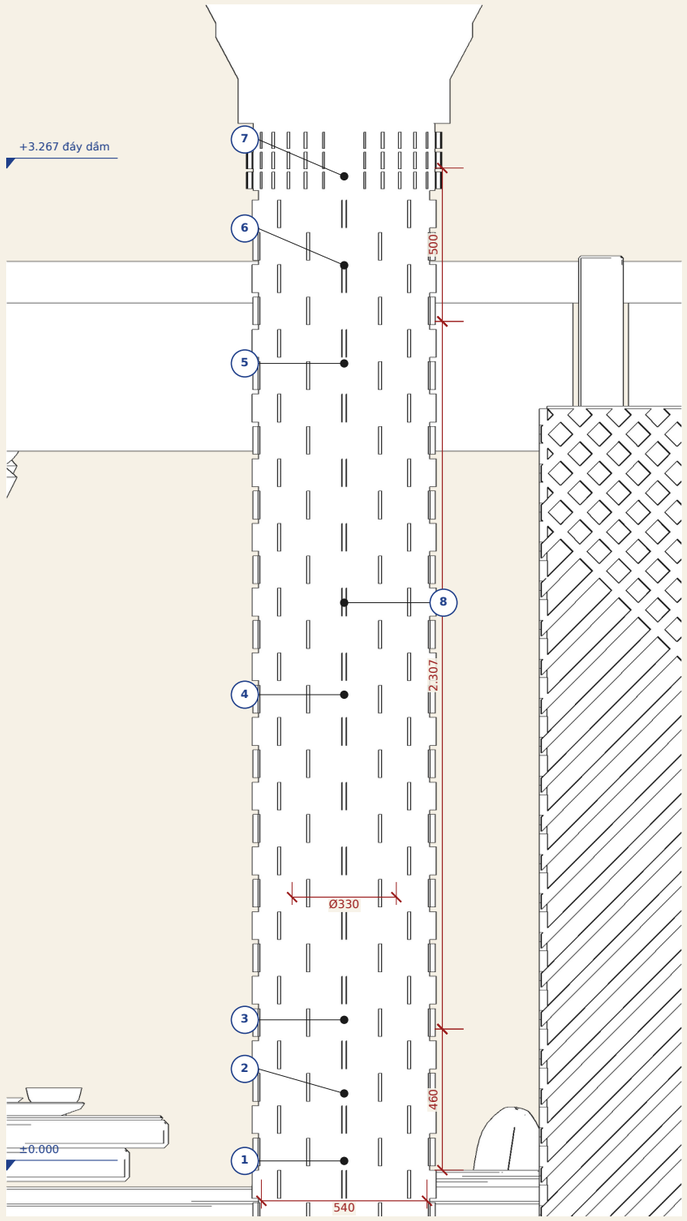

1 CHI TIẾT CỘT SAMARKAND & CỔNG PISHTAQ
Samarkand column & pishtaq · TL / Scale 1:20

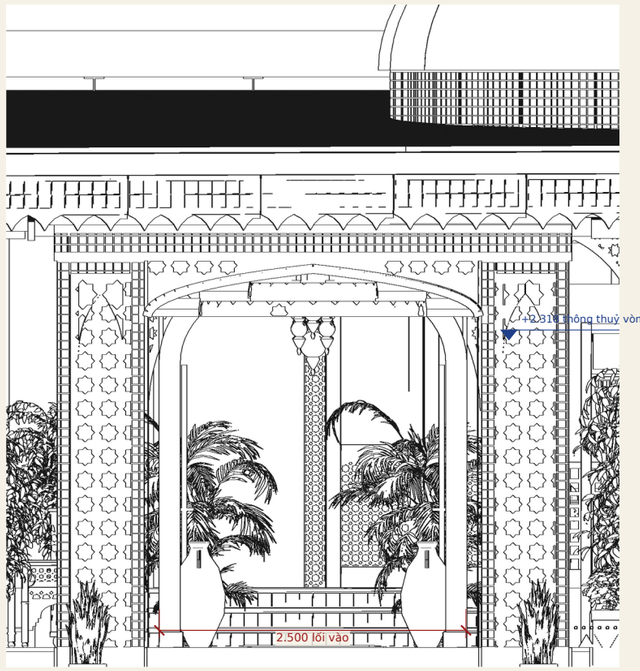

2 MẶT ĐỨNG CỔNG PISHTAQ
Pishtaq portal elevation · TL 1:50

CHÚ THÍCH CẤU TẠO / CONSTRUCTION KEY

1. Bệ đá ashlar bát giác r=270, cao 60
   Octagonal ashlar plinth r 270 × 60
2. Thân bệ ốp gạch men sao girih (bát giác r=230), cao 340
   Girih star-tile die, h 340
3. Gờ đá + băng kufic gạch men 30×30 (Ø350)
   Stone ring + square-kufic glazed band
4. Thân cột: gạch cong 120×50 mạch 8, men lam xếp lưới thoi (Ø330)
   Curved brick courses, glazed diamond lattice
5. Băng kufic trên + gờ đá
   Upper kufic band + stone ring
6. Đầu cột muqarnas 4 tầng gạch men lam/ngọc, mỗi tầng 100
   4-tier glazed muqarnas capital
7. Đế đỡ đá + bản mã liên kết dầm I300
   Stone abacus + beam seat plate
8. Lõi thép SHS 150×150×6 (kết cấu) — gạch neo bằng ty inox 316 @300
   Steel core, SS316 ties @300

GHI CHÚ / NOTES

- Gạch thân cột là gạch cong đặt hàng (bán kính 165) — không dùng gạch phẳng cắt.
- Mạch vữa vôi-xi măng 8 mm, lõm 3 mm; men: cobalt RAL 5002 / ngọc lam.
- Bọc lõi thép bằng lưới thép + vữa 20 trước khi ốp; chừa khe co giãn 10 ở đỉnh.
- Đầu cột muqarnas đúc GRC sẵn theo 4 tầng, ốp gạch men, lắp bu lông.
- Custom curved brick (r 165), 8 mm recessed joints; GRC muqarnas precast in 4 tiers.
- SL / Qty: 7 cột phố + cổng.

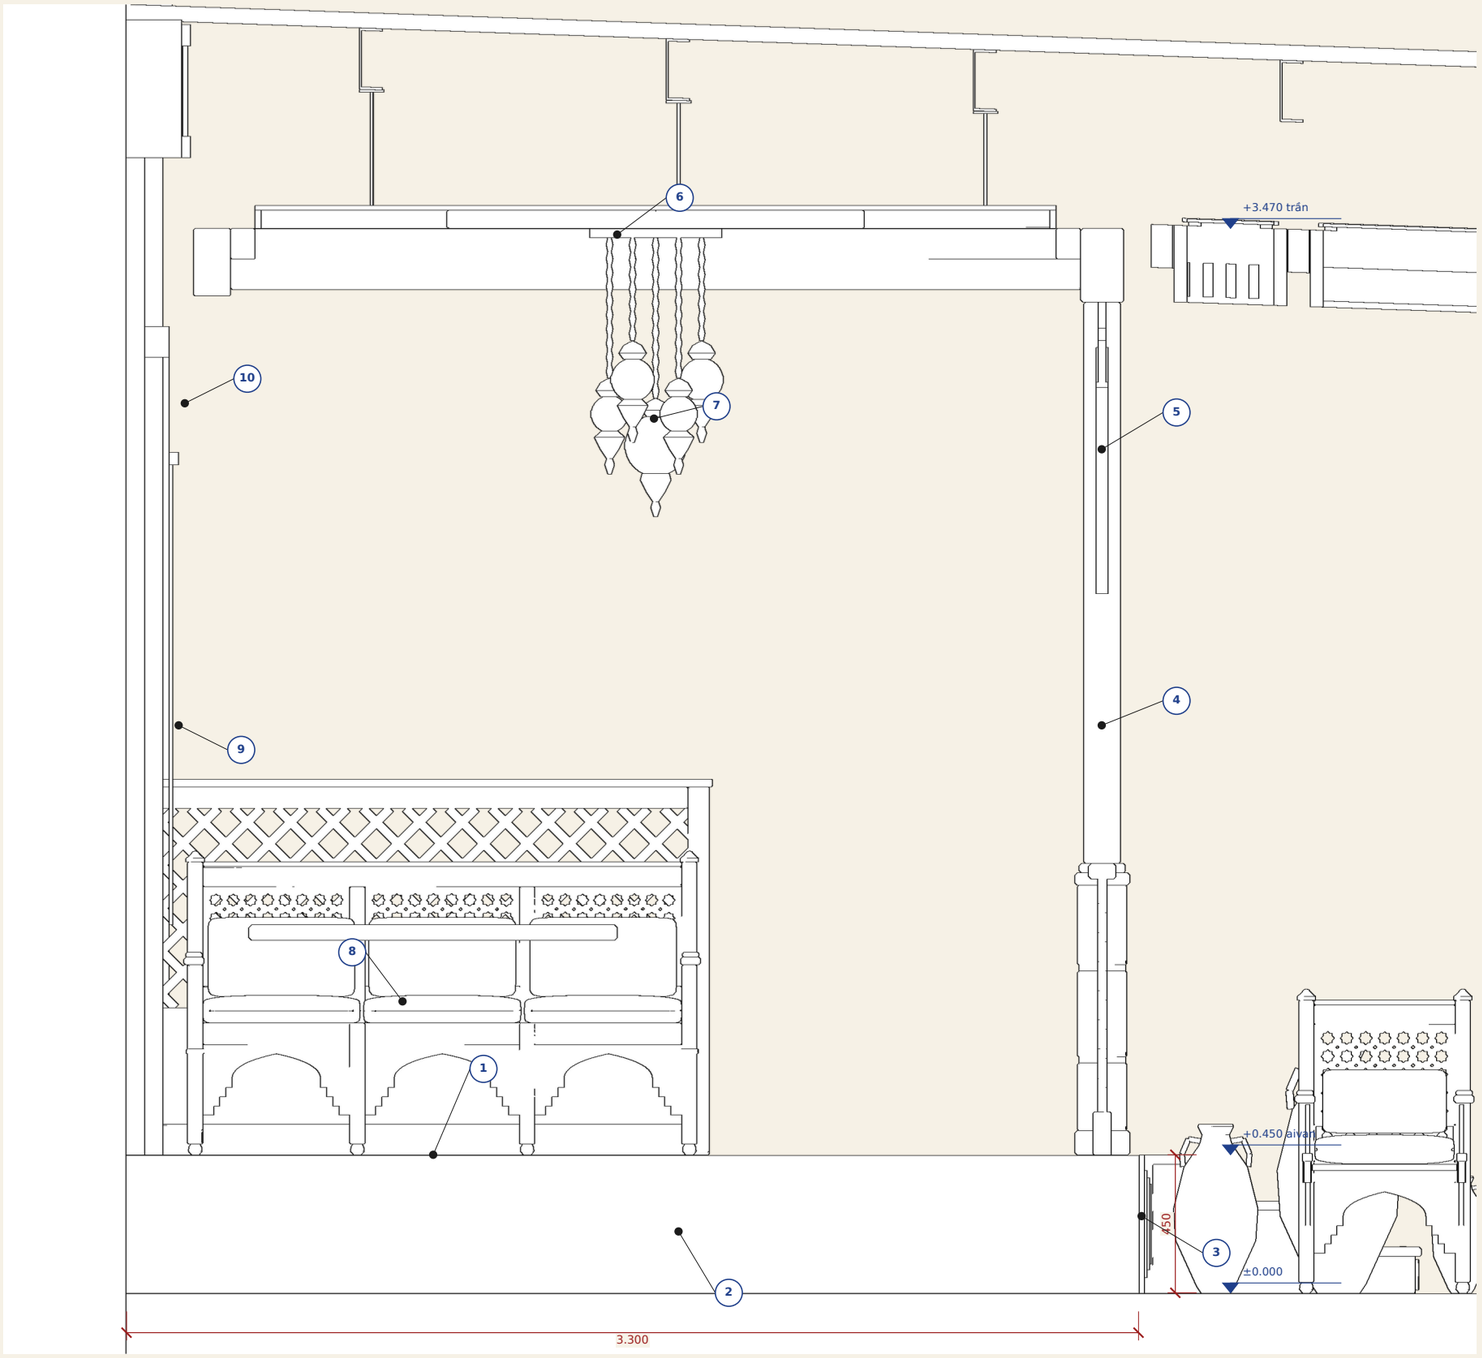

CHÚ THÍCH CẤU TẠO / CONSTRUCTION KEY

1. Sàn gạch nung 300×150 xếp chong chóng + gạch men 150 (F3)
   Terracotta pinwheel + glazed inserts
2. Kết cấu sàn: khung thép hộp 100×50, tấm xi măng 20, vữa 30, keo C2TE
   Steel frame + 20 cement board + bed
3. Mặt dựng sàn aivan ốp gỗ óc chó
   Walnut-clad deck face
4. Cột Khiva gỗ chạm 180×180, chân đế đồng
   Carved Khiva column 180×180
5. Đầu vòm chạm (arcade) + dầm gỗ
   Carved arcade head + beam
6. Trần ô hộp aivan +3.47: khung gỗ, thảm, LED hắt
   Coffered aivan ceiling
7. Đèn chùm kiểu mái vòm (7 bộ, tâm mỗi ô trần)
   Cascade chandelier at coffer centre
8. Sofa 3 chỗ 1660, đệm thảm có viền
   3-seat carved settee
9. Thảm treo tường trong khung, thanh đồng
   Wall carpets on brass rods
10. Diềm gỗ chạm sao thay zardevor
    Carved walnut frieze

GHI CHÚ / NOTES

- Mẫu chong chóng: gạch 300×150 quay quanh ô vuông 150 (gạch men); lưới lặp (300,150)/(−150,300). Mạch 3 mm vữa xám. Viền giữ bằng nẹp đồng.
- Pinwheel: 300×150 pavers round a 150 glazed insert; 3 mm grey joints.
- Lan can bậc thang đá bó: đặt bình gốm 3 cỡ (800 / 550 / 380) hai bên.
- Bậc: 3 bậc cao 150, mặt đá dày 30 mũi 20, cổ bậc gạch men 100.
- Bàn aivan: chân chữ T đặt giữa (xem CT-11).

1 CHI TIẾT AIVAN
Aivan — section & finishes · TL / Scale 1:20

CHI TIẾT CABIN VIP

VIP BOOTH — SECTION & PLAN

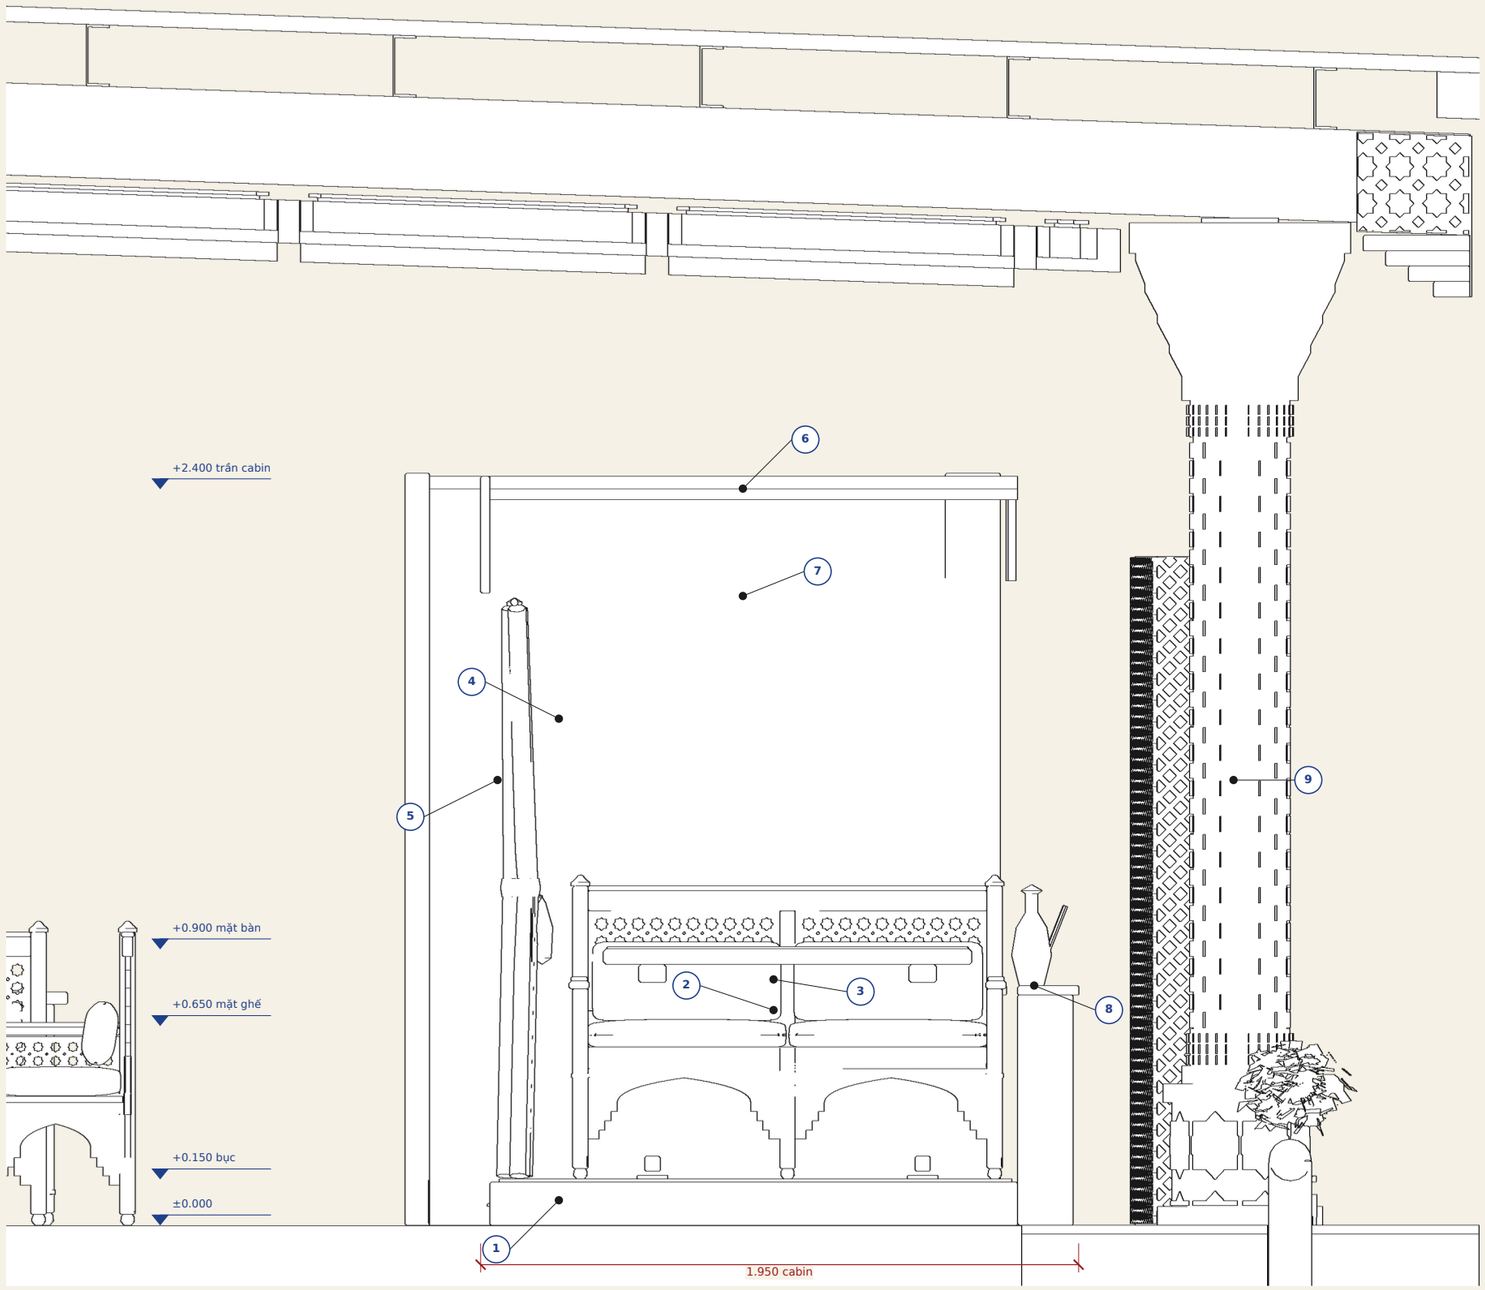

CHÚ THÍCH CẤU TẠO / CONSTRUCTION KEY

1. Bục cabin +0.150: khung gỗ, mặt ván, thảm Ba Tư; mặt dựng óc chó + nẹp đồng
   Podium, walnut riser, brass strip
2. Sofa 2 chỗ 1400 (700/người), đệm thảm có viền ống
   Wide 2-seat settee, piped rug cushions
3. Bàn chân chữ T 1200×850, mặt gỗ dày 50
   Trestle table 1200×850
4. Vách lưới gỗ óc chó 40 hai mặt + lõi MDF 18 sơn than
   Walnut lattice both faces, 18 charcoal MDF core
5. Rèm nhung, thanh đồng Ø24 dưới biển tên, vòng vén đồng + tua
   Velvet curtains, brass rod, tie-back
6. Trần lưới gỗ +2.40 trên tấm than
   Lattice ceiling +2.40
7. Đèn chùm kiểu mái vòm trên bàn
   Cascade chandelier over the table
8. Lan can phía phố cao 780, mũ đá trắng
   Street parapet h 780, stone cap
9. Cột Samarkand (CT-01)
   Samarkand column
10. Diềm mái phố (CT-08)
    Street eave

GHI CHÚ / NOTES

- Cabin 2.400 × 1.950; sofa 1400 sâu 546; bàn 1200 × 850; mép ghế — mép bàn ≈190.
- Booth 2.400 × 1.950; settee 1400 × 546; table 1200 × 850.
- Sofa đặt sâu sát lan can; lối vào phía hành lang thông thoáng ≥ 270.
- Ổ cắm 2S2U trên lan can +0.600 (2 / cabin).
- Rèm: nhung chống cháy, 2 tấm / cabin, màu theo cabin (vang / ngọc / lá / mật ong).
- 7 cabin: Samarkand, Bukhara, Khiva, Khujand, Penjikent, Tashkent, Margilan.

1 **CHI TIẾT CABIN VIP**
VIP booth — section & plan · TL / Scale 1:20

CHI TIẾT TRẦN Ô HỘP

C1 — Ô thảm Ba Tư + LED hắt / carpet coffer

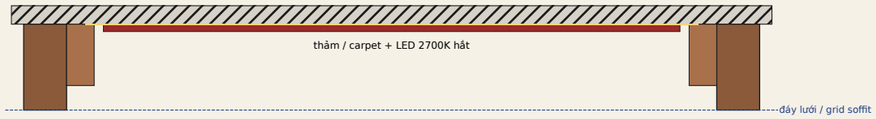

module 1200 · dầm lưới 70×140 · khung 45

C2 — Hộp nan gỗ hạ 150 / dropped slat box

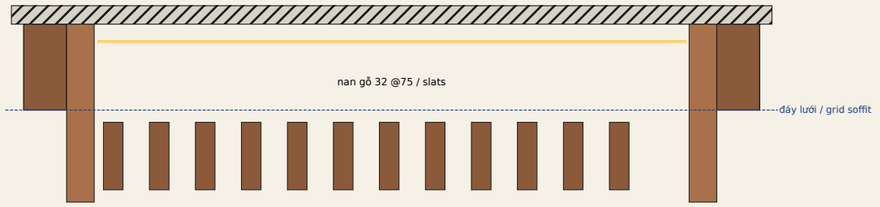

module 1200 · dầm lưới 70×140 · khung 45

C3 — Ô thảm + sườn chéo / ribbed carpet

module 1200 · dầm lưới 70×140 · khung 45

C4 — Ô sâu (khung hạ 100) + sườn / deep coffer

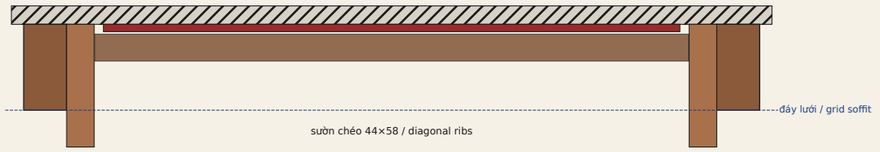

module 1200 · dầm lưới 70×140 · khung 45

Tất cả mặt cắt TL 1:10 (kích thước mm) / all sections 1:10

THÔNG SỐ / SPECIFICATION

Trần treo dưới dầm mái 130 (đi theo dốc 3,5 %).
Suspended 130 under the roof beams (3.5 % fall).

Lưới gỗ óc chó 70×140 module ≈1,2 m, liên kết
bằng ke thép ẩn + ty treo M8 @1200 vào xà gồ.

Khung ô: gỗ 45×100 (C4: 45×200).
Thảm: ảnh 19 thảm Ba Tư của chủ đầu tư,
dán lên ván MDF 9 chống cháy, khung nẹp.

LED dây 2700K, 9,6 W/m, IP20, driver 24 V
đặt trong khoang kỹ thuật, có cửa thăm.

Lỗ chờ: ống treo đèn chùm, đầu báo khói,
quạt / điều hoà (phối hợp M&E).

Mở: mái vòm (Ø5,07 vuông) và giếng trời
3,0 × 3,0 m giữ trống.

Số lượng ô: 150 (xem KT-05).

CHI TIẾT MÁI VÒM

DOME — SECTION

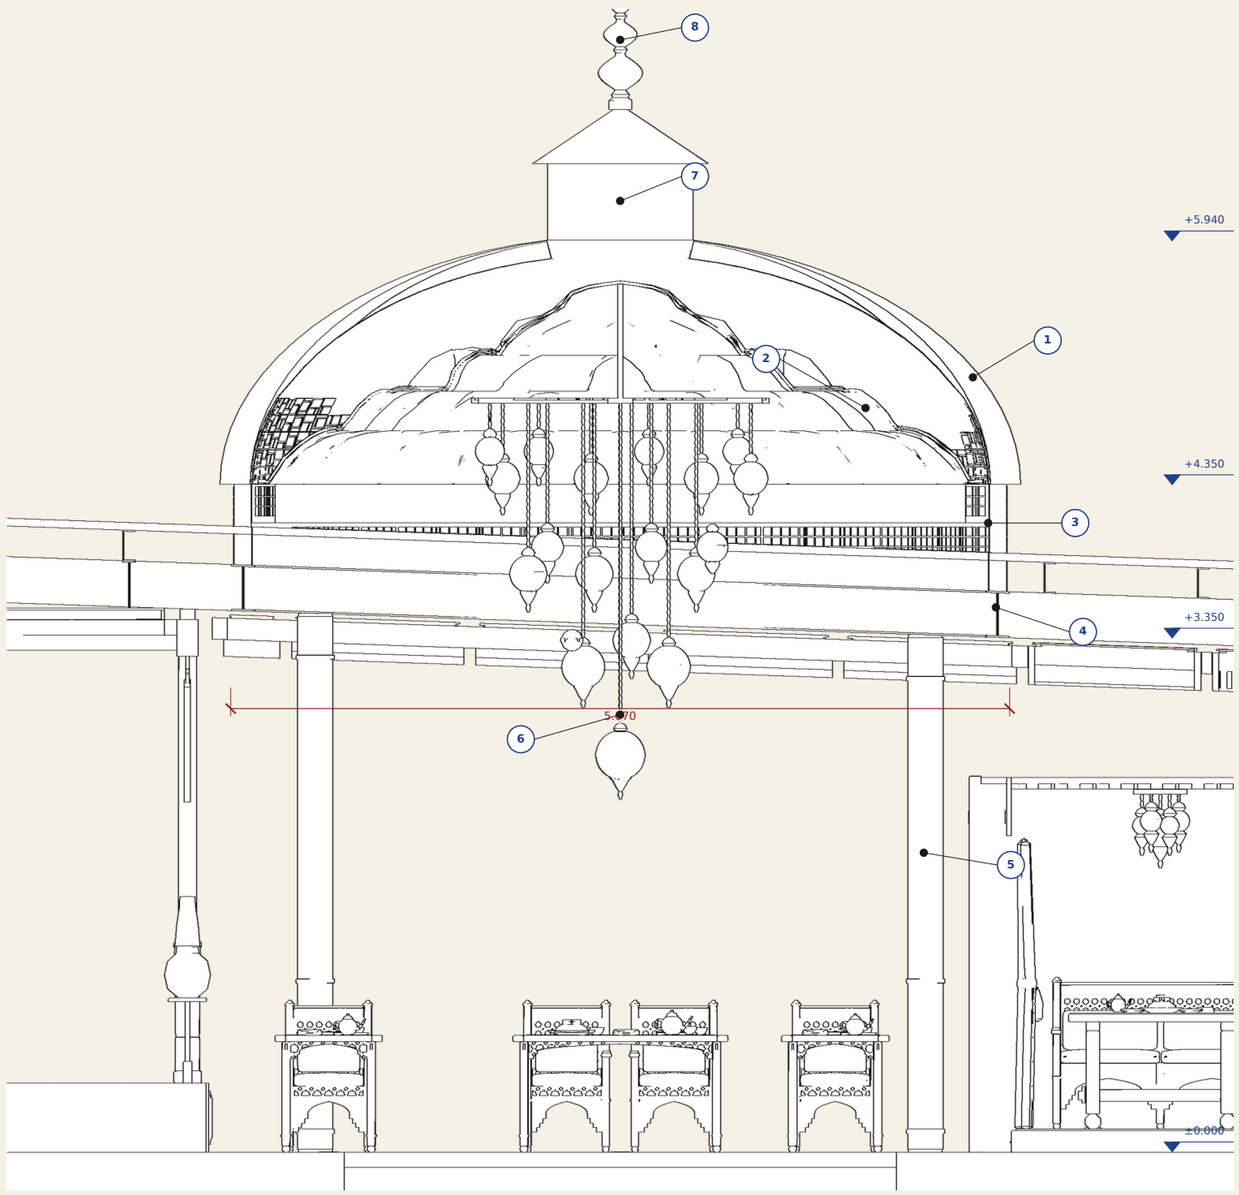

1 **CHI TIẾT MÁI VÒM**
Dome — section · TL / Scale 1:40

CHÚ THÍCH CẤU TẠO / CONSTRUCTION KEY

1. Vỏ mái vòm: sườn thép cong + tấm GRC, ốp gạch men lam (gân dưa)
   Ribbed shell, glazed tiles
2. Mặt trong karbandi (sơn vẽ hoa văn)
   Painted karbandi interior
3. Cổ vòm có cửa sổ, gạch kufic
   Drum with windows, kufic band
4. Dầm vòng thép hộp + ốp gỗ
   Steel ring girder, timber clad
5. Cột đỡ vòm SHS150 bọc gỗ chạm (4 cột)
   Dome column, carved casing
6. Đèn chùm thác cầu đồng đục lỗ (61 cầu) treo từ đỉnh
   Cascade chandelier, crown hook
7. Đèn lồng đỉnh vòm + mũ
   Lantern + cap
8. Alem đồng thau
   Brass finial

GHI CHÚ / NOTES

- Kết cấu vòm & neo đèn chùm (≈180 kg) — kỹ sư kết cấu tính.
- Móc treo inox 316 tại đỉnh, xích an toàn phụ.
- Gạch men lam ngọc ốp ngoài bằng keo ngoài trời + ron epoxy.
- Chống thấm: màng PU dưới lớp ốp, điểm thoát nước tại cổ vòm.
- Mặt trong: thạch cao chịu ẩm, sơn vẽ tay theo mẫu karbandi.

CHI TIẾT QUẦY BAR

CHÚ THÍCH CẤU TẠO / CONSTRUCTION KEY

1. Tường bar: gạch bannai + hốc vòm, kệ gỗ
   Bannai brick back wall with arched niches
2. Gờ phào gỗ chạm
   Carved cornice
3. Mặt quầy gỗ óc chó dày 40 +1.090
   Walnut counter top
4. Mặt quầy: terracotta rãnh đứng + gạch men
   Fluted terracotta front
5. Ghế bar gỗ (10 cái)
   Timber bar stools
6. Đèn trống kết hạt (4 bộ) — ống treo xuyên trần
   Beaded drum pendants
7. Trần ô hộp (C1–C4)
   Coffered ceiling

GHI CHÚ / NOTES

- Quầy dài 6.560; lối nhân viên 1.310; chân ghế cách quầy 150.
- Kỹ thuật dưới quầy: cấp/thoát nước, ổ cắm IP44, rãnh kỹ thuật 200 (phối hợp M&E).
- Tường hậu: lõi gạch + gạch bannai ốp, hốc vòm có LED 2700K, kệ gỗ.
- Bar length 6.56 m, staff aisle 1.31 m; MEP under counter by others.

1 **CHI TIẾT QUẦY BAR**
Bar — section · TL / Scale 1:20

CHI TIẾT HÀNH LANG VÒM

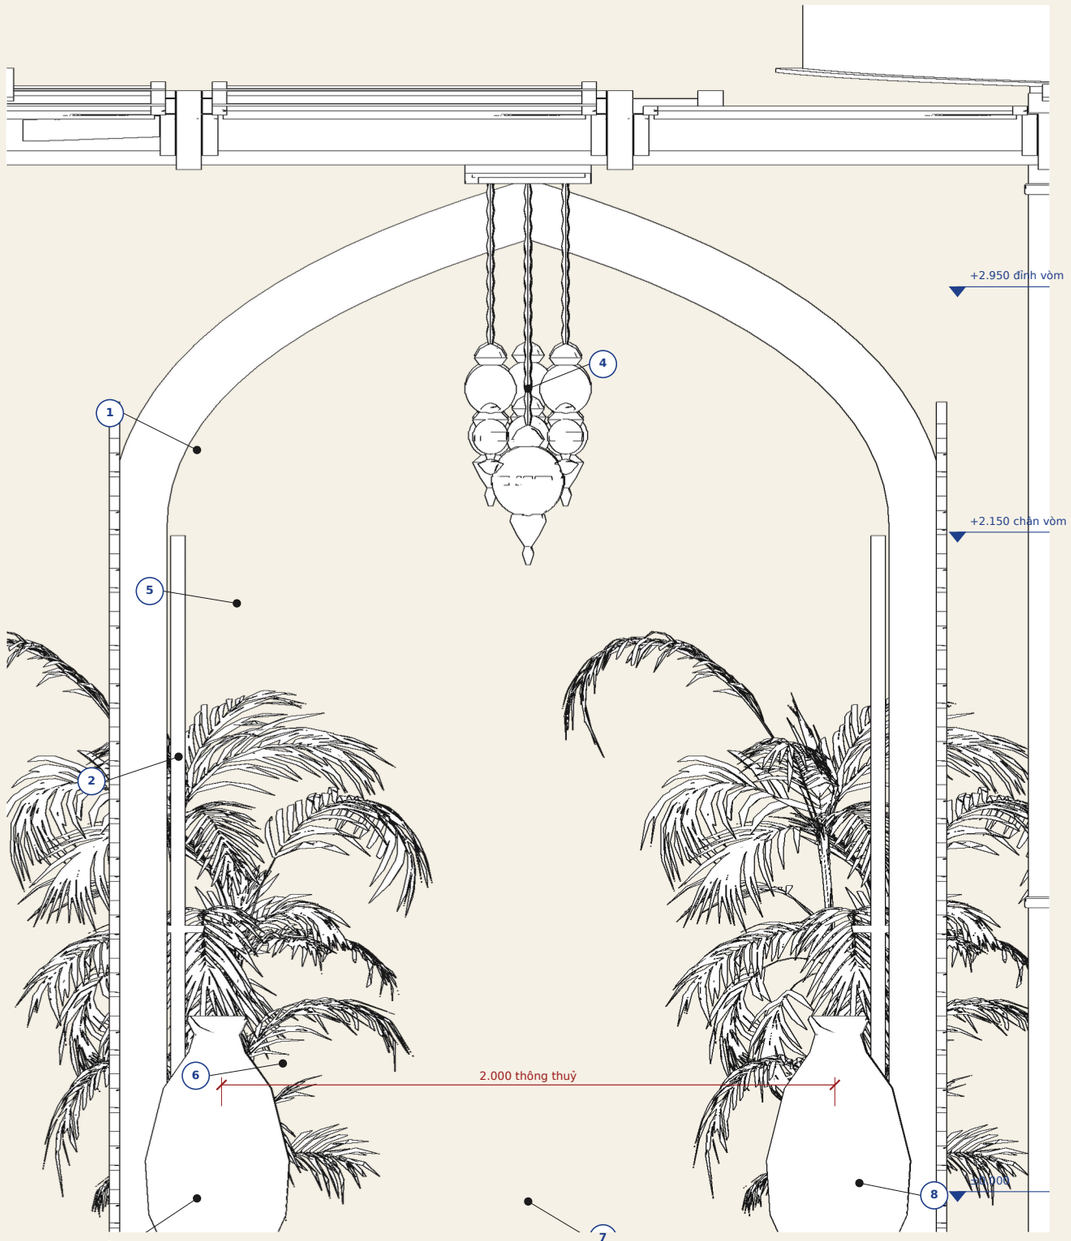

1 CHI TIẾT HÀNH LANG VÒM
Arcade corridor — section · TL / Scale 1:20

CHÚ THÍCH CẤU TẠO / CONSTRUCTION KEY

1. Vòm nhọn gỗ óc chó, bề mặt 160, dày 140 (4 vòm)
   Pointed walnut arch 160 face × 140
2. Vách lưới hoa văn sao cắt CNC gỗ óc chó dày 30, khung 60
   CNC star-lattice panel 30, frame 60
3. Dải LED hắt chân vách 2700K IP65
   Base uplight strip IP65
4. Đèn chùm kiểu mái vòm giữa các vòm
   Cascade chandelier between arches
5. Dải rèm nhung buộc, vòng đồng
   Tied velvet sash, brass ring
6. Bình gốm 3 cỡ
   Terracotta jugs
7. Lối gạch zellige sao (F2)
   Zellige star runner
8. Chân vòm bọc đồng cao 120
   Brass shoe h 120

GHI CHÚ / NOTES

- Vòm gỗ ghép thanh cong (glulam óc chó), liên kết ke inox ẩn vào sàn & trần.
- Lưới CNC: ván gỗ óc chó / MDF chống ẩm veneer óc chó dày 30.
- Hạn chế vải (gió, mưa): chỉ dải rèm buộc cố định.
- 4 arches at x = 7.75 / 8.60 / 9.45 / 10.25 m; panels between, uplights at the base.

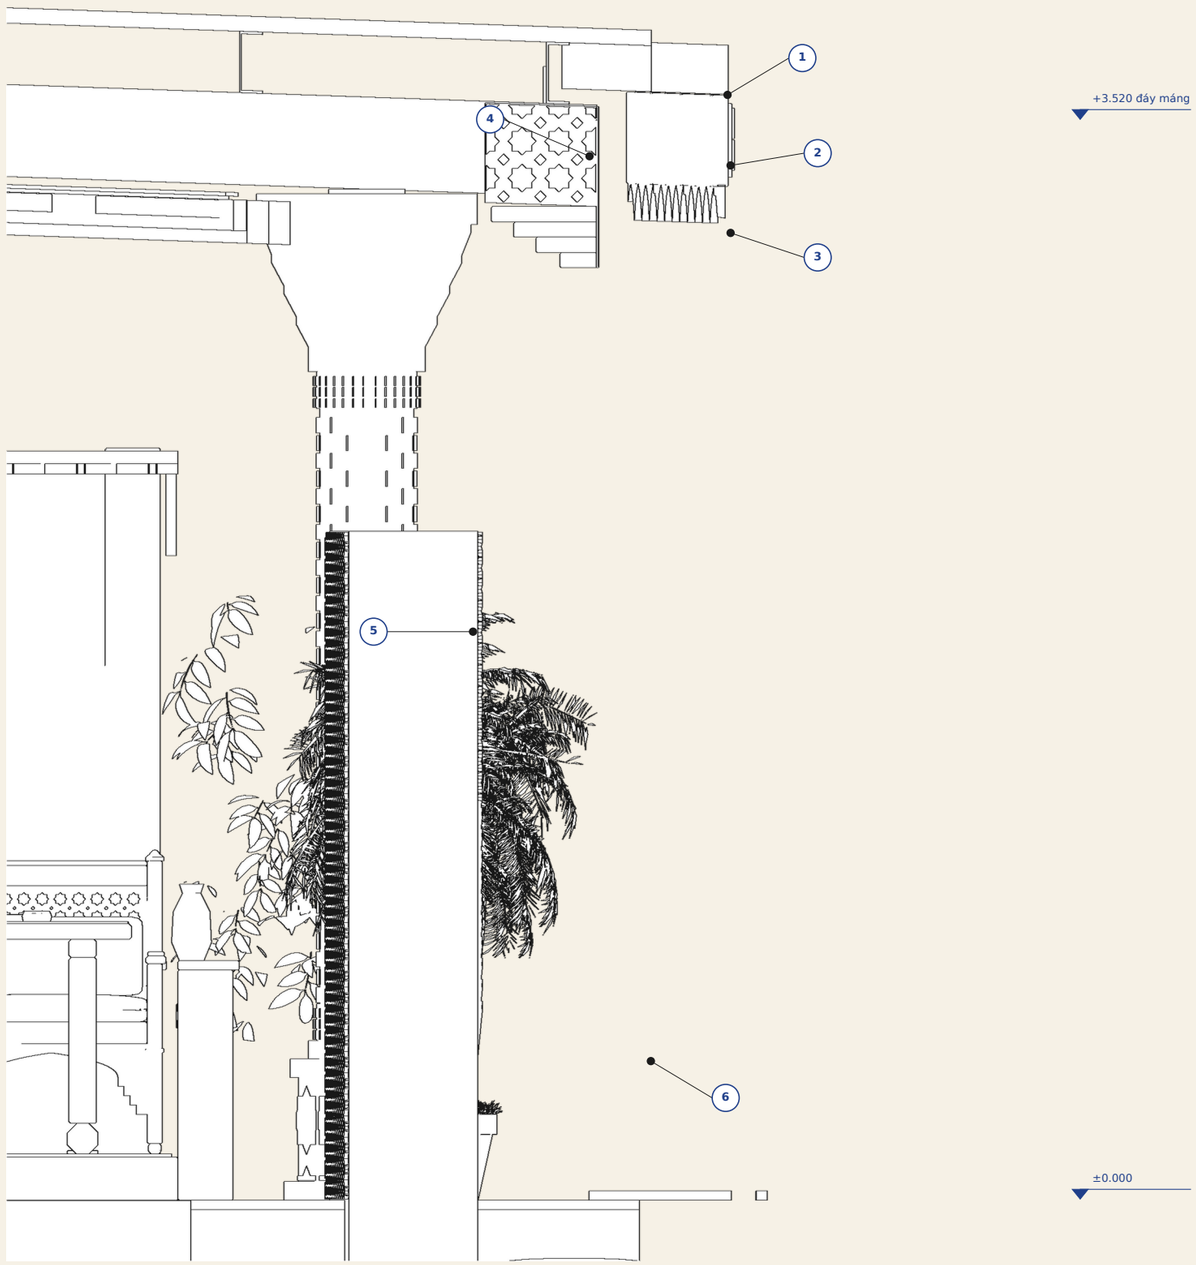

1 CHI TIẾT DIỀM MÁI MẶT TIỀN

Street eave — fascia, tiles, fringe, beam casing · TL / Scale 1:20

CHÚ THÍCH CẤU TẠO / CONSTRUCTION KEY

1. Máng xối phố (hiện trạng)
   Street gutter
2. Diềm gỗ óc chó 40×300 + 2 hàng gạch men 100 (cobalt/trắng/ngọc)
   Walnut fascia + glazed tile band
3. Diềm chạm nhọn gỗ 25, bước 250, lỗ tròn
   Carved pointed-drop fringe
4. Ốp dầm gỗ chạm sao + công-xon bậc + nắp đồng
   Carved beam casing, corbel, brass cap
5. Cột Samarkand (CT-01)
6. Ghế xây trát vôi + đệm, bồn cây
   Plaster bench + planter

GHI CHÚ / NOTES

- Diềm & ốp dầm: gỗ óc chó / teak xử lý ngoài trời, sơn dầu UV.
- Gạch men dán keo ngoài trời C2TES1, ron epoxy; khe co giãn mỗi 3 m.
- Liên kết vào máng / dầm: ke inox 316 + bu lông M10.
- Diềm chạm cắt CNC, cạnh vê 3 mm, sơn chống thấm 2 lớp.

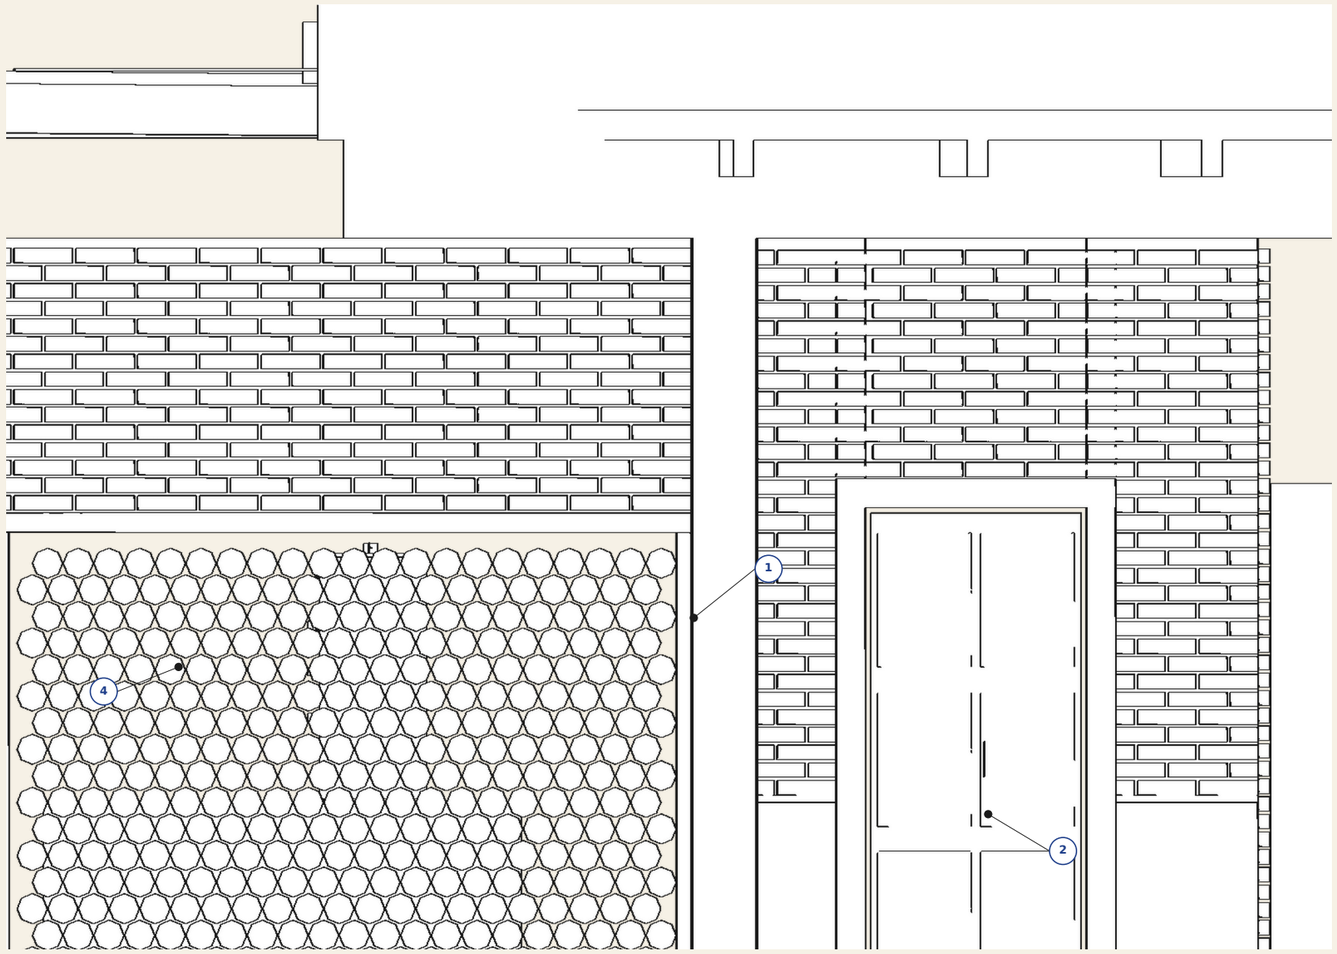

1 **CHI TIẾT KHU MANGAL**

Mangal — wall elevation · TL / Scale 1:25

CHÚ THÍCH CẤU TẠO / CONSTRUCTION KEY

1. Tường gạch hazarbaf (gạch vàng + men lam thoi)
   Hazarbaf brick, glazed lattice
2. Cửa nhân viên
   Staff door
3. Tủ trưng bày kính + đế gạch
   Glass display on brick base
4. Đống củi trang trí
   Firewood stack

GHI CHÚ / NOTES

- Lõi tường xây gạch, ốp gạch thẻ hazarbaf 240×60 mạch lõm 12.
- Bếp mangal / tandoor / kazan: thiết bị chuyên dụng — hút khói theo M&E.
- Tường chịu nhiệt phía bếp: gạch chịu lửa + vữa chịu nhiệt.

Hạng mục	Quy cách / Specification
Đá / Slab	Marble trắng Carrara (hoặc tương đương) 500×500×20, đánh bóng mờ
Viền / Band	Cobalt 14 + trắng 62 + cobalt 14 (gạch men 20 dày)
Khảm / Inlay	Kim cương men: đen / mật ong / lá / nâu xen kẽ
Giao / Crossing	Ô cobalt 90×90 + kim cương mật ong
Ron / Joint	1,5 – 3 mm epoxy xám nhạt
Lớp lót / Bed	Vữa xi măng cát 40 + keo C2TE; khe co giãn @6 m
Dung sai / Tol.	Độ phẳng ≤ 2 mm / 2 m; chống trơn R10

Cấu tạo sàn F1 / Floor build-up:

1. Đá marble 20 + keo C2TE 5
2. Vữa lót 40 (có lưới thép D4 @200 ở sân hiên ngoài trời)
3. Màng chống thấm PU 1,5 mm (khu ngoài trời)
4. Sàn bê tông hiện trạng — kiểm tra cao độ, tạo dốc 1 % ra phố

Chuyển tiếp: nẹp đồng 3×20 giữa F1 / F2 / F3 / F5

Transitions: 3×20 brass strip between finishes

CHI TIẾT NỘI THẤT: GHẾ, SOFA, BÀN

FURNITURE — CARVED CHAIR, SETTEES, TRESTLE TABLE

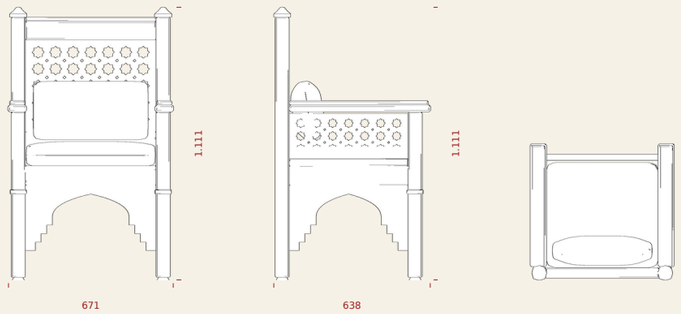

Mặt trước / front — Mặt bên / side — Mặt bằng / plan

GHẾ GỖ CHẠM (58 CÁI)

Carved armchair

671 × 638 × 1111 mm (R × S × C / W × D × H)

Mặt ngồi +468, đệm thảm có viền

Lưng lưới sao chạm, chân đồng

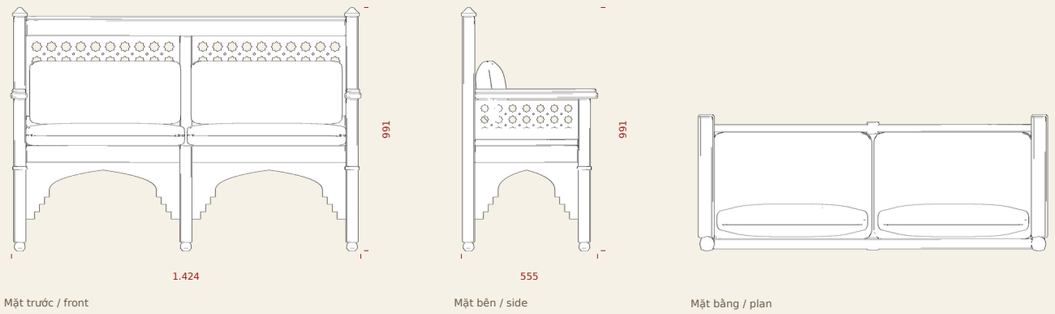

Mặt trước / front — Mặt bên / side — Mặt bằng / plan

SOFA CABIN 2 CHỖ (14 CÁI)

Booth settee 2-seat

1424 × 555 × 991 mm (R × S × C / W × D × H)

Mặt ngồi +500 trên bục +0.150

Đệm thảm Ba Tư có viền ống

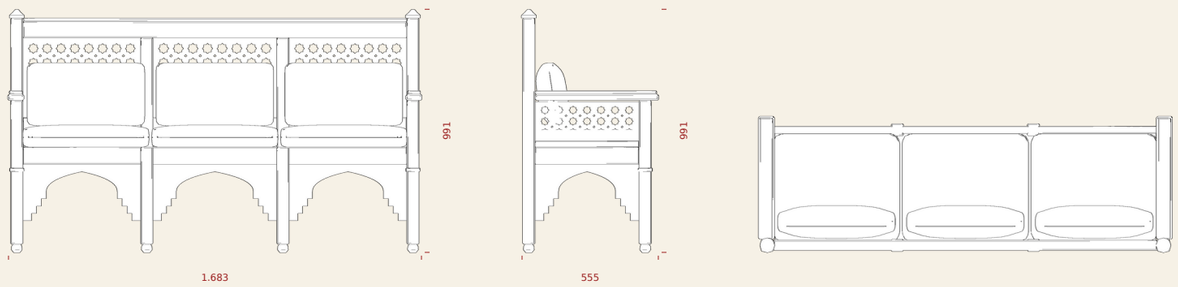

Mặt trước / front — Mặt bên / side — Mặt bằng / plan

SOFA AIVAN 3 CHỖ (8 CÁI)

Aivan settee 3-seat

1683 × 555 × 991 mm (R × S × C / W × D × H)

Cùng mẫu với sofa cabin

Đệm thảm có viền

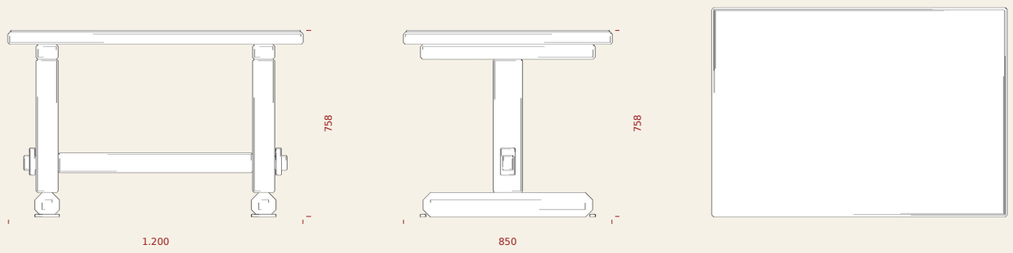

Mặt trước / front — Mặt bên / side — Mặt bằng / plan

BÀN CHÂN CHỮ T (CABIN 7 / AIVAN 4)

Trestle table

1200 × 850 × 758 mm (R × S × C / W × D × H)

Mặt gỗ dày 50, chân giữa + thanh giằng

Cabin 1200 × 850 · aivan 1200 × 560

TL / Scale 1:25 · gỗ óc chó / walnut, PU mờ / matt PU

BẢNG VẬT LIỆU HOÀN THIỆN

FINISHES & MATERIALS SCHEDULE

Mã	Vị trí / Location	Vật liệu & quy cách / Material & spec	Chi tiết
F1	Sàn sảnh	Marble trắng 500×500 chéo 45°, viền cobalt 90, khảm kim cương	KT-04, CT-10
F2	Sàn hành lang	Gạch zellige sao 8 cánh trên nền men trắng	CT-07
F3	Sàn aivan	Gạch nung 300×150 chong chóng + gạch men 150	CT-02
F4	Bục cabin	Gỗ óc chó + thảm Ba Tư, nẹp đồng	CT-03
F5	Sàn trẻ em	Cao su EPDM 500×500, 4 màu	KT-04
W1	Cột phố	Gạch cong + men lam, kufic, muqarnas, bệ đá	CT-01
W2	Pishtaq / sebil	Gạch men sao girih, kufic gạch, vòm nhọn	CT-01
W3	Tường bar	Gạch bannai + hốc vòm, kệ gỗ	CT-06
W4	Tường mangal	Gạch hazarbaf vàng + men lam	CT-09
W5	Tường đất (ranh nam)	Vữa đất sét, hốc vòm nổi, thảm khung đèn hắt	KT-07
W6	Vách cabin	Lưới gỗ óc chó 40 hai mặt + lõi MDF than 18	CT-03
C1–C4	Trần	Ô hộp gỗ óc chó, thảm Ba Tư, nan gỗ, LED 2700K	CT-04
C5	Trần aivan	Ô hộp gỗ, thảm kilim, sườn chéo	CT-02
C6	Mái vòm	Vỏ GRC ốp men lam ngọc, karbandi vẽ tay	CT-05
T1	Gỗ nội thất	Óc chó (walnut) vân thẳng, PU mờ; chạm khắc sao & kim cương	CT-11
T2	Kim loại	Đồng thau (bóng mờ), inox 316 ngoài trời	—
T3	Vải bọc	Thảm Ba Tư (ảnh chủ đầu tư) cho đệm; nhung chống cháy cho rèm	CT-03
T4	Gạch men	Cobalt RAL 5002, ngọc lam, trắng, mật ong — men bóng	—

Ghi chú: mọi vật liệu cần mẫu thật được chủ đầu tư duyệt; gỗ có chứng chỉ độ ẩm; gạch men ngoài trời có hệ số hút nước ≤ 3 %.

Notes: real samples approved by the owner; timber with moisture certificate; outdoor tiles water absorption ≤ 3 %.

BẢNG CHIẾU SÁNG & ĐIỆN

LIGHTING & POWER SCHEDULE

Mã	Thiết bị / Fitting	SL / Qty	Thông số / Data
L1	Đèn chùm thác mái vòm (61 cầu đồng đục lỗ)	1	2700K · ~600 W LED · treo đỉnh vòm
L2	Đèn chùm nhỏ kiểu mái vòm (7 cầu)	7+3+3+4+7	Aivan · hành lang · pergola · lều · cabin
L3	Dải LED hắt ô trần	150 ô	2700K · 9,6 W/m · 24 V · IP20
L4	Dải LED chân vách hành lang	6	2700K · IP65
L5	Đèn trống kết hạt (bar)	4	2700K · E27 LED 8 W
L6	Đèn sưởi mangal	4	Hồng ngoại 2 kW — ổ riêng
L7	Bra đồng tường lửa	1	IP65
L8	Đèn hắt cây	3	IP67 · 2700K
L9	Đèn LED sau thảm khung	2	2700K · IP44
P1	Hộp ổ cắm sàn 2S2U	22	IP44 · cạnh bàn / sofa
P2	Ổ cắm lan can cabin	14	2 / cabin · +0.600
P3	Cấp nguồn bar / mangal	—	Theo M&E — RCBO 30 mA

Điều khiển: 4 kịch bản (ngày / chiều / tối / dọn dẹp), dimmer DALI hoặc 0–10 V cho L1–L3.

Controls: 4 scenes, DALI / 0-10 V dimming for L1–L3.

Mạch riêng cho mangal, bar, chiếu sáng trần, ổ cắm sàn; tủ điện phụ đặt trong kho nhân viên.

Tất cả thiết bị ngoài trời IP65, dây đi ống luồn chống cháy.

PHỐI CẢNH 1

Mặt tiền phố / street front

Cabin VIP nhìn từ phố / booths from the street

Sảnh nhìn về mái vòm / hall to the dome

Mái vòm & đèn chùm / dome & chandelier

PHỐI CẢNH 2

Aivan

Bên trong cabin / inside a booth

Hành lang vòm / arcade corridor

Quầy bar / bar