SAMARKAND

R12

Крытая терраса · планировка R12 · ред. 8

2026-10-28

Таджикская и узбекская кухня · Võ Nguyên Giáp, 254, Дананг

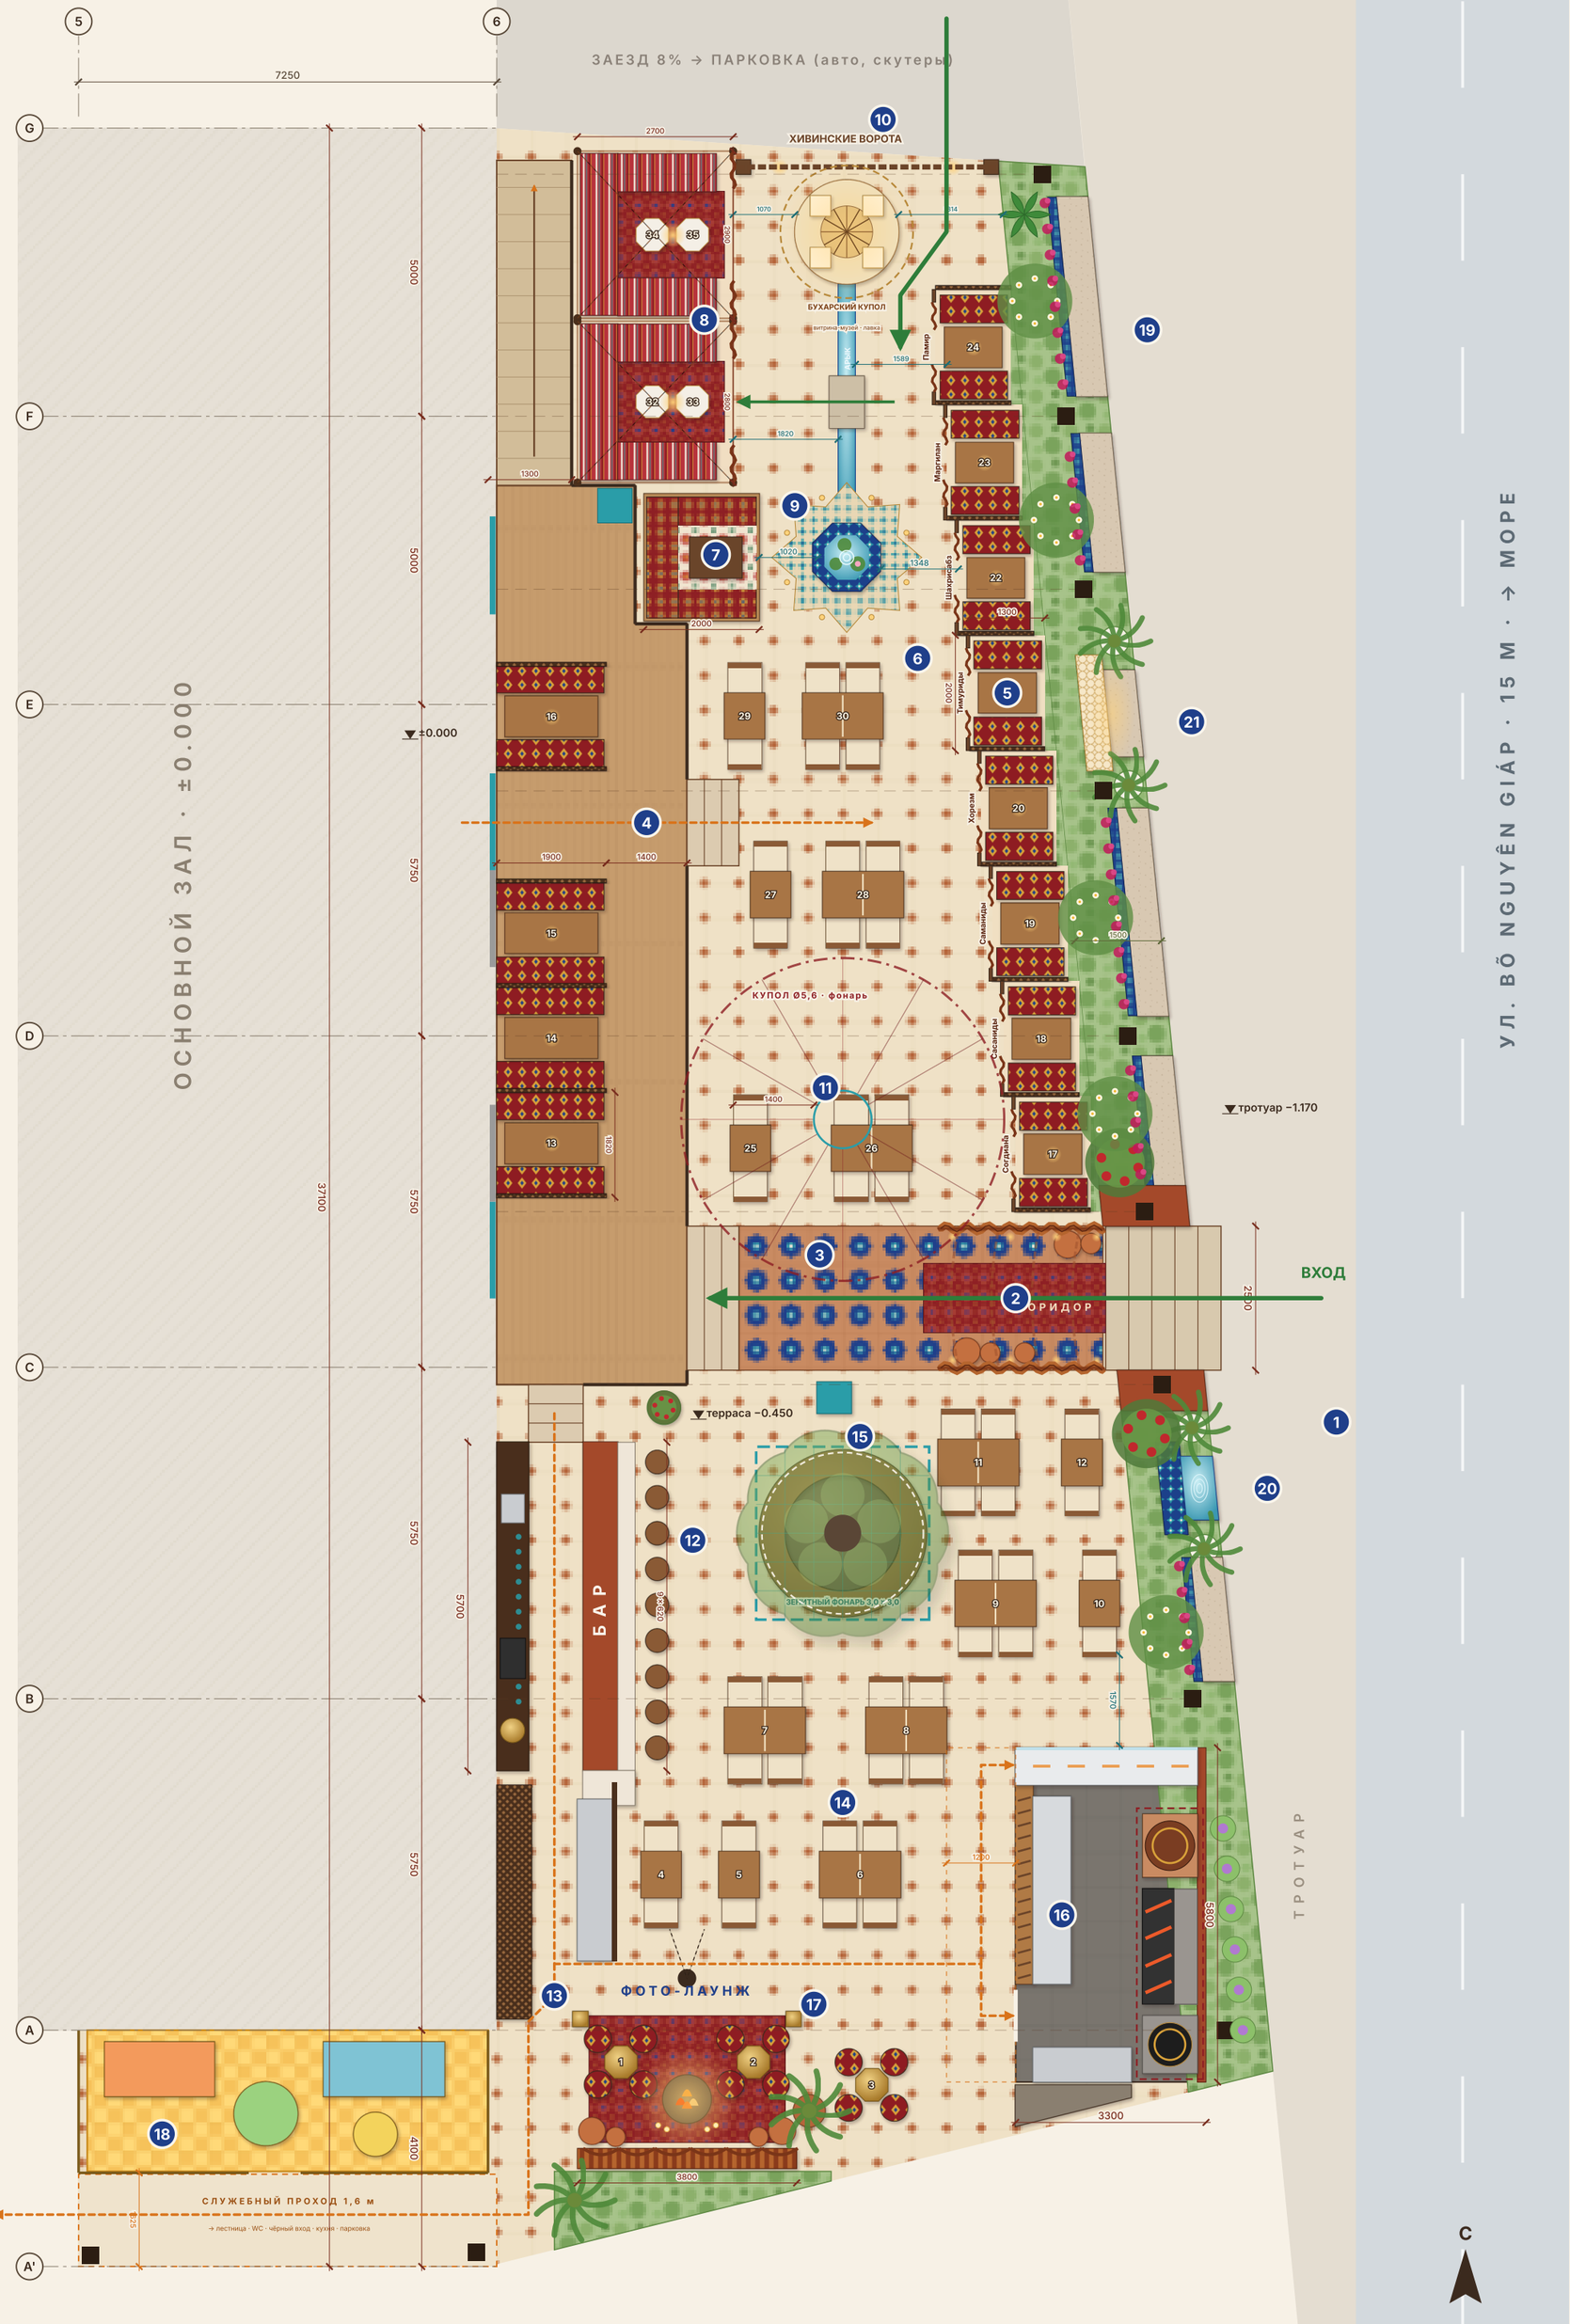

ЗОНЫ

1. **Главный вход · портал-пештак**
   проём 2,5 м, 4 ступени с тротуара
2. **Коридор-драпировка**
   бархатные сваги крест-накрест, ковры внахлёст, кувшины, свечи
3. **Аллея к залу**
   гирих, 2,5 м, хостес у выхода
4. **Айван-платформа ±0.000**
   4 седир-кабинки на 6, резные экраны, монитор 65″ к аллее
5. **Тематические кабинки**
   8 закрытых залов: эпохи и города, шторы-порталы
6. **Столы у фонтана**
   на 4 + на 2, на месте северного чинара
7. **Топчан 2,0 × 2,2 м**
   6 гостей, балясины, курпачи, столик на точёных ножках
8. **Два шатра-маджлиса 2,6 × 2,75 м**
   по 8 гостей, напольный маджлис, восьмигранные столики
9. **Фонтан-хауз и арык**
   хауз Ø1,2 м, арык 0,3 м ведёт от северного входа
10. **Северный вход · «Хивинские ворота»**
    ворота 4,1 м, Бухарский купол — витрина и лавка, пандус 1:12
11. **Зал север**
    ряды 4 + 2, центр под куполом свободен
12. **Бар**
    чай, самовар, кофе · 9 стульев
13. **Станция персонала**
    стеллажи, касса, вода, лёд, посуда
14. **Зал юг**
    ряд 4 + 2 + 4 и ряд 4 + 4
15. **Чинар под фонарём + столы у входа**
    дерево под навесом, зенитный фонарь 3 × 3 м; 4 стола у мангала
16. **Мангальная 3,3 × 5,8 м**
    тандыр · мангал · казан · раздача · вывеска SAMARKAND
17. **Фото-лаунж «Очаг»**
    драпировки, ковры, огонь-чаша, 3 столика, 12 пуфов
18. **Детская зона**
    у стекла зала — дети видны из зала; мягкое покрытие
19. **Уличные скамьи**
    литой бетон в стенке клумбы, майолика
20. **Фонтан-себиль**
    майоликовая стена, латунный носик, чаша
21. **Уличная фото-арка**
    ниша со скамьёй, подсветка, пальмы

ПОСАДКА

Столы у входа	12
Скамья у чинара (юг)	10
Зал юг	16
Фото-лаунж (пуфы)	12
Барная стойка	9
Айван: седир-кабинки (4 × 6)	24
Зал север + столы у фонтана	18
Тематические кабинки	32
Топчан	6
Шатры-маджлисы (2 × 8)	16
Итого мест в ресторане	**155**
+ уличные скамьи (вне счёта)	~31

Столы: на 2 — 7, на 4 — 8 (все делятся на модули 2-местные; столов на 6 нет), кабинки на 6 — 4

ЭРГОНОМИКА · норма / по плану

Главный проход / аллея	≥1500	**2500**
Проход к кабинкам	≥1200	**1348**
Проход топчан ↔ фонтан	≥900	**932**
Проход на айване	≥1200	**1400**
Модуль стола: на 1 гостя / глубина	600–700 / 750–800	**700 / 800**
Край стола → спинка кресла	450–600	**525**
Спинка–спинка (без прохода)	≥450	**600**
Кресло 580: зазор между подлокотниками	≥100	**120**
Барная стойка: высота / вынос	1050 / 250–300	**1050 / 300**
Шаг барных стульев	600–650	**620**
Рабочая зона повара	≥1200	**2450**
Раздача → гости	≥1500	**1570**
Пандус: уклон / ширина	1:12 / ≥1200	**1:12 / 1300**
Топчан: высота / на 1 гостя	400–450 / ≥600	**450 / 700**
Служебный проход (в свету у колонн)	≥1200	**1275**
Сиденье / стол / подлокотник	450–500 / 740–760	**500 / 760 / 660**

ОБОЗНАЧЕНИЯ

- Колонна навеса (сталь, обшивка деревом)
- Ось здания
- Маршрут персонала
- Дверь зала закрыта
- Размер, мм
- Зенитный фонарь над чинаром
- Балка навеса
- Вход гостей
- Дверь зала открыта
- Вытяжной зонт
- № стола
- Стык модулей стола

· Основа: исполнительный DWG (Long House, 10.07.2024) 1:1. Отметки: тротуар −1.170, терраса −0.450, айван и зал ±0.000.

· Навес: стальные балки по осям, сэндвич-панель 50 мм, уклон 5% к улице, желоб вдоль улицы; низ плиты балкона +3.850, волна-ламели демонтируются.

· Купол в кровле один — центральный Ø5,6 (карбанди, остеклённый фонарь). Чинар у бара остаётся под навесом: крона формуется на высоте 2,2–3,0 м, над ним зенитный фонарь 3,0 × 3,0 м с резной решёткой-панджарой. Северный чинар удаляется.

· Все отдельно стоящие столы — модули 700 × 800: пары разъединяются на 2-местные или сдвигаются в столы на 6–8 (ряды выровнены).

· Двери: C–D южная открыта; C–D северная и D–E южная закрыты (банкетка); D–E северная и E–F у лифта открыты.

ОЗЕЛЕНЕНИЕ

- **Гранат (анор) — символ Самарканда**
  у входа в клумбе и в кадке у бара
- **Плюмерия (франжипани)**
  в уличной клумбе, аромат вечером
- **Бугенвиллия и жасмин самбак**
  по спинкам уличных скамей
- **Пальма арека**
  кадки в фото-лаунже
- **Банан, стрелиция Николая**
  зелёная рамка Хивинских ворот
- **Райхон, мята, базилик**
  грядка у мангальной — к столу
- **Лотос, кувшинка**
  в хаузе
- **Чинар у бара (существующий)**
  под зенитным фонарём, формовка кроны, подсветка снизу

Масштаб 1:100 · A2

0 — 5 м

МАНГАЛЬНАЯ · 1:100

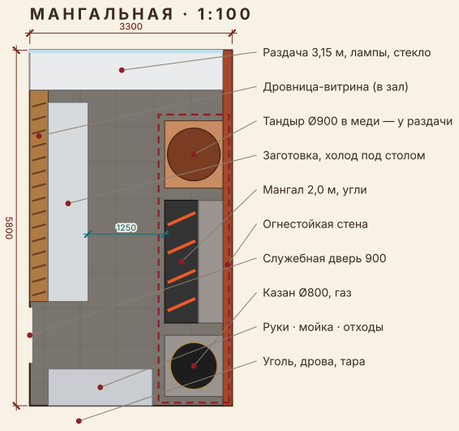

ШАТЁР-МАДЖЛИС (×2) · 1:75

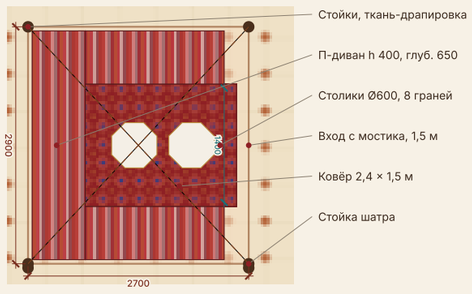

АЙВАН: СЕДИР-КАБИНКИ · 1:75

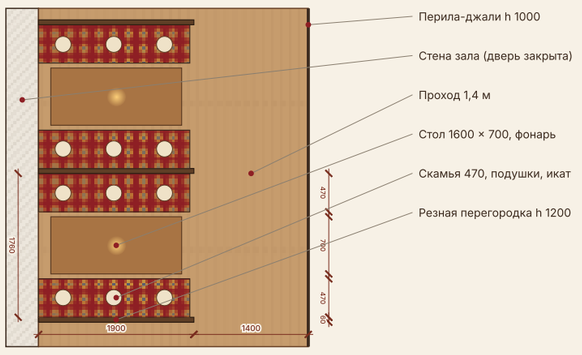

СТОЛЫ-МОДУЛИ · 1:100

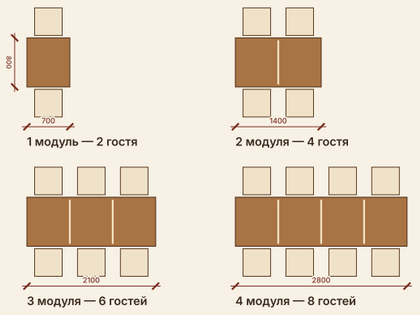

Столешница 700 × 800, h 760, вставка-зеллидж; стык на скрытых стяжках

Концепция для согласования с заказчиком · размеры уточнить на месте