
# SAMARKAND

## Крытая терраса · планировка R10

Таджикская и узбекская кухня · Võ Nguyên Giáp, 254, Дананг

R10

2026-10-27

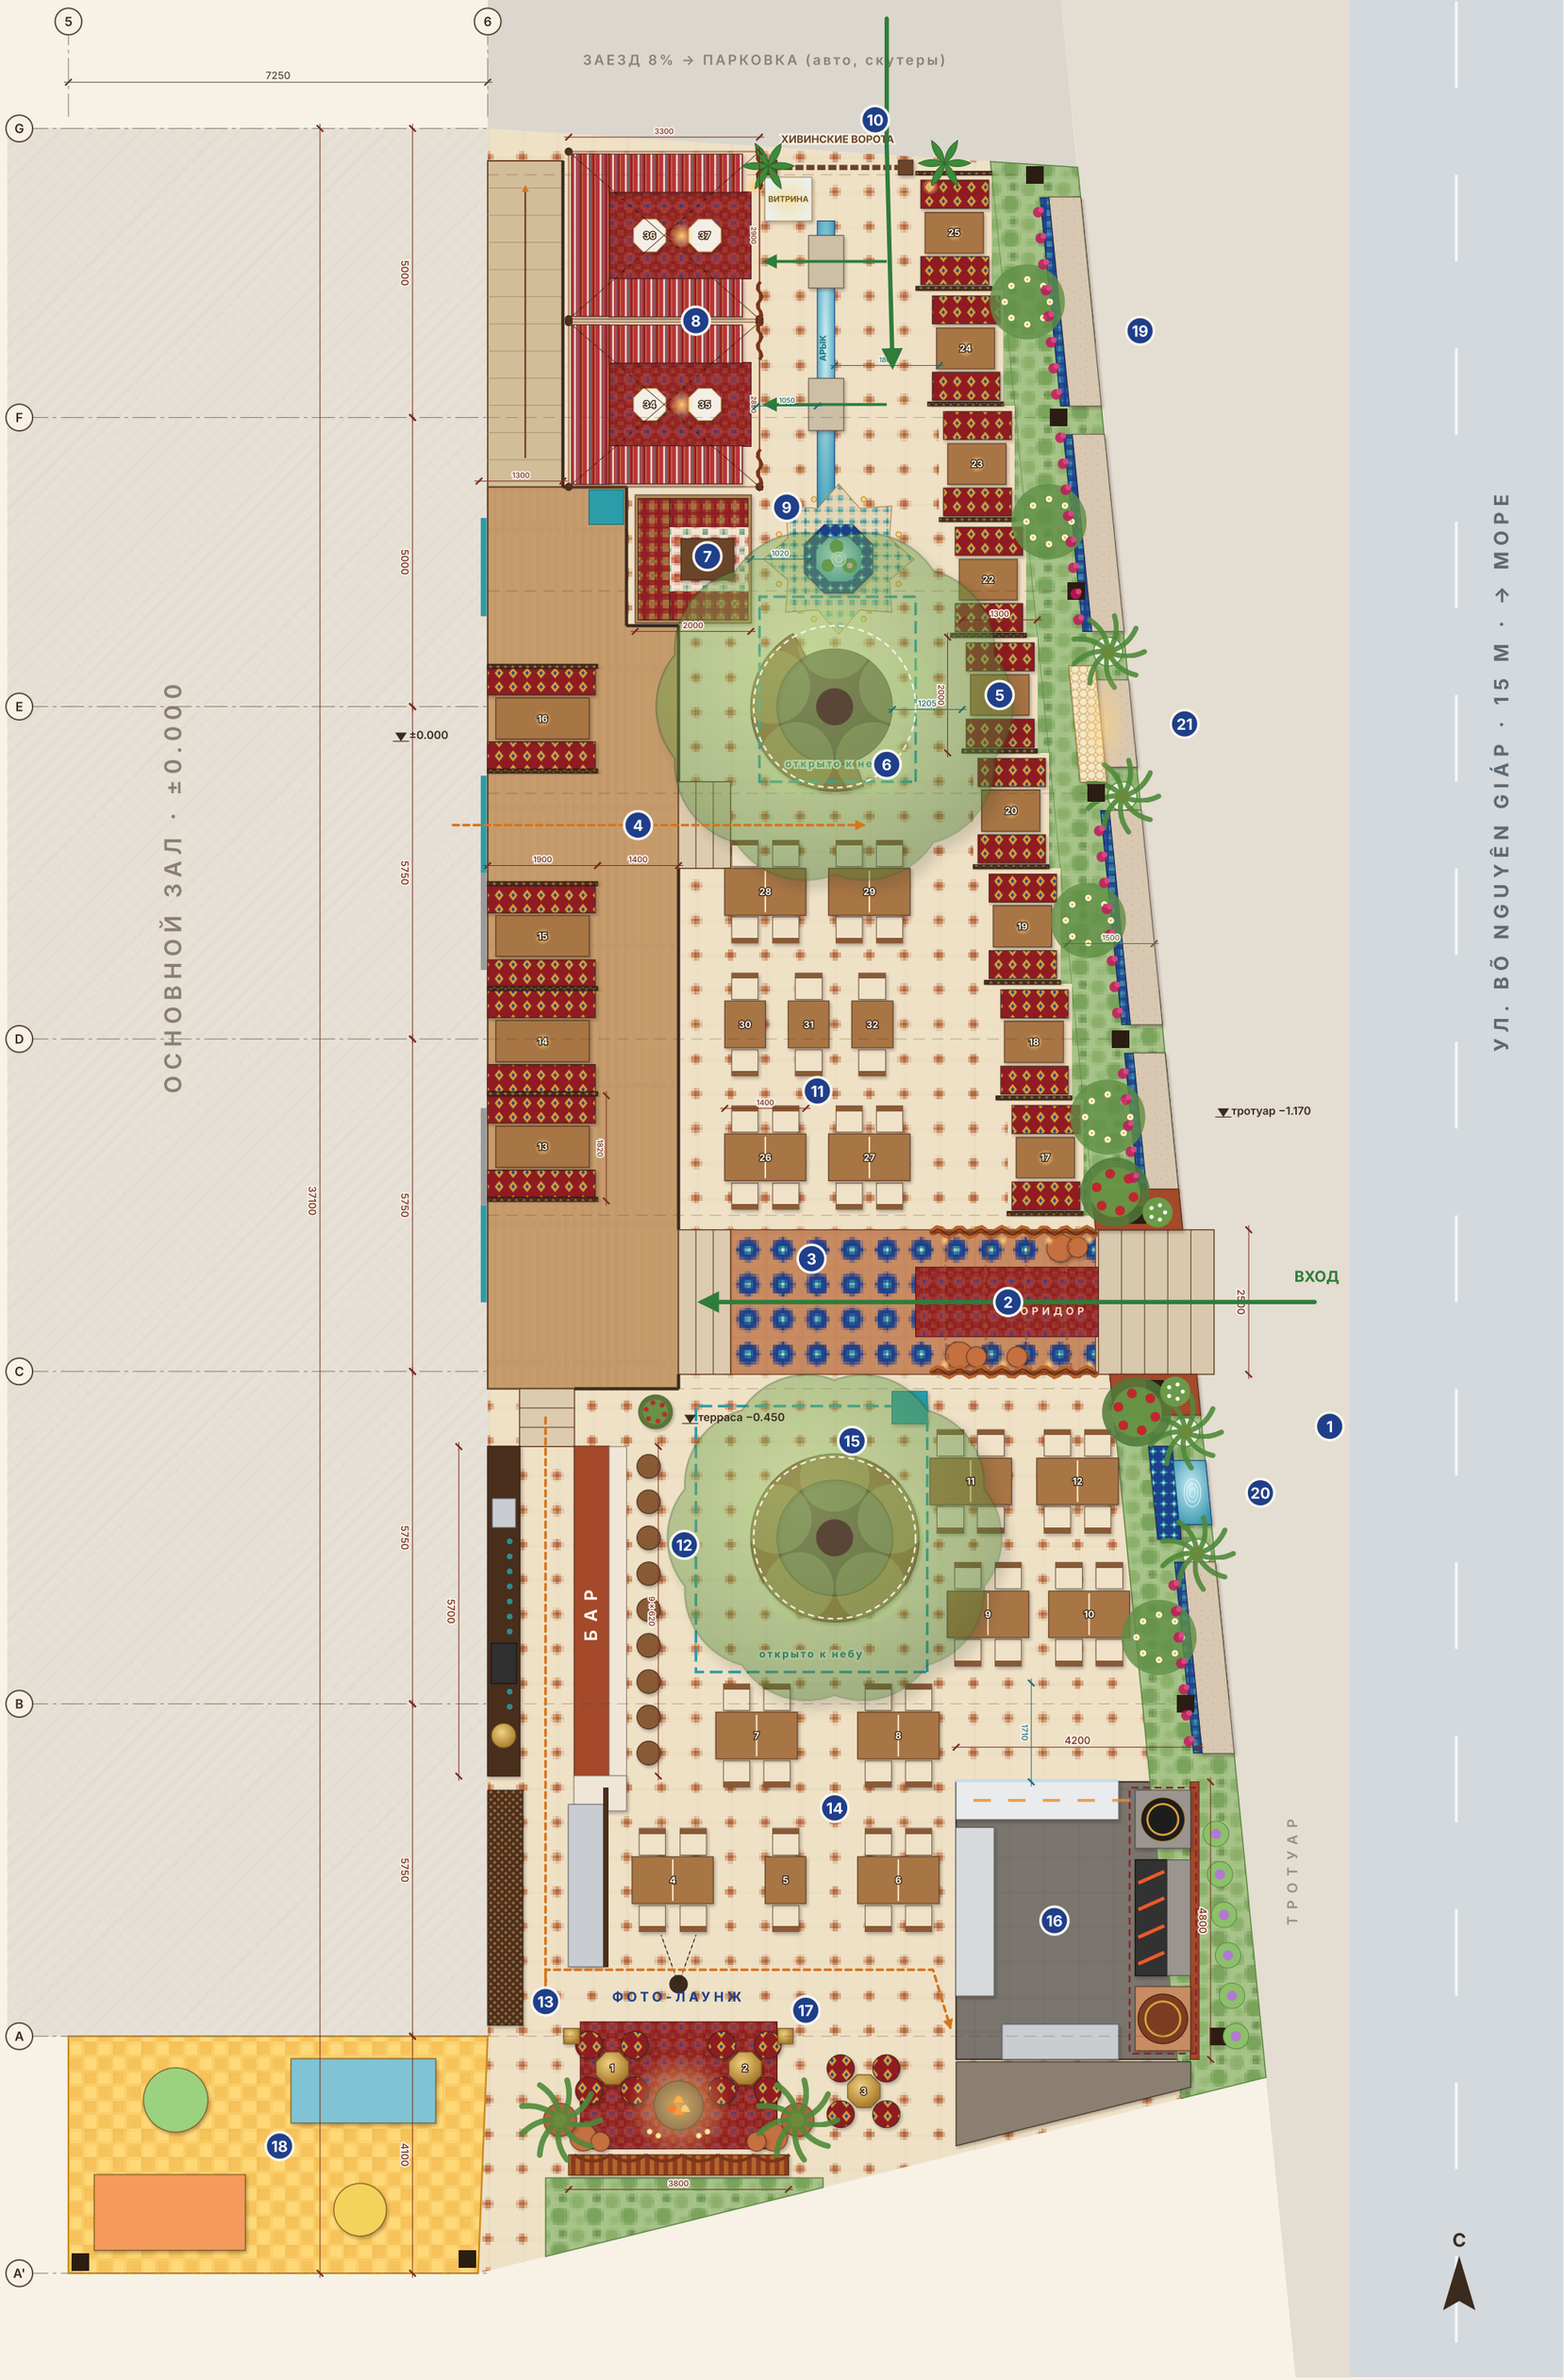


## ЗОНЫ

1. **Главный вход · портал-пештак** — проём 2,5 м, 4 ступени с тротуара
2. **Коридор-драпировка** — бархат, ковровая дорожка, хумы, фонари
3. **Аллея к залу** — гирих, 2,5 м, хостес у выхода
4. **Айван-платформа ±0.000** — 4 седир-кабинки на 6 у стены, проход 1,4 м
5. **Кабинки вдоль улицы** — 9 кабинок на 4, резные ширмы, фонари
6. **Чинар-дворик (север)** — открыт к небу, скамья-полукольцо
7. **Топчан 2,0 × 2,2 м** — 6 гостей, курпачи с 3 сторон, у фонтана
8. **Два шатра-маджлиса 3,2 × 2,8 м** — по 8 гостей, вход по мостику через арык
9. **Фонтан-хауз и арык** — хауз Ø1,2 м, арык 0,3 м ведёт от северного входа
10. **Северный вход · «Хивинские ворота»** — резные ворота, витрина-музей, пандус 1:12
11. **Зал север** — ряды по 4 + средний ряд из 3 столов на 2
12. **Бар** — чай, самовар, кофе · 9 стульев
13. **Станция персонала** — стеллажи, касса, вода, лёд, посуда
14. **Зал юг** — ряд 4 + 2 + 4 и ряд 4 + 4
15. **Чинар-дворик (юг) + столы у входа** — открыт к небу; 4 стола напротив мангала
16. **Мангальная 4,2 × 4,8 м** — тандыр · мангал · казан · раздача к гостям
17. **Фото-лаунж «Очаг»** — драпировки, ковры, огонь-чаша, 3 столика, 12 пуфов
18. **Детская зона** — ограждение, мягкое покрытие
19. **Уличные скамьи** — литой бетон в стенке клумбы, майолика
20. **Фонтан-себиль** — майоликовая стена, латунный носик, чаша
21. **Уличная фото-арка** — ниша со скамьёй, подсветка, пальмы

## ПОСАДКА

| | |
|---|---|
| Столы у входа | 16 |
| Скамья у чинара (юг) | 10 |
| Зал юг | 18 |
| Фото-лаунж (пуфы) | 12 |
| Барная стойка | 9 |
| Айван: седир-кабинки (4 × 6) | 24 |
| Зал север | 22 |
| Скамья у чинара (север) | 6 |
| Кабинки | 36 |
| Топчан | 6 |
| Шатры-маджлисы (2 × 8) | 16 |
| **Итого мест в ресторане** | **175** |
| + уличные скамьи (вне счёта) | ~35 |

**Столы: на 2 — 4, на 4 — 12 (каждый делится на 2 × 2), кабинки на 6 — 4**

## ЭРГОНОМИКА · норма / по плану

| | | |
|---|---|---|
| Главный проход / аллея | ≥1500 | **2500** |
| Проход к кабинкам | ≥1200 | **1205** |
| Проход топчан ↔ фонтан | ≥900 | **932** |
| Проход на айване | ≥1200 | **1400** |
| Модуль стола: на 1 гостя / глубина | 600–700 / 750–800 | **700 / 800** |
| Край стола → спинка стула | 450–600 | **490** |
| Спинка–спинка (без прохода) | ≥450 | **520** |
| Барная стойка: высота / вынос | 1050 / 250–300 | **1050 / 300** |
| Шаг барных стульев | 600–650 | **620** |
| Рабочая зона повара | ≥1200 | **2450** |
| Раздача → гости | ≥1500 | **2010** |
| Пандус: уклон / ширина | 1:12 / ≥1200 | **1:12 / 1300** |
| Топчан: высота / на 1 гостя | 400–450 / ≥600 | **450 / 700** |

## ОБОЗНАЧЕНИЯ

- Колонна навеса (сталь, обшивка деревом)
- Ось здания
- Маршрут персонала
- Дверь зала закрыта
- Размер, мм
- Проём в кровле — открыто к небу
- Балка навеса
- Вход гостей
- Дверь зала открыта
- Вытяжной зонт
- № стола
- Стык модулей стола

· Основа: исполнительный DWG (Long House, 10.07.2024) 1:1. Отметки: тротуар −1.170, терраса −0.450, айван и зал ±0.000.

· Навес: стальные балки по осям, сэндвич-панель 50 мм, уклон 5% к улице, желоб вдоль улицы; низ плиты балкона +3.850, волна-ламели демонтируются.

· Над чинарами — открытые дворики (проём в кровле с желобом по периметру): юг 4,0 × 4,6 м, север 2,7 × 3,2 м. Под ними только всепогодные скамьи.

· Все отдельно стоящие столы — модули 700 × 800: пары разъединяются на 2-местные или сдвигаются в столы на 6–8 (ряды выровнены).

· Двери: C–D южная открыта; C–D северная и D–E южная закрыты (банкетка); D–E северная и E–F у лифта открыты.


## ОЗЕЛЕНЕНИЕ

- **Гранат (анор) — символ Самарканда** — у входа в клумбе и в кадке у бара
- **Плюмерия (франжипани)** — в уличной клумбе, аромат вечером
- **Бугенвиллия** — по спинкам скамей и колоннам
- **Жасмин самбак** — у портала входа
- **Пальма арека** — кадки в фото-лаунже
- **Банан, стрелиция Николая** — зелёная рамка Хивинских ворот
- **Райхон, мята, базилик** — грядка у мангальной — к столу
- **Лотос, кувшинка** — в хаузе
- **Чинары (существующие)** — открытые дворики, подсветка снизу


Масштаб 1:100 · А2

0 — 5 м


### МАНГАЛЬНАЯ · 1:75

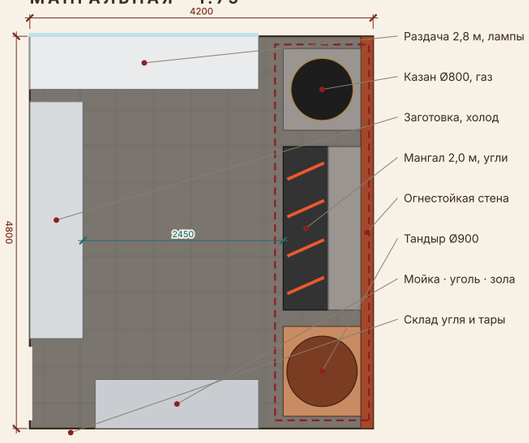



### ШАТЁР-МАДЖЛИС (×2) · 1:75

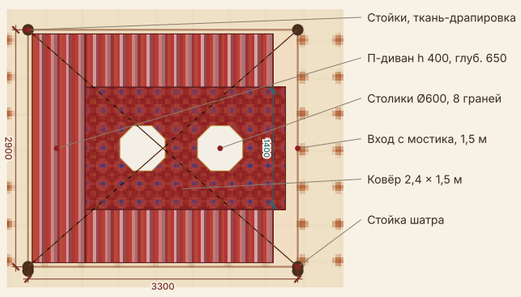


### АЙВАН: СЕДИР-КАБИНКИ · 1:75

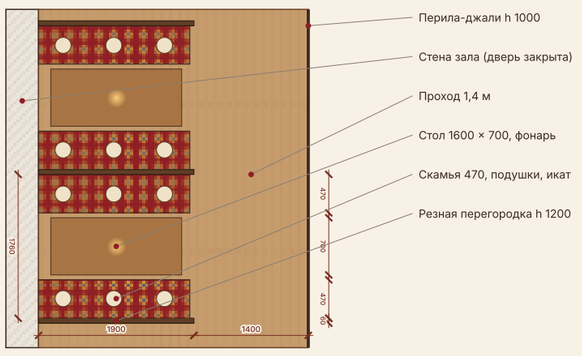


### СТОЛЫ-МОДУЛИ · 1:100

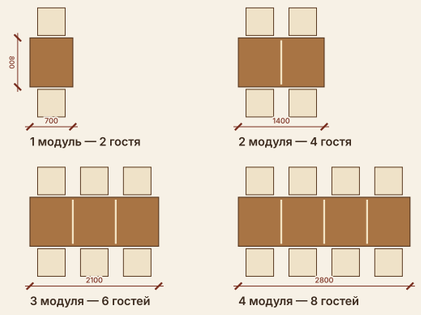


Столешница 700 × 800, h 750; стык на скрытых стяжках



Концепция для согласования с заказчиком · размеры уточнить на месте