SAMARKAND


Terrace roof · concept

Roof plan 1:200 · sections 1:100


R10

2026-10-27


ROOF PLAN · 1:200

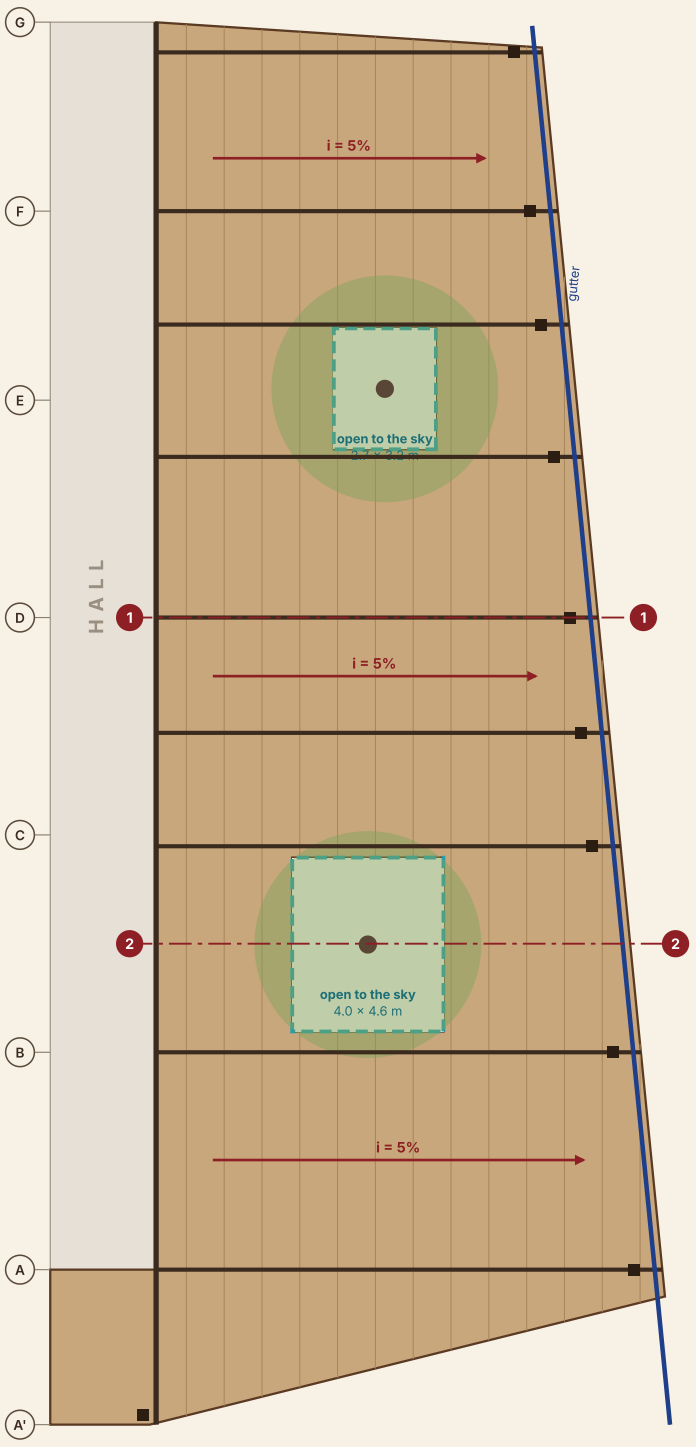

SECTION 1–1 (on axis D) · 1:100

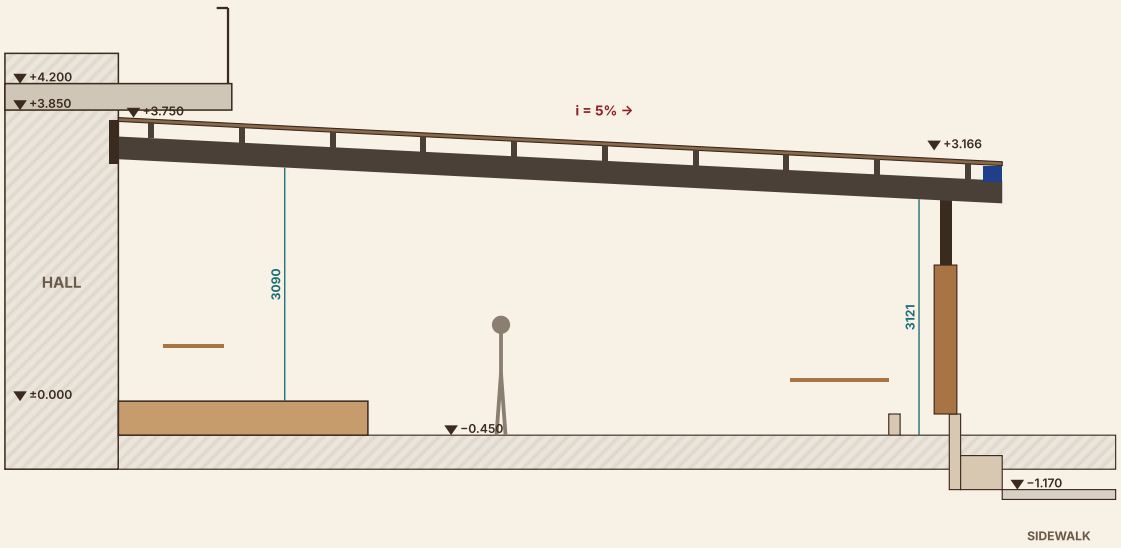

SECTION 2–2 (through the south chinar court) · 1:100

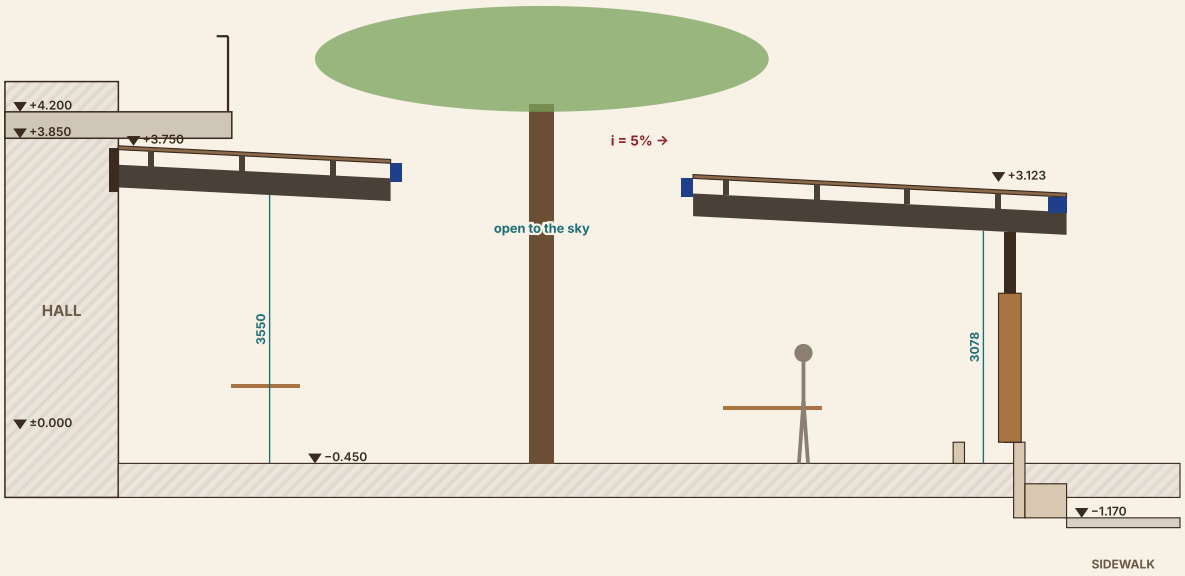

SOLUTION

- Beams: galvanised steel, dark-bronze powder coat, on the column lines at 3.0–5.75 m
- Façade bearing: steel ledger on anchors under the balcony slab (soffit +3.850)
- Street bearing: 9 columns 150×150 in the planter wall, wood-clad; cap +2.9
- C200 purlins at 1.2 m; 50 mm PU sandwich panel with a wood-look underside
- 5% fall to the street; box gutter along the street, downpipes inside the columns → planter drain
- Chinar courts: trimmed opening with a perimeter gutter, downpipe into the tree pit
- Timber slat ceiling only over the bar and the corridor (accent)
- Wave louvers under the balcony removed; the F2 façade stays open
- Typhoon: wind zone II, uplift anchorage; structural engineer to calculate

QUANTITIES

Roof area	**419.5 m²**
Open courts	**27.0 m²**
Beams (lin. m)	**105.2 m**
Purlins (lin. m)	**377.6 m**
Columns	**11 pcs**
Gutter street / courts	**37.2 / 29.0 m**