SAMARKAND


R10

Навес · концепция кровли


2026-10-27

План кровли 1:200 · разрезы 1:100


ПЛАН КРОВЛИ · 1:200

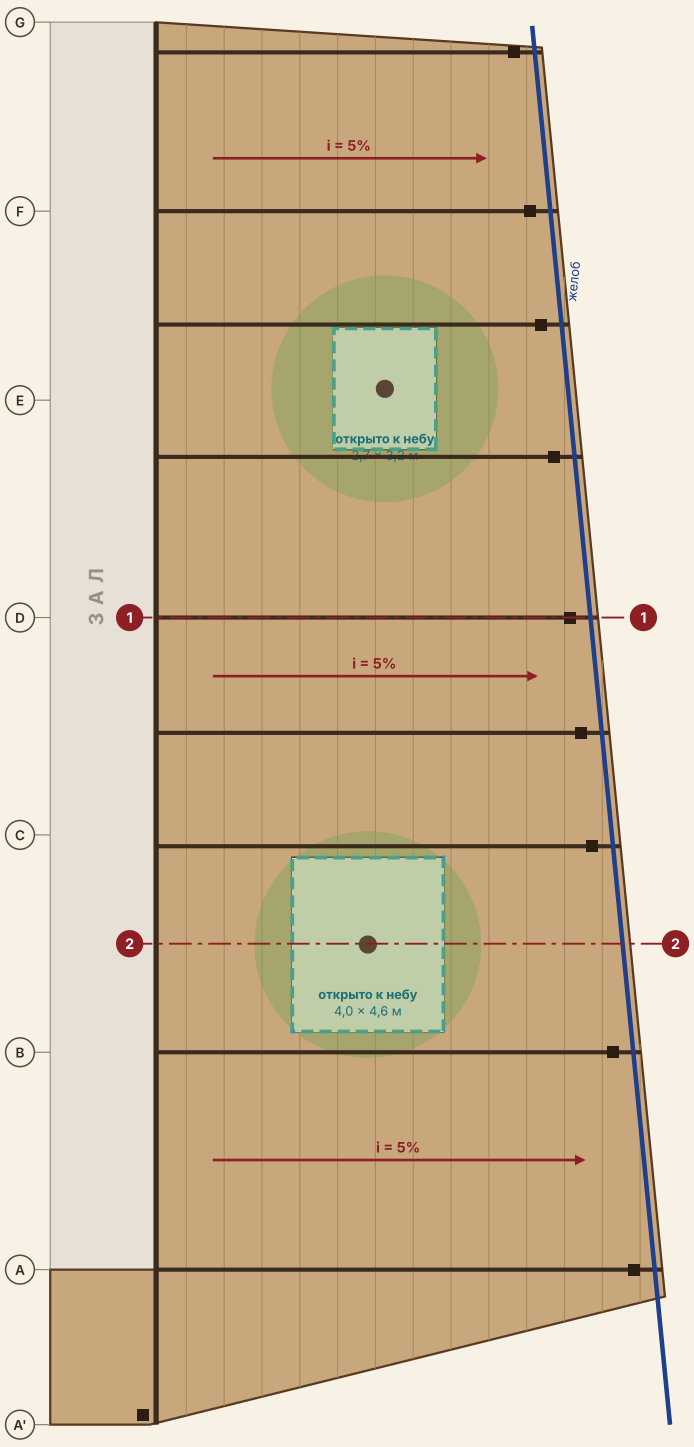

РАЗРЕЗ 1–1 (по оси D) · 1:100

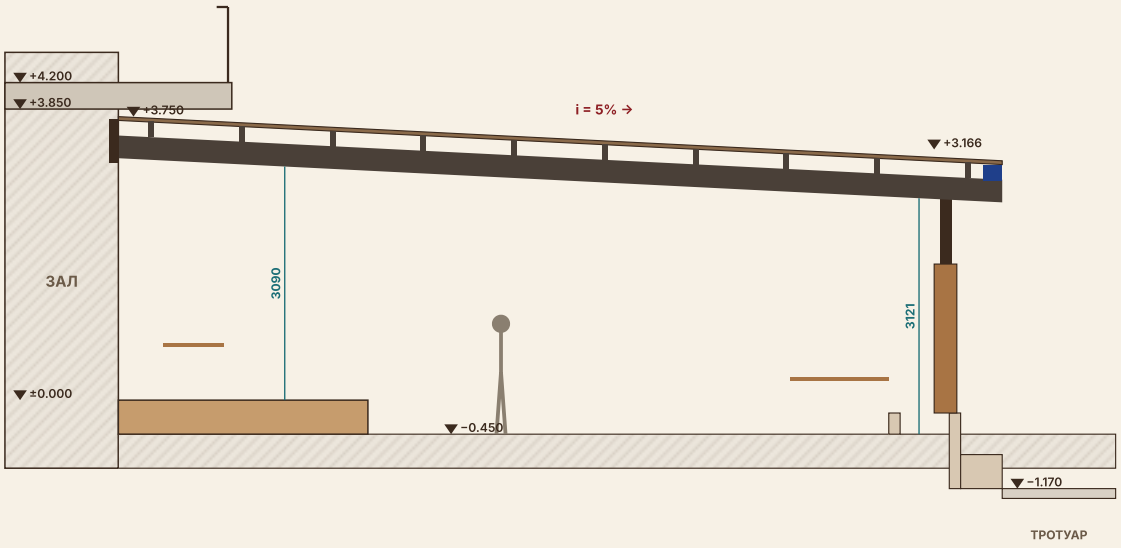

РАЗРЕЗ 2–2 (через южный чинар-дворик) · 1:100

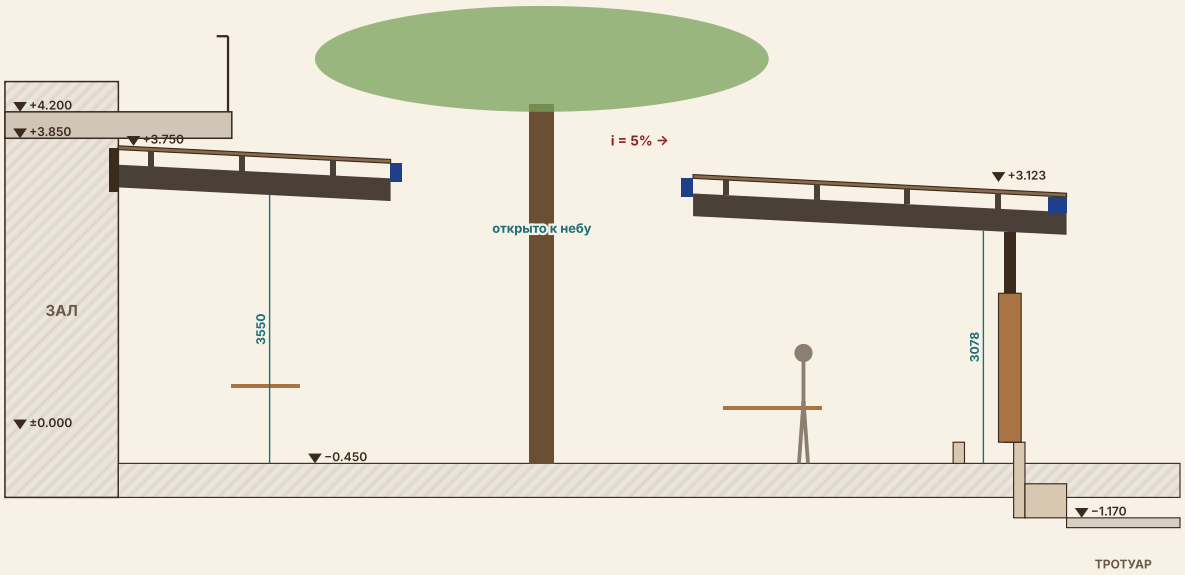

РЕШЕНИЕ

- Балки: сталь, оцинковка + порошковая краска «тёмная бронза», по линиям колонн, шаг 3,0–5,75 м
- Опора у фасада: опорный уголок/швеллер на анкерах под плитой балкона (низ плиты +3.850)
- Опора у улицы: 9 колонн 150×150 в стенке клумбы, обшивка деревом; оголовок +2.9
- Прогоны С200 шаг 1,2 м; сэндвич-панель PU 50 мм с нижним слоем «под дерево»
- Уклон 5% к улице; коробчатый желоб вдоль улицы, водостоки внутри колонн → дренаж клумб
- Дворики у чинаров: проём с обвязкой и желобом по периметру, водосток в приствольную яму
- Деревянная реечная подшивка — только над баром и коридором (акцент)
- Волна-ламели под балконом демонтируются; фасад 2-го этажа остаётся открытым
- Тайфун: ветровой район II, анкеровка на отрыв; расчёт — инженер-конструктор

ОБЪЁМЫ

Площадь кровли	**419.5 м²**
Открытые дворики	**27.0 м²**
Балки (пог. м)	**105.2 м**
Прогоны (пог. м)	**377.6 м**
Колонны	**11 шт**
Желоб улица / дворики	**37.2 / 29.0 м**

С