SAMARKAND

Covered terrace · Layout R7

Tajik & Uzbek national cuisine · 254 Võ Nguyên Giáp, Đà Nẵng

R6

2026-10-26

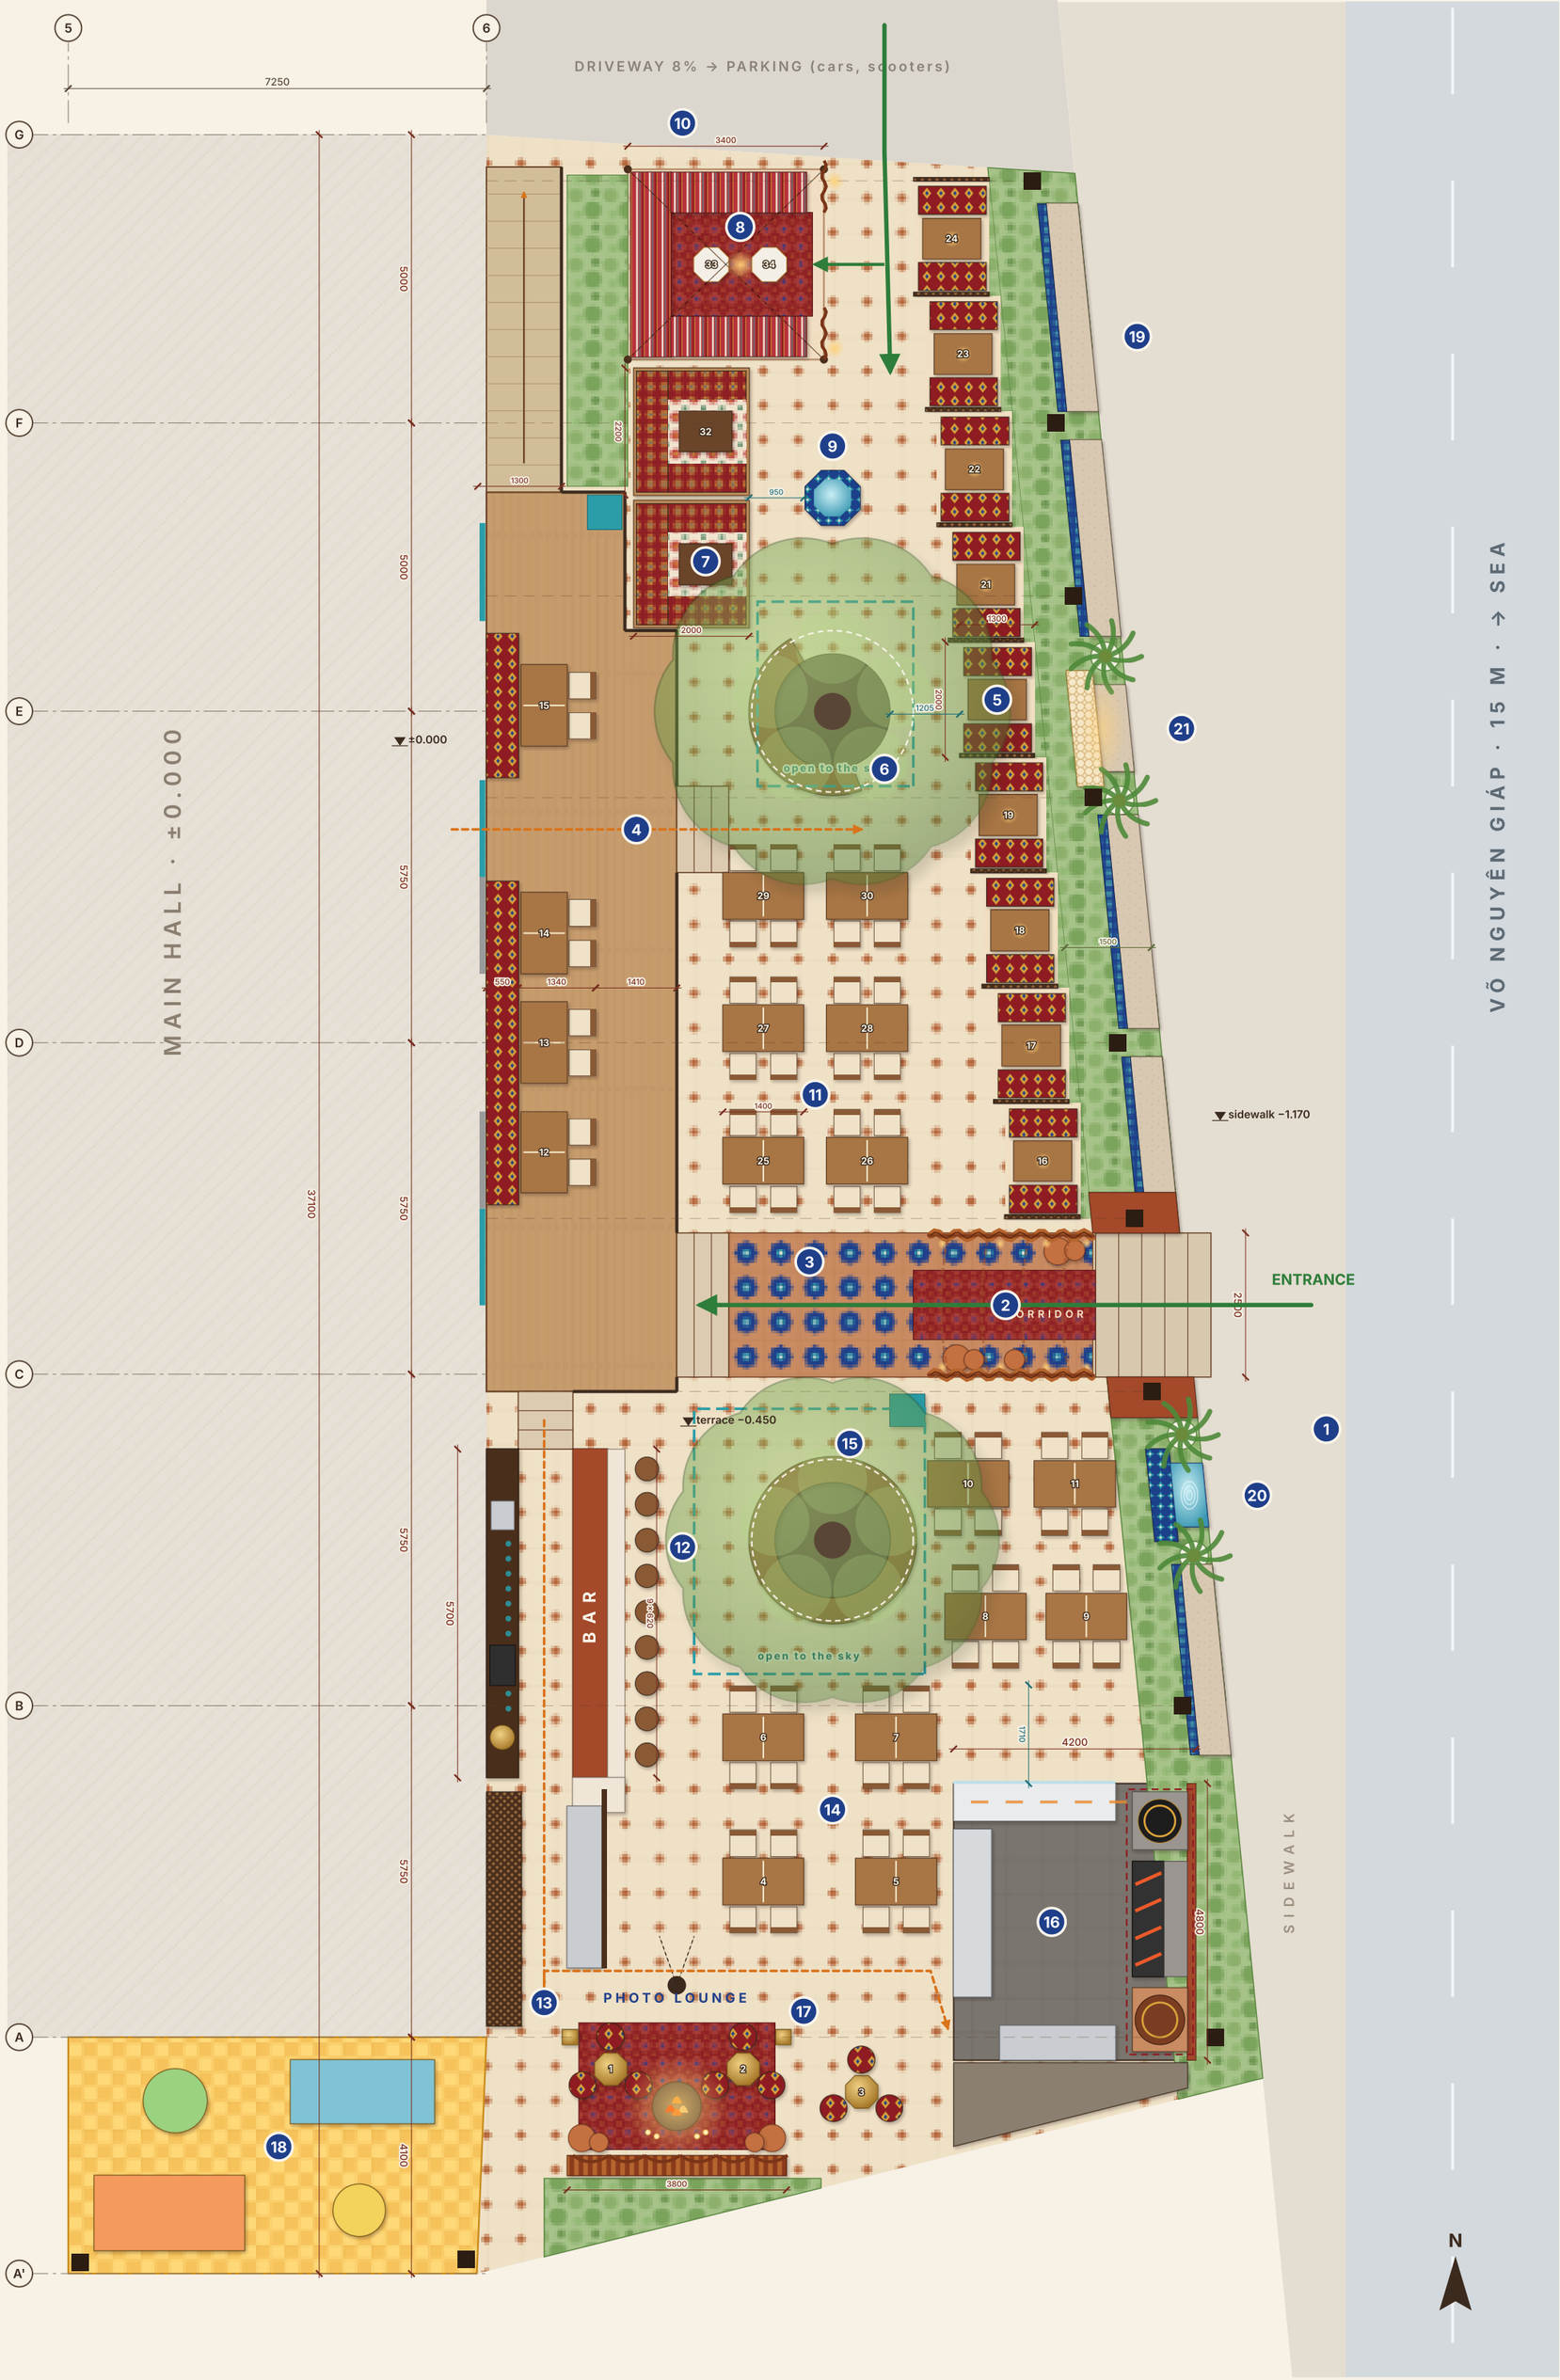

Scale 1:100 · A2

ZONES

1. **Street entrance · pishtaq portal** — 2.5 m opening, 4 steps from the sidewalk
2. **Draped corridor** — velvet swags, runner, clay jars, lanterns
3. **Alley to the hall** — girih paving, 2.5 m, host at the exit
4. **Aivan platform ±0.000** — banquette + 4 modular tables, 1.4 m aisle
5. **Booths along the street** — 9 booths for 4, carved screens, lanterns
6. **Chinar court north** — open to the sky, half-ring bench
7. **Tapchans 2.0 × 2.2 m** — 6 guests each, kurpacha on 3 sides, entered from the path
8. **Majlis tent** — entered from the east (1.8 m), U-sofa, 10 guests
9. **Hauz fountain** — in front of the tapchans, seen from the entrance and booths
10. **North entrance + ramp 1:12** — from parking, step-free
11. **Dining north** — 6 tables for 4 (12 modules)
12. **Bar** — tea, samovar, coffee · 9 stools
13. **Staff station** — shelving, POS, water, ice, dishes
14. **Dining south** — 4 tables for 4 (8 modules)
15. **Chinar court south + entrance tables** — open to the sky; 4 tables facing the mangal
16. **Mangal kitchen 4.2 × 4.8 m** — tandoor · mangal · kazan · pass to guests
17. **Photo lounge "Ochag"** — drapes, carpets, fire bowl, low tables
18. **Kids zone** — fenced, soft floor
19. **Street benches** — cast concrete in the planter wall, majolica
20. **Sebil fountain** — majolica wall, brass spout, basin
21. **Street photo arch** — bench niche, uplight, palms

SEATS

Entrance tables	16
Chinar bench south	10
Dining south	16
Photo lounge (poufs)	9
Bar counter	9
Aivan platform	16
Dining north	24
Chinar bench north	6
Booths	36
Tapchans (2 × 6)	12
Majlis tent	10
Total restaurant seats	**164**
+ street benches (not counted)	~35

700 × 800 table modules: 36 in total

ERGONOMICS · standard / as planned

Main path / alley	≥1500	2500
Path to the booths	≥1200	1205
Path tapchan ↔ fountain	≥900	977
Aivan aisle	≥1200	1410
Table module: per guest / depth	600–700 / 750–800	700 / 800
Table edge → chair back	450–600	490
Chair back to back (no path)	≥450	512
Bar counter: height / overhang	1050 / 250–300	1050 / 300
Bar stool pitch	600–650	620
Cook work aisle	≥1200	2450
Pass → guests	≥1500	2010
Ramp: slope / width	1:12 / ≥1200	1:12 / 1300
Tapchan: height / per guest	400–450 / ≥600	450 / 700

KEY

- Roof column (steel, wood-clad)
- Building axis
- Staff route
- Hall door, closed
- Dimension, mm
- Roof opening, open to the sky
- Roof beam
- Guest entrance
- Hall door, open
- Exhaust hood
- Table no.
- Table module joint

· Base: as-built DWG (Long House, 10-07-2024) 1:1. Levels: sidewalk −1.170, terrace −0.450, aivan and hall ±0.000.

· Roof: steel beams on the grid, 50 mm sandwich panel, 5% fall to the street, gutter along the street; balcony soffit +3.850, wave louvers removed.

· Over the chinars, courts open to the sky (roof opening with a perimeter gutter): south 4.0 × 4.6 m, north 2.7 × 3.2 m. Only all-weather benches below.

· Every loose table is a 700 × 800 module: pairs split into 2-tops or push together into tables for 6–8 (rows are aligned).

· Doors: C–D south open; C–D north and D–E south closed (banquette); D–E north and E–F by the lift open.

MANGAL KITCHEN · 1:75

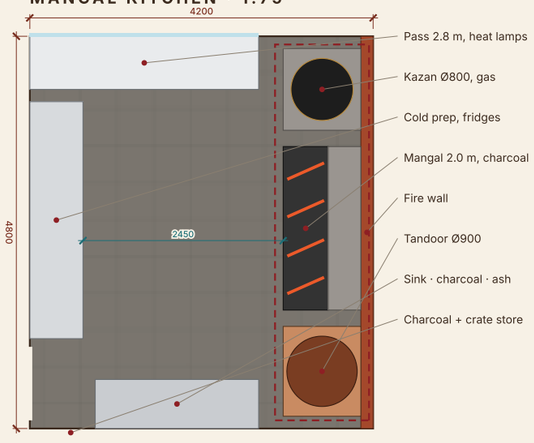

MAJLIS TENT · 1:75

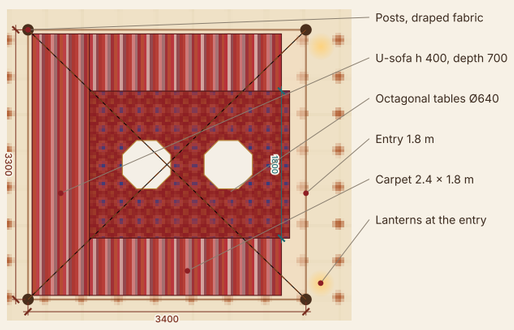

STREET BENCH · SECTION 1:60

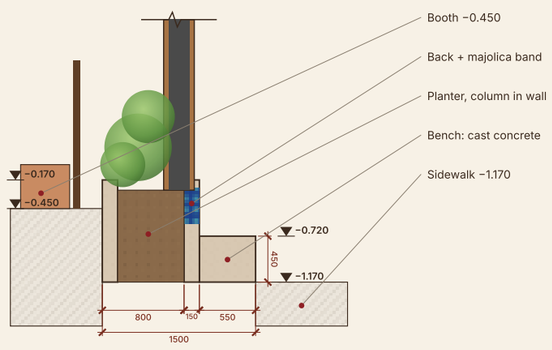

TABLE MODULES · 1:100

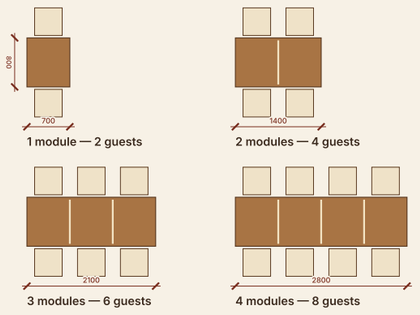

Top 700 × 800, h 750; joined with hidden clamps

Concept for client review · dimensions to verify on site

designed by Nomad Group