SAMARKAND

Covered terrace · Layout R12 · rev. 7

Tajik & Uzbek national cuisine · 254 Võ Nguyên Giáp, Đà Nẵng

R12

2026-10-28

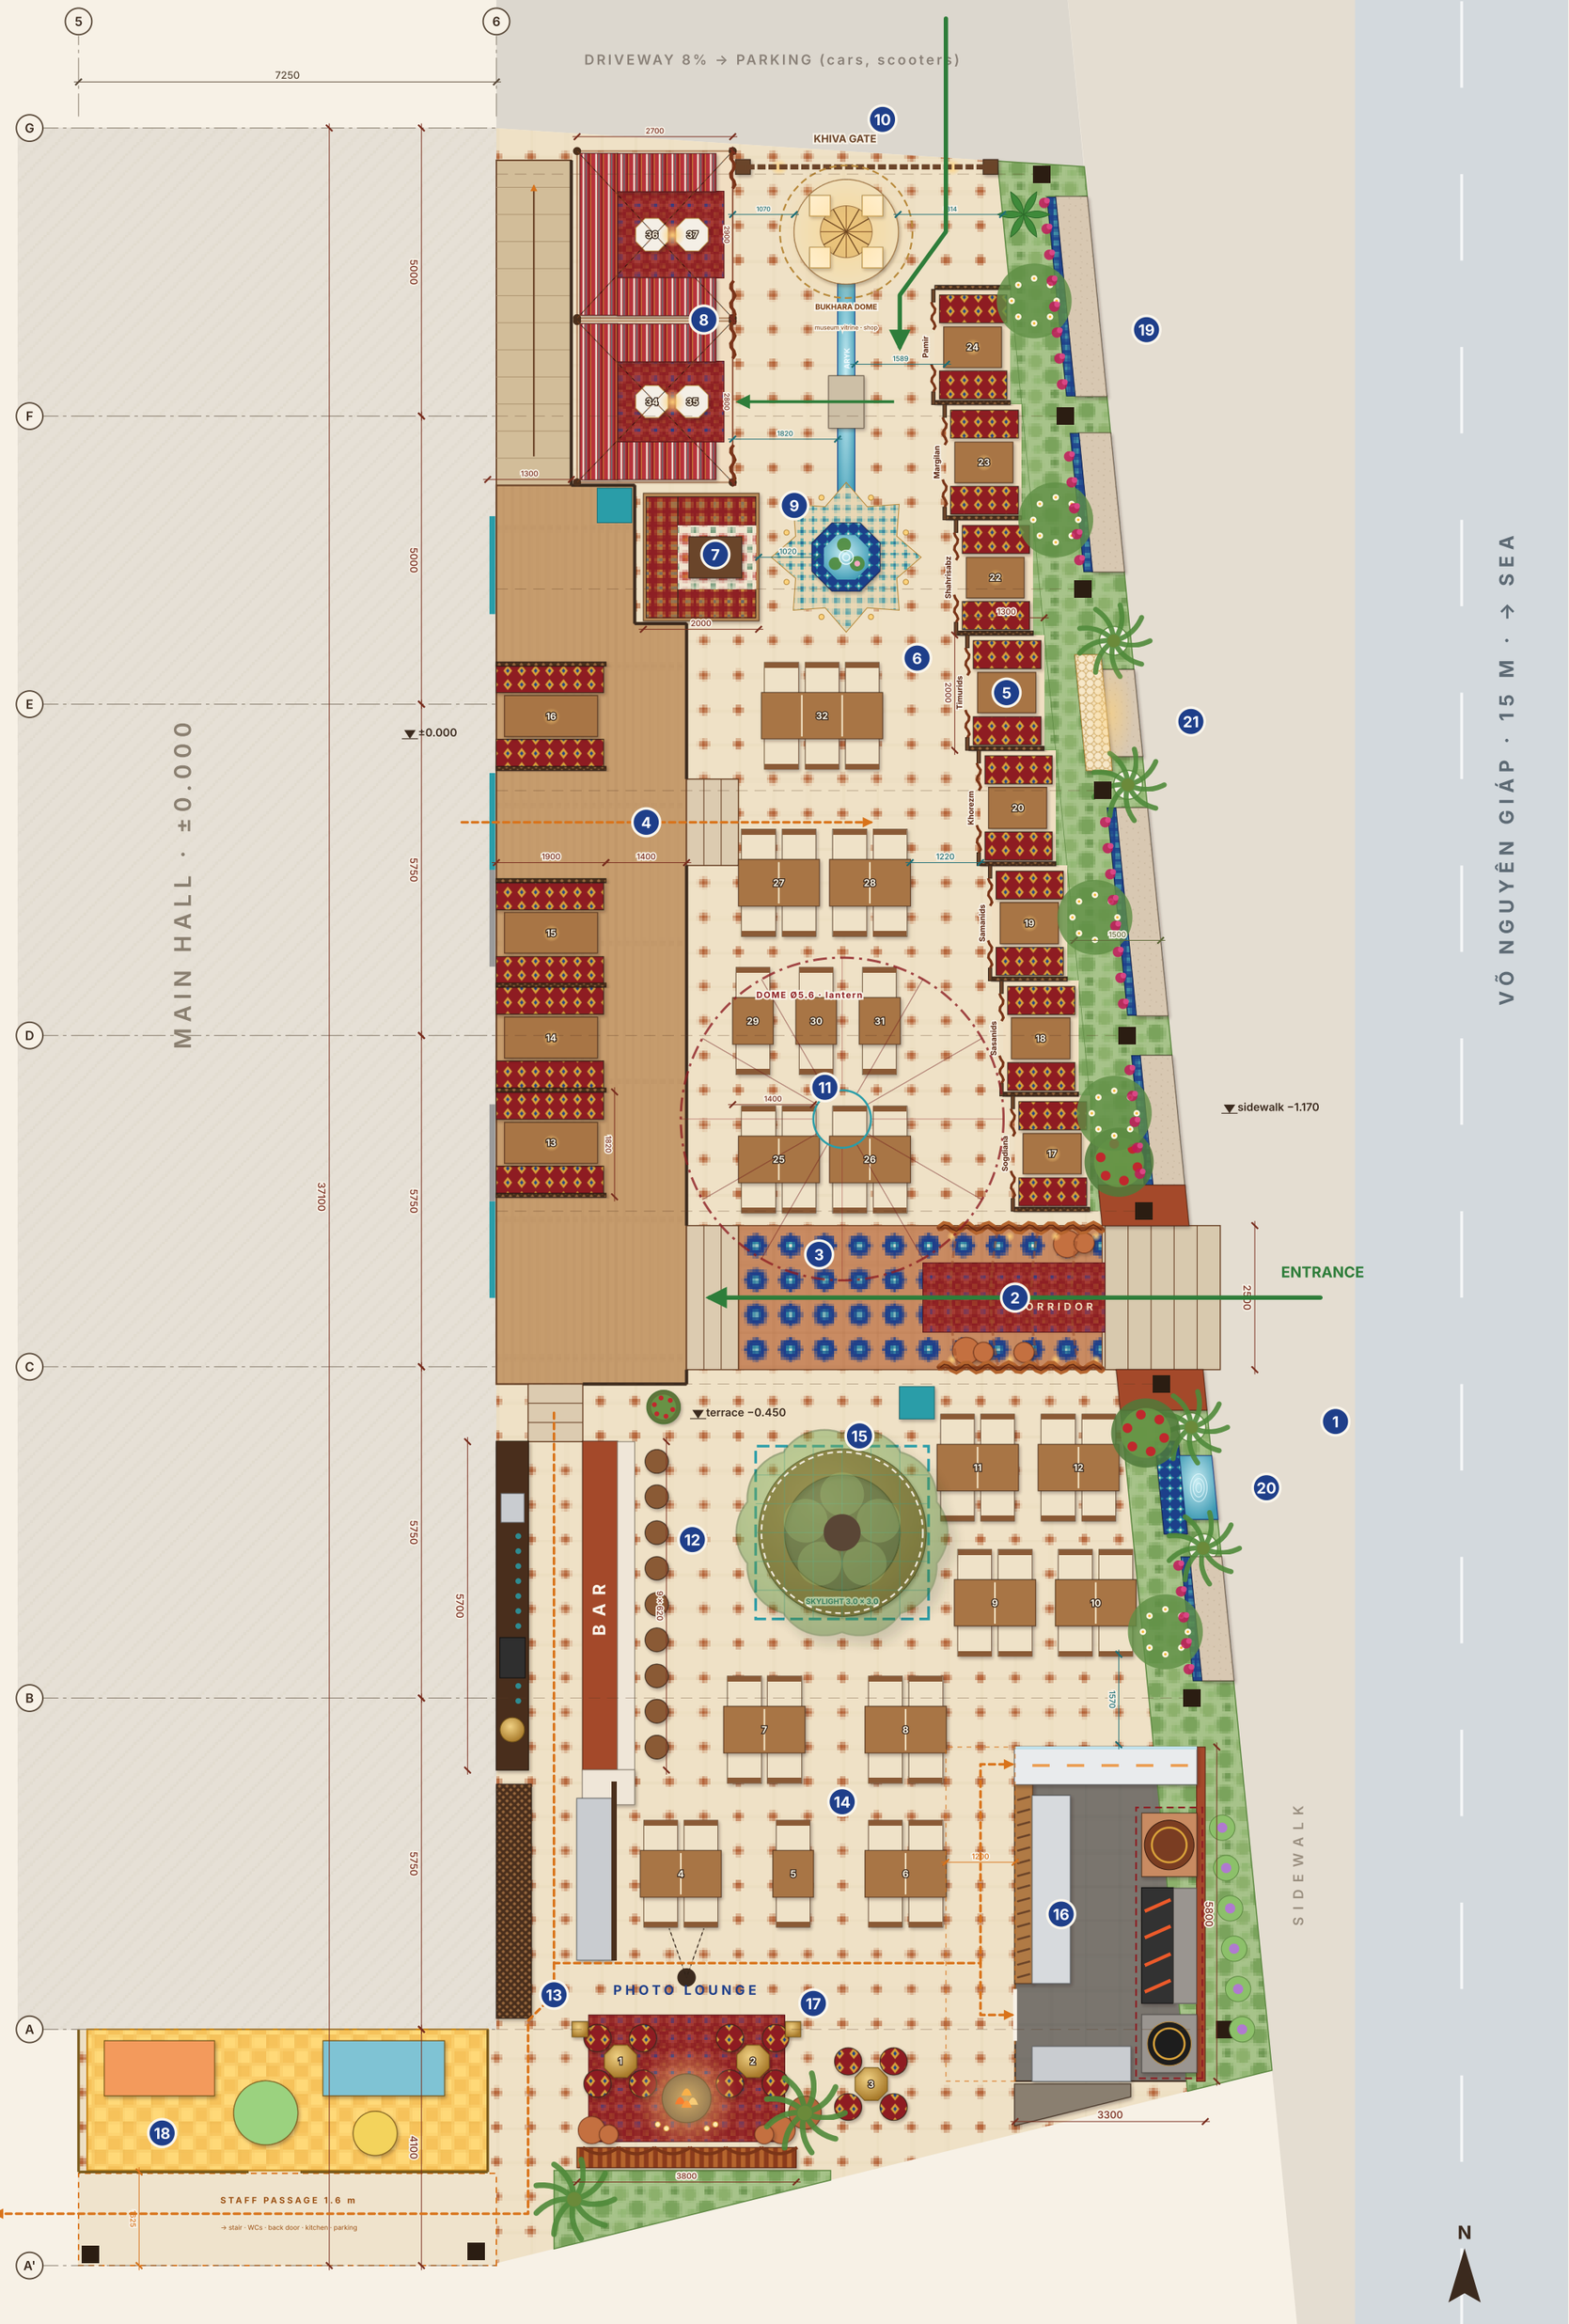

ZONES

1. **Street entrance · pishtaq portal** — 2.5 m opening, 4 steps from the sidewalk
2. **Draped corridor** — velvet swags, runner, clay jars, lanterns
3. **Alley to the hall** — girih paving, 2.5 m, host at the exit
4. **Aivan platform ±0.000** — 4 sedir booths for 6 on the wall, 1.4 m aisle
5. **Themed booths** — 8 closed rooms: epochs and cities, curtained portals
6. **Family table for 6** — by the fountain, where the north chinar stood
7. **Tapchan 2.0 × 2.2 m** — 6 guests, kurpacha on 3 sides, by the fountain
8. **Two majlis tents 2.6 × 2.75 m** — 8 guests each, entered over a bridge across the aryk
9. **Hauz fountain and aryk** — hauz Ø1.2 m, 0.3 m aryk leads from the north entrance
10. **North entrance · "Khiva gate"** — 4.1 m gate, Bukhara dome — vitrine and shop, ramp 1:12
11. **Dining north** — rows of 4-tops + a middle row of three 2-tops
12. **Bar** — tea, samovar, coffee · 9 stools
13. **Staff station** — shelving, POS, water, ice, dishes
14. **Dining south** — row 4 + 2 + 4 and row 4 + 4
15. **Chinar under the lantern + entrance tables** — tree under the roof, 3 × 3 m skylight; 4 tables by the mangal
16. **Mangal kitchen 3.3 × 5.8 m** — tandoor · mangal · kazan · pass to guests
17. **Photo lounge "Ochag"** — drapes, carpets, fire bowl, 3 low tables, 12 poufs
18. **Kids zone** — against the hall glazing — seen from inside; soft floor
19. **Street benches** — cast concrete in the planter wall, majolica
20. **Sebil fountain** — majolica wall, brass spout, basin
21. **Street photo arch** — bench niche, uplight, palms

SEATS

Entrance tables	16
Chinar bench south	10
Dining south	18
Photo lounge (poufs)	12
Bar counter	9
Aivan: sedir booths (4 × 6)	24
Dining north + family table	28
Themed booths	32
Tapchan	6
Majlis tents (2 × 8)	16
Total restaurant seats	**171**
+ street benches (not counted)	~31

Tables: 4 two-tops, 12 four-tops, 1 six-top (all split into 2-top modules), 4 booths for 6

ERGONOMICS · standard / as planned

Main path / alley	≥1500	2500
Path to the booths	≥1200	1220
Path tapchan ↔ fountain	≥900	932
Aivan aisle	≥1200	1400
Table module: per guest / depth	600–700 / 750–800	700 / 800
Table edge → armchair back	450–600	525
Chair back to back (no path)	≥450	500
Armchair 580: gap between arms	≥100	120
Bar counter: height / overhang	1050 / 250–300	1050 / 300
Bar stool pitch	600–650	620
Cook work aisle	≥1200	2450
Pass → guests	≥1500	1570
Ramp: slope / width	1:12 / ≥1200	1:12 / 1300
Tapchan: height / per guest	400–450 / ≥600	450 / 700
Staff passage (clear at the columns)	≥1200	1275
Seat / table / armrest	450–500 / 740–760	500 / 760 / 660

KEY

- Roof column (steel, wood-clad)
- Building axis
- Staff route
- Hall door, closed
- Dimension, mm
- Skylight over the chinar
- Roof beam
- Guest entrance
- Hall door, open
- Exhaust hood
- Table no.
- Table module joint

- Base: as-built DWG (Long House, 10-07-2024) 1:1. Levels: sidewalk −1.170, terrace −0.450, aivan and hall ±0.000.
- Roof: steel beams on the grid, 50 mm sandwich panel, 5% fall to the street, gutter along the street; balcony soffit +3.850, wave louvers removed.
- One roof dome — the central Ø5.6 karbandi dome with a glazed lantern. The chinar by the bar stays under the roof: crown trained at 2.2–3.0 m, a 3.0 × 3.0 m skylight with a carved panjara grille above it. The north chinar is removed.
- Every loose table is a 700 × 800 module: pairs split into 2-tops or push together into tables for 6–8 (rows are aligned).
- Doors: C–D south open; C–D north and D–E south closed (banquette); D–E north and E–F by the lift open.

PLANTING

- **Pomegranate (anor), symbol of Samarkand** — at the entrance and in a pot by the bar
- **Plumeria (frangipani)** — street planter, evening scent
- **Bougainvillea and jasmine sambac** — on the street bench backs
- **Areca palm** — pots in the photo lounge
- **Banana, Strelitzia nicolai** — green frame of the Khiva gate
- **Reyhan, mint, basil** — herb bed by the mangal, to the table
- **Lotus, water lily** — in the hauz
- **Chinar by the bar (existing)** — under the skylight, trained crown, uplit

Scale 1:100 · A2

0 — 5 m

MANGAL KITCHEN · 1:100

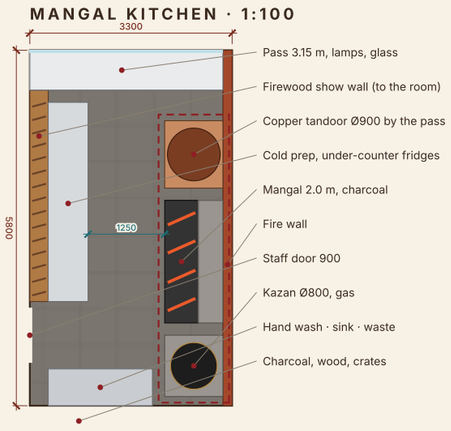

MAJLIS TENT (×2) · 1:75

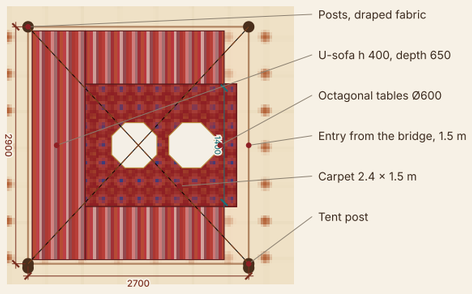

AIVAN: SEDIR BOOTHS · 1:75

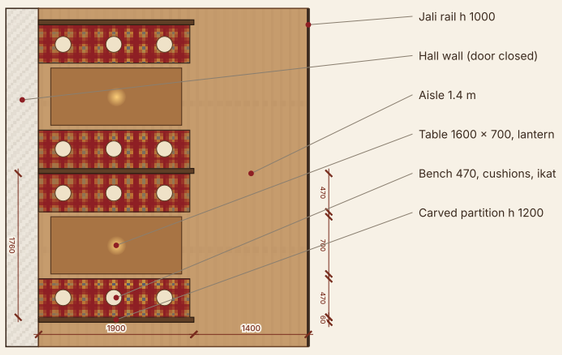

TABLE MODULES · 1:100

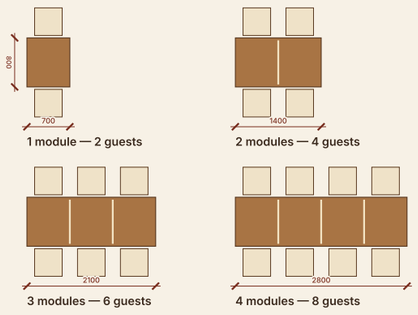

Top 700 × 800, h 750; joined with hidden clamps

Concept for client review · dimensions to verify on site

designed by Nomad Group