# SAMARKAND


R12

## Навес · концепция кровли

2026-10-28


План кровли 1:200 · разрезы 1:100

### ПЛАН КРОВЛИ · 1:200

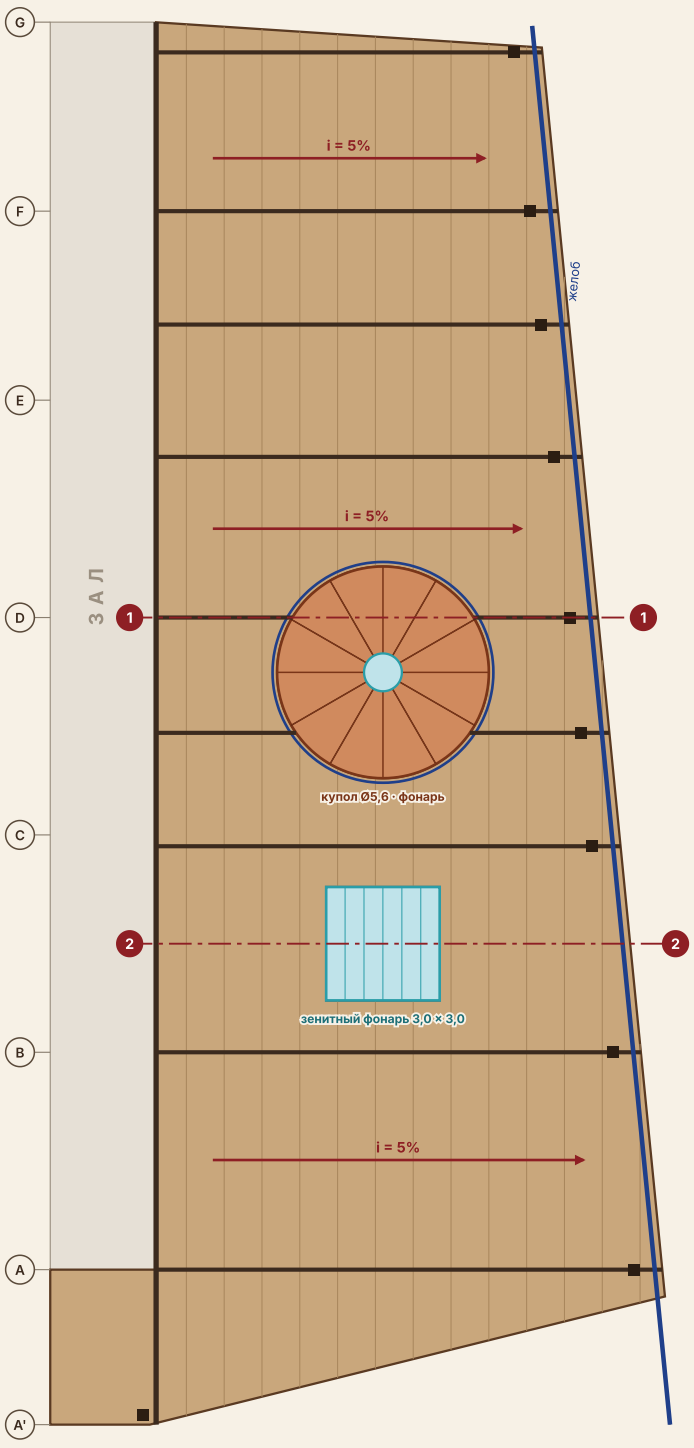



С

### РАЗРЕЗ 1–1 (по оси D, через центральный купол) · 1:100

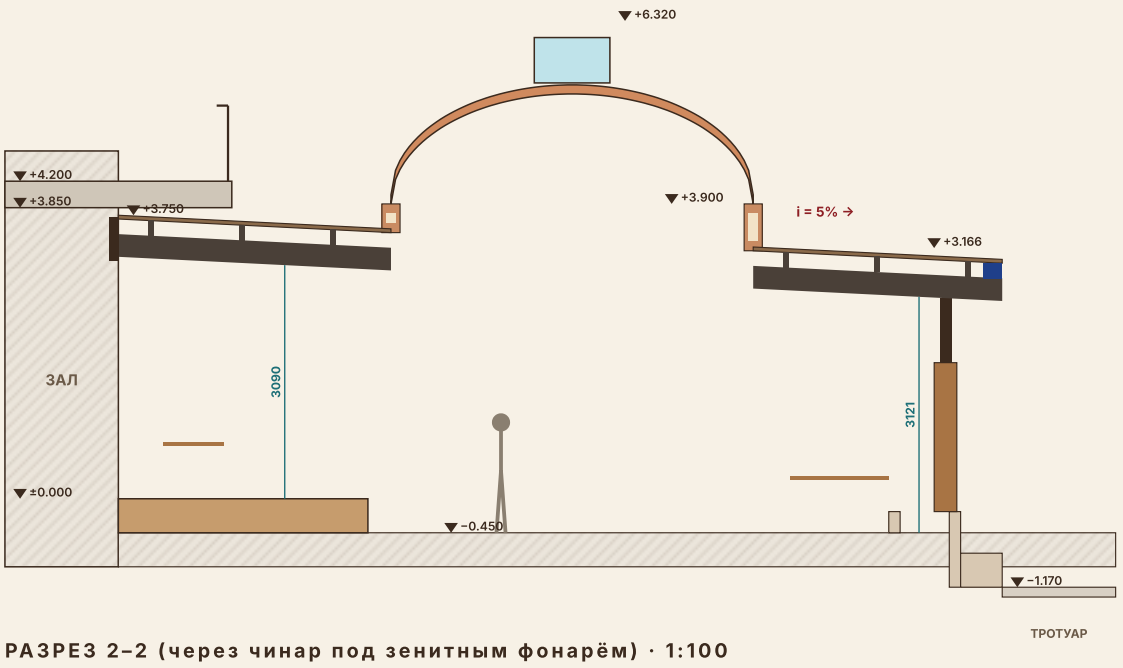


### РАЗРЕЗ 2–2 (через чинар под зенитным фонарём) · 1:100

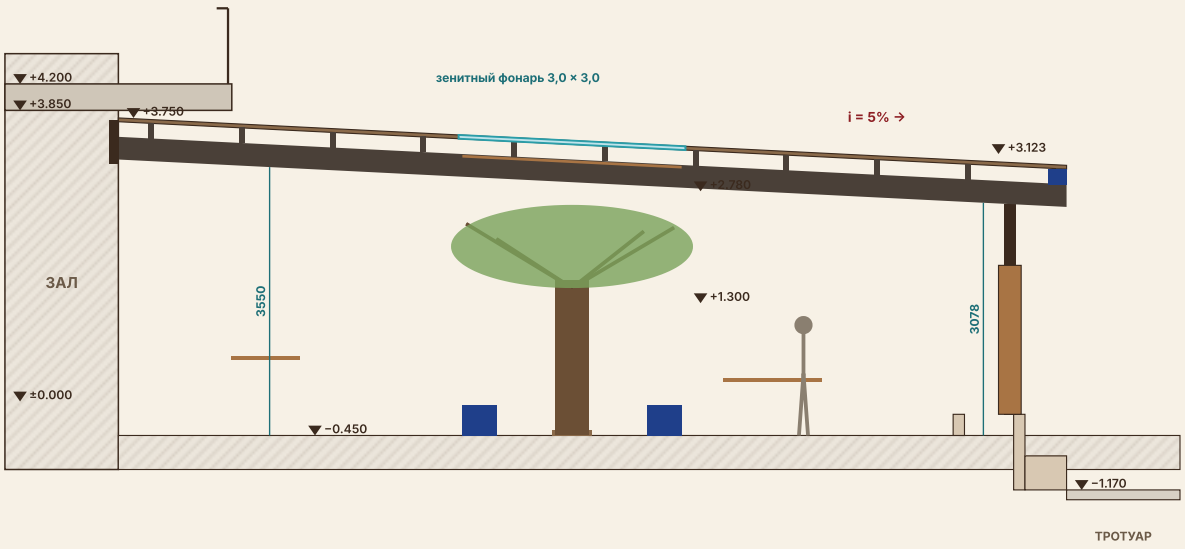


### РЕШЕНИЕ

- Балки: сталь, оцинковка + порошковая краска «тёмная бронза», по линиям колонн, шаг 3,0–5,75 м
- Опора у фасада: опорный уголок/швеллер на анкерах под плитой балкона (низ плиты +3.850)
- Опора у улицы: 9 колонн 150×150 в стенке клумбы, обшивка деревом; оголовок +2.9
- Прогоны С200 шаг 1,2 м; сэндвич-панель PU 50 мм с нижним слоем «под дерево»
- Уклон 5% к улице; коробчатый желоб вдоль улицы, водостоки внутри колонн → дренаж клумб
- Купол один — центральный Ø5,6 с остеклённым фонарём. Над чинаром у бара — зенитный фонарь 3,0 × 3,0 м: закалённый триплекс по прогонам в плоскости кровли (уклон 5%), алюминиевая рама с EPDM, снизу резная решётка-панджара; дерево под навесом, крона формуется. Северный чинар удаляется
- Купол: 12 гнутых рёбер 100×50 на опорном кольце +3.900, барабан с джали-окнами (свет + вытяжка горячего воздуха), внутри ГРЦ-панели «кирпич-гирих», снаружи терракотовое покрытие по мембране
- Деревянная реечная подшивка — только над баром и коридором (акцент)
- Волна-ламели под балконом демонтируются; фасад 2-го этажа остаётся открытым
- Тайфун: ветровой район II, анкеровка на отрыв; расчёт — инженер-конструктор

### ОБЪЁМЫ

| | |
|---|---|
| Площадь кровли | **412.9 м²** |
| Зенитный фонарь (стекло) | **9.0 м²** |
| Балки (пог. м) | **105.2 м** |
| Прогоны (пог. м) | **381.8 м** |
| Колонны | **11 шт** |
| Желоб вдоль улицы | **37.2 м** |
| Купол ø5,6 · фонарь | **36.2 + 7.9 м² · 37.1 м** |