SAMARKAND

Крытая терраса · планировка R6

Таджикская и узбекская кухня · Võ Nguyên Giáp, 254, Дананг

R6

2026-10-22

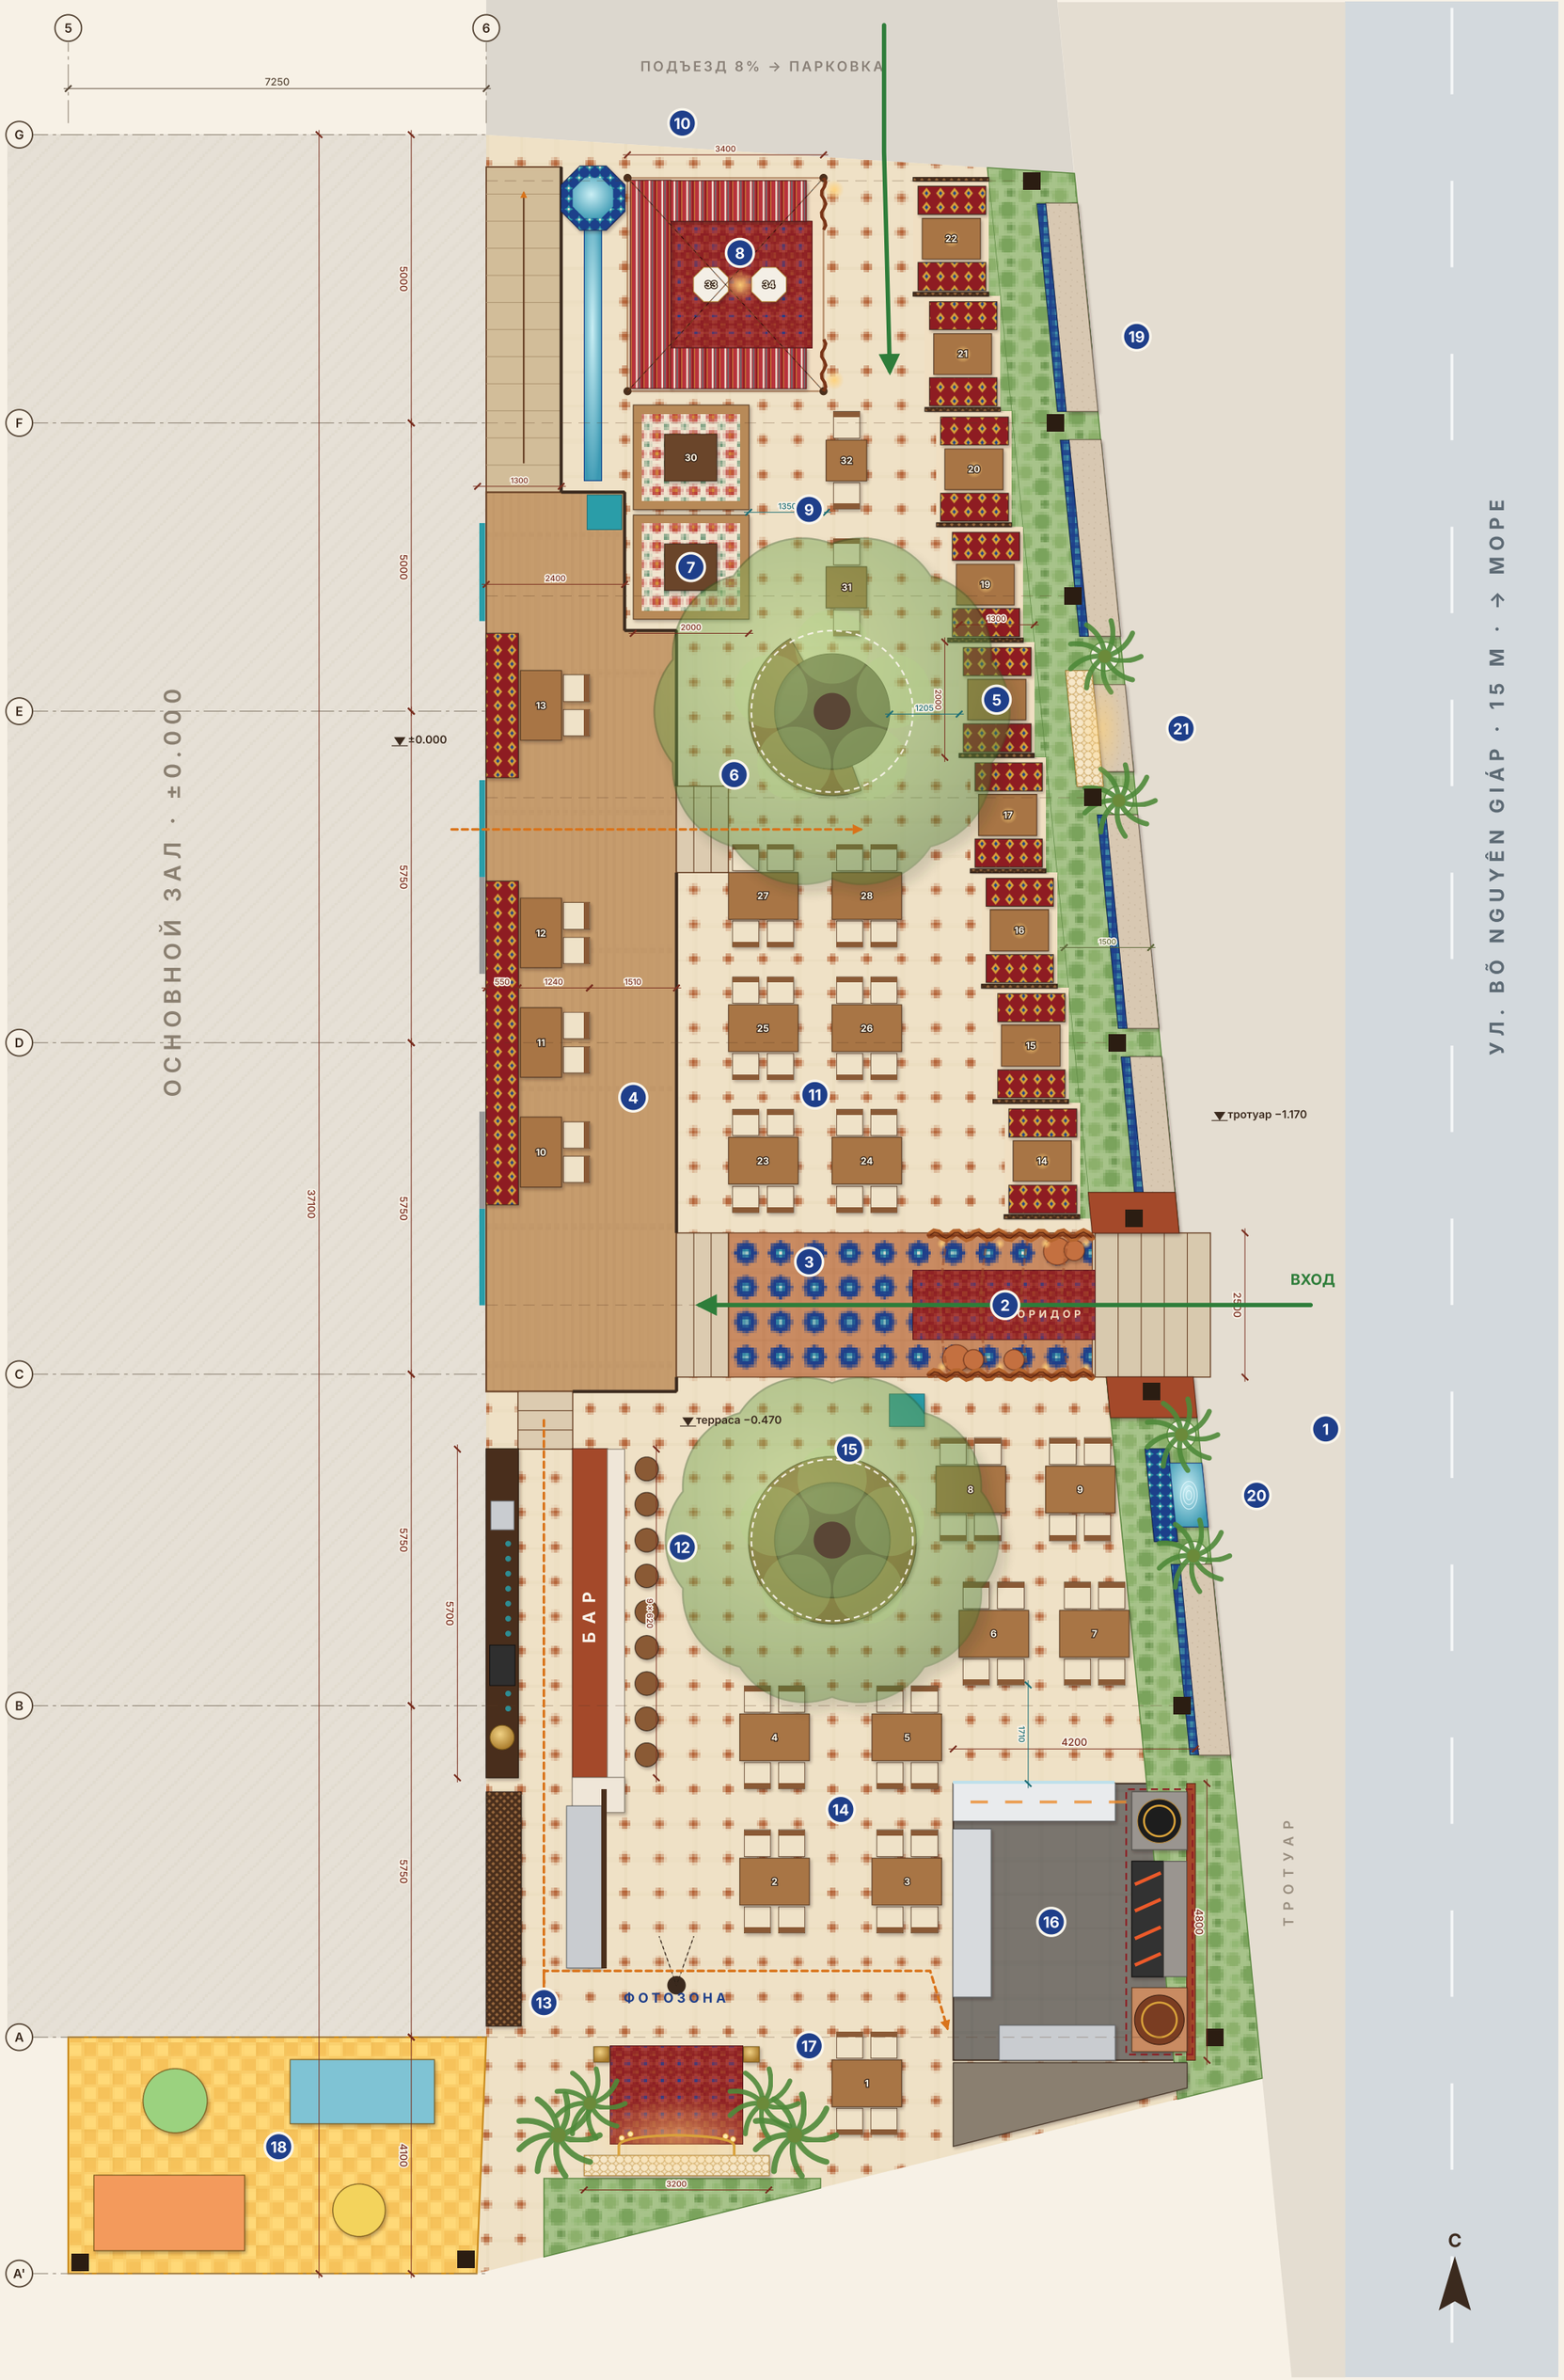

ЗОНЫ

1. **Главный вход · портал-пештак**
   проём 2,5 м, 4 ступени с тротуара
2. **Коридор-драпировка**
   бархат, ковровая дорожка, хумы, фонари
3. **Аллея к залу**
   гирих, 2,5 м, хостес у выхода
4. **Айван-платформа ±0.000**
   один ряд: банкетка у стены, 4 стола, проход 1,5 м
5. **Кабинки с видом на улицу**
   9 кабинок, резные ширмы, фонари
6. **Чинар-дворик (север)**
   дерево сохранено, скамья-полукольцо
7. **Топчаны у арыка**
   2 топчана, открыты к проходу
8. **Шатёр-маджлис**
   П-диван, ковёр, 2 стола, на 10 гостей
9. **Столики у северного входа**
   2 стола на 2
10. **Северный вход + пандус 1:12**
    с парковки, без ступеней, хауз
11. **Зал север**
    6 столов на 4
12. **Бар**
    чай, самовар, кофе · 9 стульев
13. **Станция персонала**
    стеллажи, касса, вода, лёд, посуда
14. **Зал юг**
    4 стола на 4
15. **Чинар-дворик (юг) + столы у входа**
    круглая скамья, 4 стола напротив мангала
16. **Мангальная 4,2 × 4,8 м**
    тандыр · мангал · казан · раздача к гостям
17. **Фотозона**
    арка-джали с подсветкой, пальмы, ковёр, свечи
18. **Детская зона**
    ограждение, мягкое покрытие
19. **Уличные скамьи**
    литой бетон в стенке клумбы, майолика
20. **Фонтан-себиль**
    майоликовая стена, латунный носик, чаша
21. **Уличная фото-арка**
    ниша со скамьёй, подсветка, пальмы

ПОСАДКА

Столы у входа	16
Скамья у чинара (юг)	10
Зал юг	16
Стол у фотозоны	4
Барная стойка	9
Айван-платформа	16
Зал север	24
Скамья у чинара (север)	6
Кабинки	36
Топчаны (2)	12
Шатёр-маджлис	10
Столики у северного входа	4
Итого мест в ресторане	**163**
+ уличные скамьи (вне счёта)	~35

ЭРГОНОМИКА · норма / по плану

Главный проход / аллея	≥1500	**2500**
Проход к кабинкам	≥1200	**1205**
Проход у топчанов	≥1200	**1350**
Проход на айване	≥1200	**1510**
Край стола → спинка стула	450–600	**490**
Спинка–спинка (без прохода)	≥450	**450**
Барная стойка: высота / вынос	1050 / 250–300	**1050 / 300**
Шаг барных стульев	600–650	**620**
Рабочая зона повара	≥1200	**2450**
Раздача → гости	≥1500	**1710**
Пандус: уклон / ширина	1:12 / ≥1200	**1:12 / 1300**
Уличная скамья: h / глубина	420–460 / ≥450	**450 / 550**

ОБОЗНАЧЕНИЯ

- Колонна навеса (сталь, обшивка деревом)
- Ось здания
- Маршрут персонала
- Дверь зала закрыта
- Размер, мм
- Линия фермы навеса
- Вход гостей
- Дверь зала открыта
- Вытяжной зонт
- № стола

· Основа: исполнительный DWG (Long House, 10.07.2024) 1:1. Отметки: тротуар −1.170, терраса −0.470, айван и зал ±0.000.

· Навес: стальные фермы по осям; колонны у улицы замоноличены в стенку клумбы за скамьями. Внутри обеденной зоны колонн нет.

· Деревья сохранены, проходят через проёмы в кровле Ø2,8 м. Шатёр — тканевый, под навесом, огнезащитная пропитка.

· Двери: C–D южная открыта; C–D северная и D–E южная закрыты (банкетка); D–E северная и E–F у лифта открыты.

· Скамьи и себиль — в границе участка, не выступают на тротуар. Мангальная: зонт и труба выше кровли.

МАНГАЛЬНАЯ · 1:75

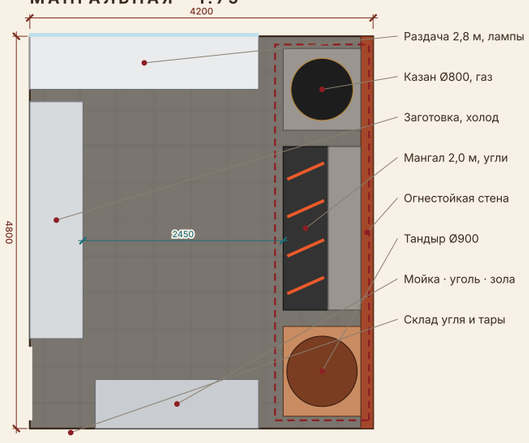

ШАТЁР-МАДЖЛИС · 1:75

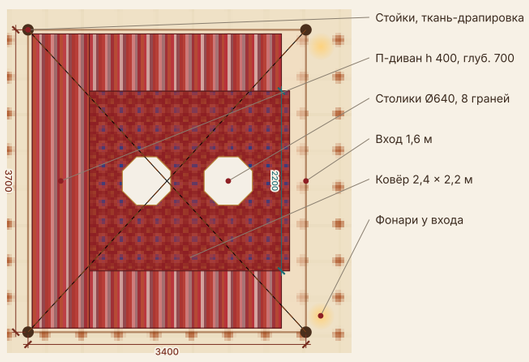

УЛИЧНАЯ СКАМЬЯ · РАЗРЕЗ 1:60

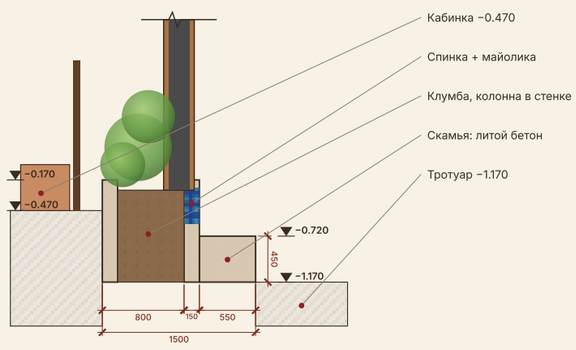

АЙВАН · РАЗРЕЗ 1:60

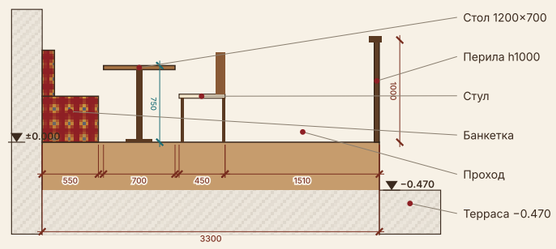

Концепция для согласования с заказчиком · размеры уточнить на месте

designed by Nomad Group