SAMARKAND

R12

Крытая терраса · планировка R12 · ред. 7

2026-10-28

Таджикская и узбекская кухня · Võ Nguyên Giáp, 254, Дананг

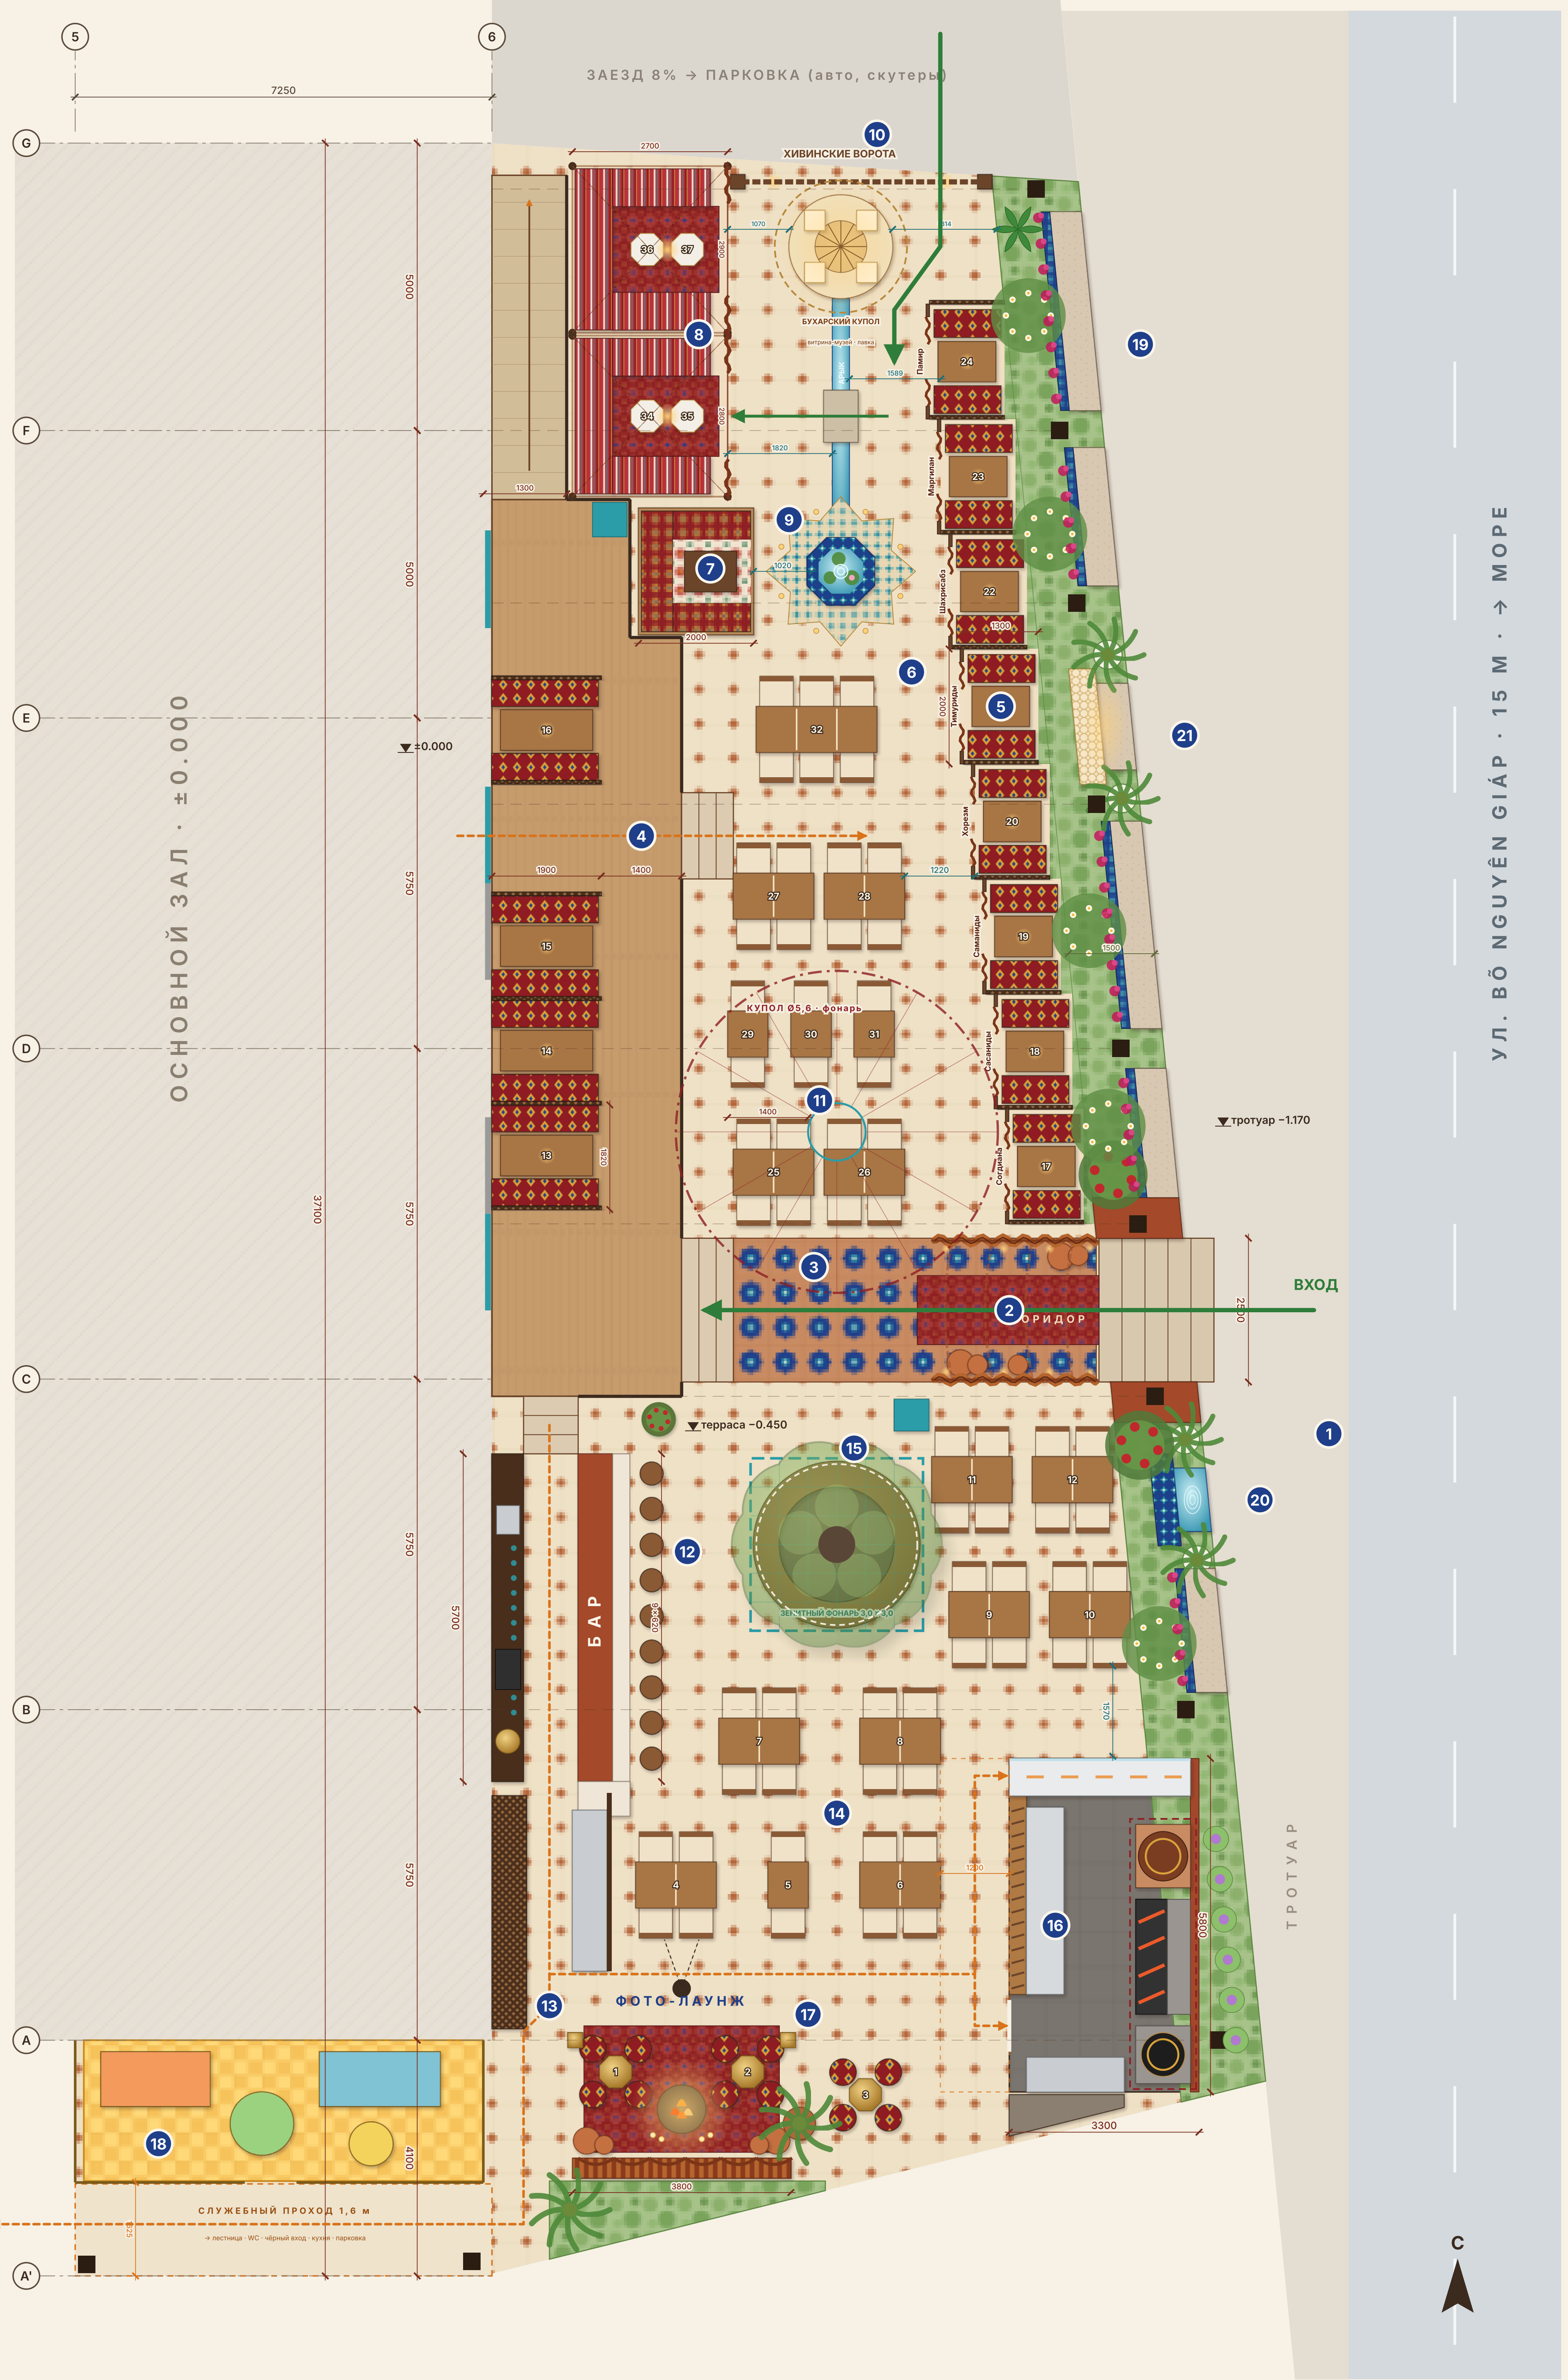
5
6
7250
G
F
E
D
C
B
A
A'
5000
5000
5750
5750
5750
5750
37100
5700
ОСНОВНОЙ ЗАЛ · ±0.000
±0.000
ЗАЕЗД 8% → ПАРКОВКА (авто, скутеры)
10
ХИВИНСКИЕ ВОРОТА
2700
2900
2800
1300
36
37
34
35
8
1070
814
БУХАРСКИЙ КУПОЛ
витрина-музей · лавка
АРЫК
1589
1820
9
7
1020
2000
Памир
24
Маргилан
23
Шахрисабз
22
1300
Тимуриды
2000
5
6
32
4
1900
1400
27
28
1220
Хорезм
20
Саманиды
19
1500
Сасаниды
18
Согдиана
17
16
15
14
13
1820
КУПОЛ Ø5,6 · фонарь
29
30
31
11
1400
25
26
3
2
КОРИДОР
ВХОД
2500
19
21
тротуар −1.170
1
20
терраса −0.450
15
ЗЕНИТНЫЙ ФОНАРЬ 3,0 × 3,0
11
12
9
10
12
БАР
9 × 620
1570
7
8
14
4
5
6
1200
16
5800
13
ФОТО-ЛАУНЖ
17
1
2
3
3300
18
4100
3800
СЛУЖЕБНЫЙ ПРОХОД 1,6 м
→ лестница · WC · чёрный вход · кухня · парковка
УЛ. VÕ NGUYÊN GIÁP · 15 М · → МОРЕ
ТРОТУАР
С

0 — 5 м · Масштаб 1:100 · A2

ЗОНЫ

1. **Главный вход · портал-пештак**
   проём 2,5 м, 4 ступени с тротуара
2. **Коридор-драпировка**
   бархат, ковровая дорожка, хумы, фонари
3. **Аллея к залу**
   гирих, 2,5 м, хостес у выхода
4. **Айван-платформа ±0.000**
   4 седир-кабинки на 6 у стены, проход 1,4 м
5. **Тематические кабинки**
   8 закрытых залов: эпохи и города, шторы-порталы
6. **Семейный стол на 6**
   у фонтана, на месте северного чинара
7. **Топчан 2,0 × 2,2 м**
   6 гостей, курпачи с 3 сторон, у фонтана
8. **Два шатра-маджлиса 2,6 × 2,75 м**
   по 8 гостей, вход по мостику через арык
9. **Фонтан-хауз и арык**
   хауз Ø1,2 м, арык 0,3 м ведёт от северного входа
10. **Северный вход · «Хивинские ворота»**
    ворота 4,1 м, Бухарский купол — витрина и лавка, пандус 1:12
11. **Зал север**
    ряды по 4 + средний ряд из 3 столов на 2
12. **Бар**
    чай, самовар, кофе · 9 стульев
13. **Станция персонала**
    стеллажи, касса, вода, лёд, посуда
14. **Зал юг**
    ряд 4 + 2 + 4 и ряд 4 + 4
15. **Чинар под фонарём + столы у входа**
    дерево под навесом, зенитный фонарь 3 × 3 м; 4 стола у мангала
16. **Мангальная 3,3 × 5,8 м**
    тандыр · мангал · казан · раздача к гостям
17. **Фото-лаунж «Очаг»**
    драпировки, ковры, огонь-чаша, 3 столика, 12 пуфов
18. **Детская зона**
    у стекла зала — дети видны из зала; мягкое покрытие
19. **Уличные скамьи**
    литой бетон в стенке клумбы, майолика
20. **Фонтан-себиль**
    майоликовая стена, латунный носик, чаша
21. **Уличная фото-арка**
    ниша со скамьёй, подсветка, пальмы

ПОСАДКА

Столы у входа	16
Скамья у чинара (юг)	10
Зал юг	18
Фото-лаунж (пуфы)	12
Барная стойка	9
Айван: седир-кабинки (4 × 6)	24
Зал север + семейный стол	28
Тематические кабинки	32
Топчан	6
Шатры-маджлисы (2 × 8)	16
Итого мест в ресторане	**171**
+ уличные скамьи (вне счёта)	~31

Столы: на 2 — 4, на 4 — 12, на 6 — 1 (все делятся на модули 2-местные), кабинки на 6 — 4

ЭРГОНОМИКА · норма / по плану

Главный проход / аллея	≥1500	**2500**
Проход к кабинкам	≥1200	**1220**
Проход топчан ↔ фонтан	≥900	**932**
Проход на айване	≥1200	**1400**
Модуль стола: на 1 гостя / глубина	600–700 / 750–800	**700 / 800**
Край стола → спинка кресла	450–600	**525**
Спинка–спинка (без прохода)	≥450	**500**
Кресло 580: зазор между подлокотниками	≥100	**120**
Барная стойка: высота / вынос	1050 / 250–300	**1050 / 300**
Шаг барных стульев	600–650	**620**
Рабочая зона повара	≥1200	**2450**
Раздача → гости	≥1500	**1570**
Пандус: уклон / ширина	1:12 / ≥1200	**1:12 / 1300**
Топчан: высота / на 1 гостя	400–450 / ≥600	**450 / 700**
Служебный проход (в свету у колонн)	≥1200	**1275**
Сиденье / стол / подлокотник	450–500 / 740–760	**500 / 760 / 660**

ОБОЗНАЧЕНИЯ

■	Колонна навеса (сталь, обшивка деревом)	– –	Балка навеса
—·—	Ось здания	➡	Вход гостей
- - -	Маршрут персонала	▬	Дверь зала открыта
▬	Дверь зала закрыта	– –	Вытяжной зонт
⟋	Размер, мм	12	№ стола
⬚	Зенитный фонарь над чинаром	▮	Стык модулей стола

- Основа: исполнительный DWG (Long House, 10.07.2024) 1:1. Отметки: тротуар −1.170, терраса −0.450, айван и зал ±0.000.
- Навес: стальные балки по осям, сэндвич-панель 50 мм, уклон 5% к улице, желоб вдоль улицы; низ плиты балкона +3.850, волна-ламели демонтируются.
- Купол в кровле один — центральный Ø5,6 (карбанди, остеклённый фонарь). Чинар у бара остаётся под навесом: крона формуется на высоте 2,2–3,0 м, над ним зенитный фонарь 3,0 × 3,0 м с резной решёткой-панджарой. Северный чинар удаляется.
- Все отдельно стоящие столы — модули 700 × 800: пары разъединяются на 2-местные или сдвигаются в столы на 6–8 (ряды выровнены).
- Двери: C–D южная открыта; C–D северная и D–E южная закрыты (банкетка); D–E северная и E–F у лифта открыты.

ОЗЕЛЕНЕНИЕ

- **Гранат (анор) — символ Самарканда**
  у входа в клумбе и в кадке у бара
- **Плюмерия (франжипани)**
  в уличной клумбе, аромат вечером
- **Бугенвиллия и жасмин самбак**
  по спинкам уличных скамей
- **Пальма арека**
  кадки в фото-лаунже
- **Банан, стрелиция Николая**
  зелёная рамка Хивинских ворот
- **Райхон, мята, базилик**
  грядка у мангальной — к столу
- **Лотос, кувшинка**
  в хаузе
- **Чинар у бара (существующий)**
  под зенитным фонарём, формовка кроны, подсветка снизу

МАНГАЛЬНАЯ · 1:100

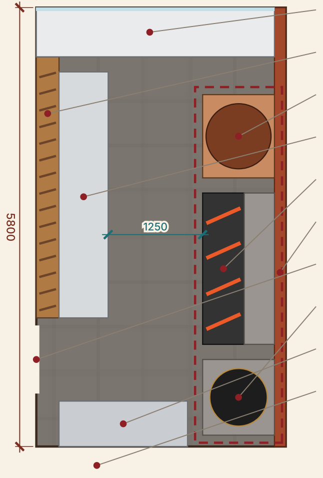
3300
5800
1250

- Раздача 3,15 м, лампы, стекло
- Дровница-витрина (в зал)
- Тандыр Ø900 в меди — у раздачи
- Заготовка, холод под столом
- Мангал 2,0 м, угли
- Огнестойкая стена
- Служебная дверь 900
- Казан Ø800, газ
- Руки · мойка · отходы
- Уголь, дрова, тара

ШАТЁР-МАДЖЛИС (×2) · 1:75

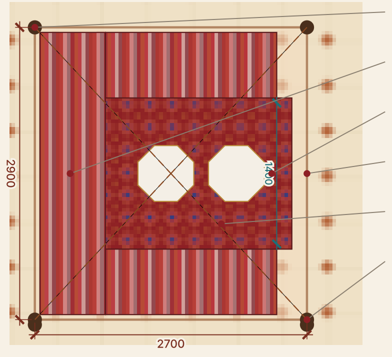
2900
2700
1400

- Стойки, ткань-драпировка
- П-диван h 400, глуб. 650
- Столики Ø600, 8 граней
- Вход с мостика, 1,5 м
- Ковёр 2,4 × 1,5 м
- Стойка шатра

АЙВАН: СЕДИР-КАБИНКИ · 1:75

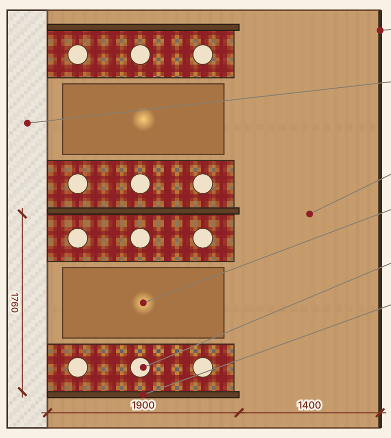
1760
1900
1400
470
760
470
60

- Перила-джали h 1000
- Стена зала (дверь закрыта)
- Проход 1,4 м
- Стол 1600 × 700, фонарь
- Скамья 470, подушки, икат
- Резная перегородка h 1200

СТОЛЫ-МОДУЛИ · 1:100

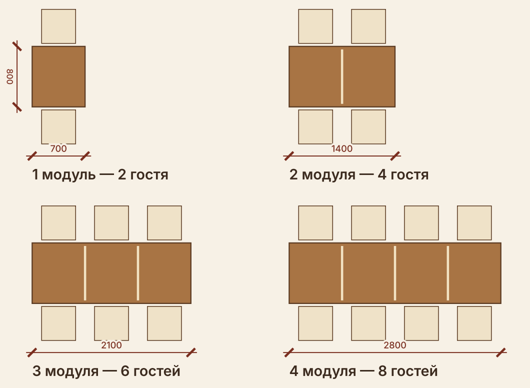
800
700
1400
2100
2800

1 модуль — 2 гостя

2 модуля — 4 гостя

3 модуля — 6 гостей

4 модуля — 8 гостей

Столешница 700 × 800, h 750; стык на скрытых стяжках

Концепция для согласования с заказчиком · размеры уточнить на месте

designed by Nomad Group