SAMARKAND


Навес · концепция кровли

План кровли 1:200 · разрезы 1:100

R12


2026-10-28

ПЛАН КРОВЛИ · 1:200

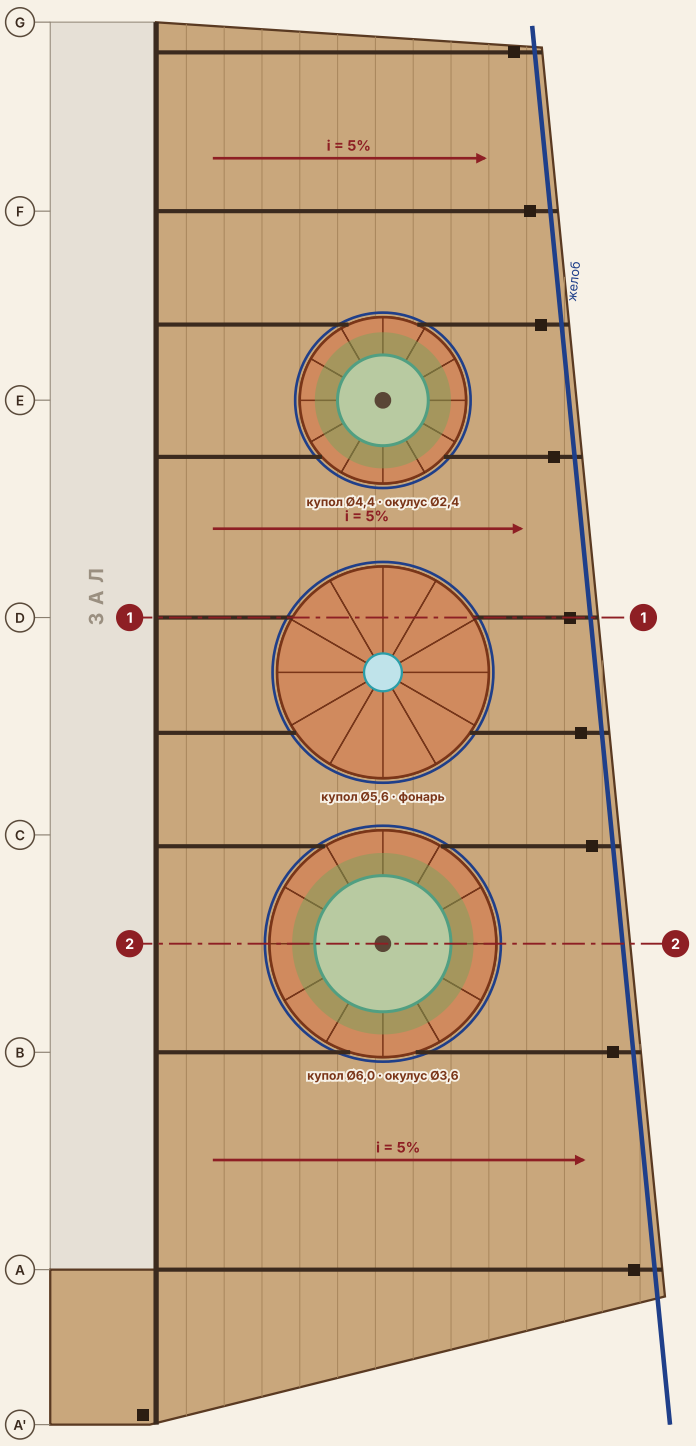


С

РАЗРЕЗ 1–1 (по оси D, через центральный купол) · 1:100

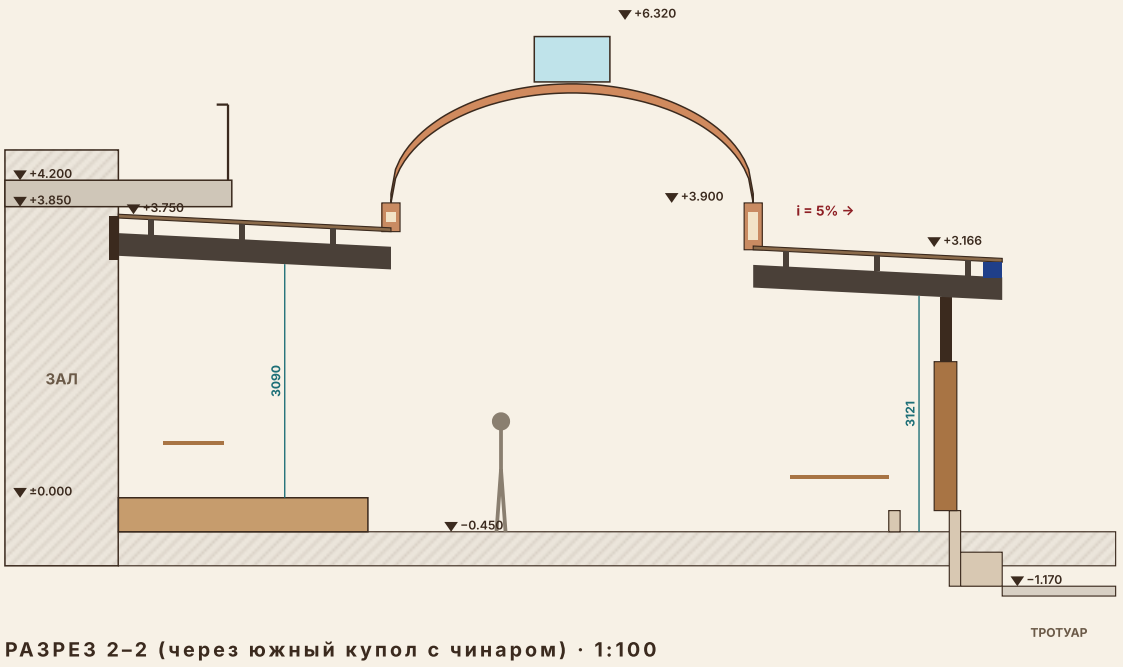

РАЗРЕЗ 2–2 (через южный купол с чинаром) · 1:100

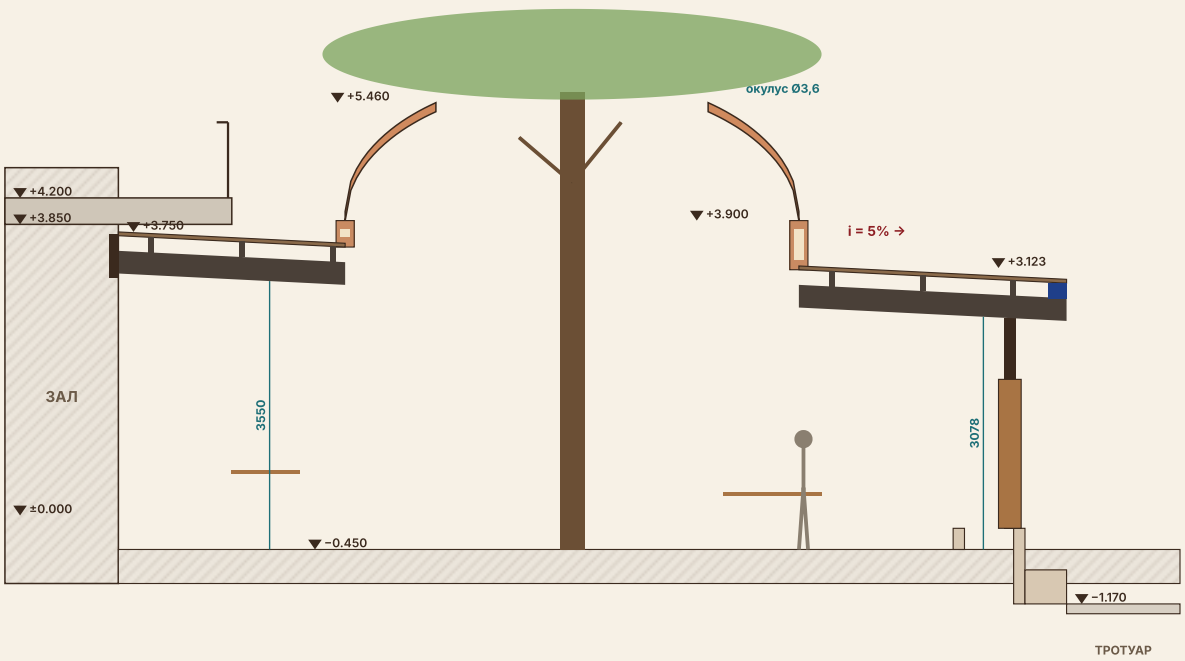

РЕШЕНИЕ

- Балки: сталь, оцинковка + порошковая краска «тёмная бронза», по линиям колонн, шаг 3,0–5,75 м
- Опора у фасада: опорный уголок/швеллер на анкерах под плитой балкона (низ плиты +3.850)
- Опора у улицы: 9 колонн 150×150 в стенке клумбы, обшивка деревом; оголовок +2.9
- Прогоны С200 шаг 1,2 м; сэндвич-панель PU 50 мм с нижним слоем «под дерево»
- Уклон 5% к улице; коробчатый желоб вдоль улицы, водостоки внутри колонн → дренаж клумб
- Купола: над чинарами Ø6,0 и Ø4,4 с открытым окулусом Ø3,6 / Ø2,4 (крона выходит наружу, дождь — в приствольную яму), между ними глухой Ø5,6 с остеклённым фонарём
- Купол: 12 гнутых рёбер 100×50 на опорном кольце +3.900, барабан с джали-окнами (свет + вытяжка горячего воздуха), внутри ГРЦ-панели «кирпич-гирих», снаружи терракотовое покрытие по мембране
- Деревянная реечная подшивка — только над баром и коридором (акцент)
- Волна-ламели под балконом демонтируются; фасад 2-го этажа остаётся открытым
- Тайфун: ветровой район II, анкеровка на отрыв; расчёт — инженер-конструктор

ОБЪЁМЫ

Площадь кровли	**378.4 м²**
Окулусы (открыто)	**14.7 м²**
Балки (пог. м)	**105.2 м**
Прогоны (пог. м)	**338.7 м**
Колонны	**11 шт**
Желоб улица / дворики	**37.2 / 18.8 м**
Купол ø6.0 · окулус ø3.6	**31.6 + 8.5 м² · 28.0 м**
Купол ø5.6 · фонарь	**36.2 + 7.9 м² · 37.1 м**
Купол ø4.4 · окулус ø2.4	**17.9 + 6.2 м² · 21.3 м**

Концепция · сечения и узлы подтверждает расчёт конструктора