
ZONES

Kids zone	**29.4 m²**
East entrance plaza	**37.8 m²**
Alley	**17.0 m²**
Bar (incl. stools)	**21.9 m²**
BBQ / outdoor kitchen	**15.0 m²**
BBQ viewing / queue	**5.9 m²**
Photo zone	**20.3 m²**
Dining + circulation (rest)	**256.8 m²**
Planters (kept)	**42.4 m²**
Usable total (car ramp kept)	**446.5 m²**

WHY THIS WORKS

- Two entrances, one spine: street stair → plaza → alley → hall doors; parking → north aisle.
- Bar on the façade under the balcony: closest to the hall, waiter pick-up faces the dining.
- BBQ on the street side: smoke goes out over the planter, the show faces the alley and plaza.
- Kids + photo at the quiet south end, 9 m from the fire, visible from the dining.
- Staff (orange) use doors D–E / C–D, stations W1/W2, never cross the kids zone.
- Tapchans under the existing canopy: shade, privacy, family tables next to parking.
- Aisles ≥ 1200, alley 3400, 600 between chair backs, 2550 clear at the hall doors.
- Roof columns sit on the building grid, inside planters or in aisle gaps.

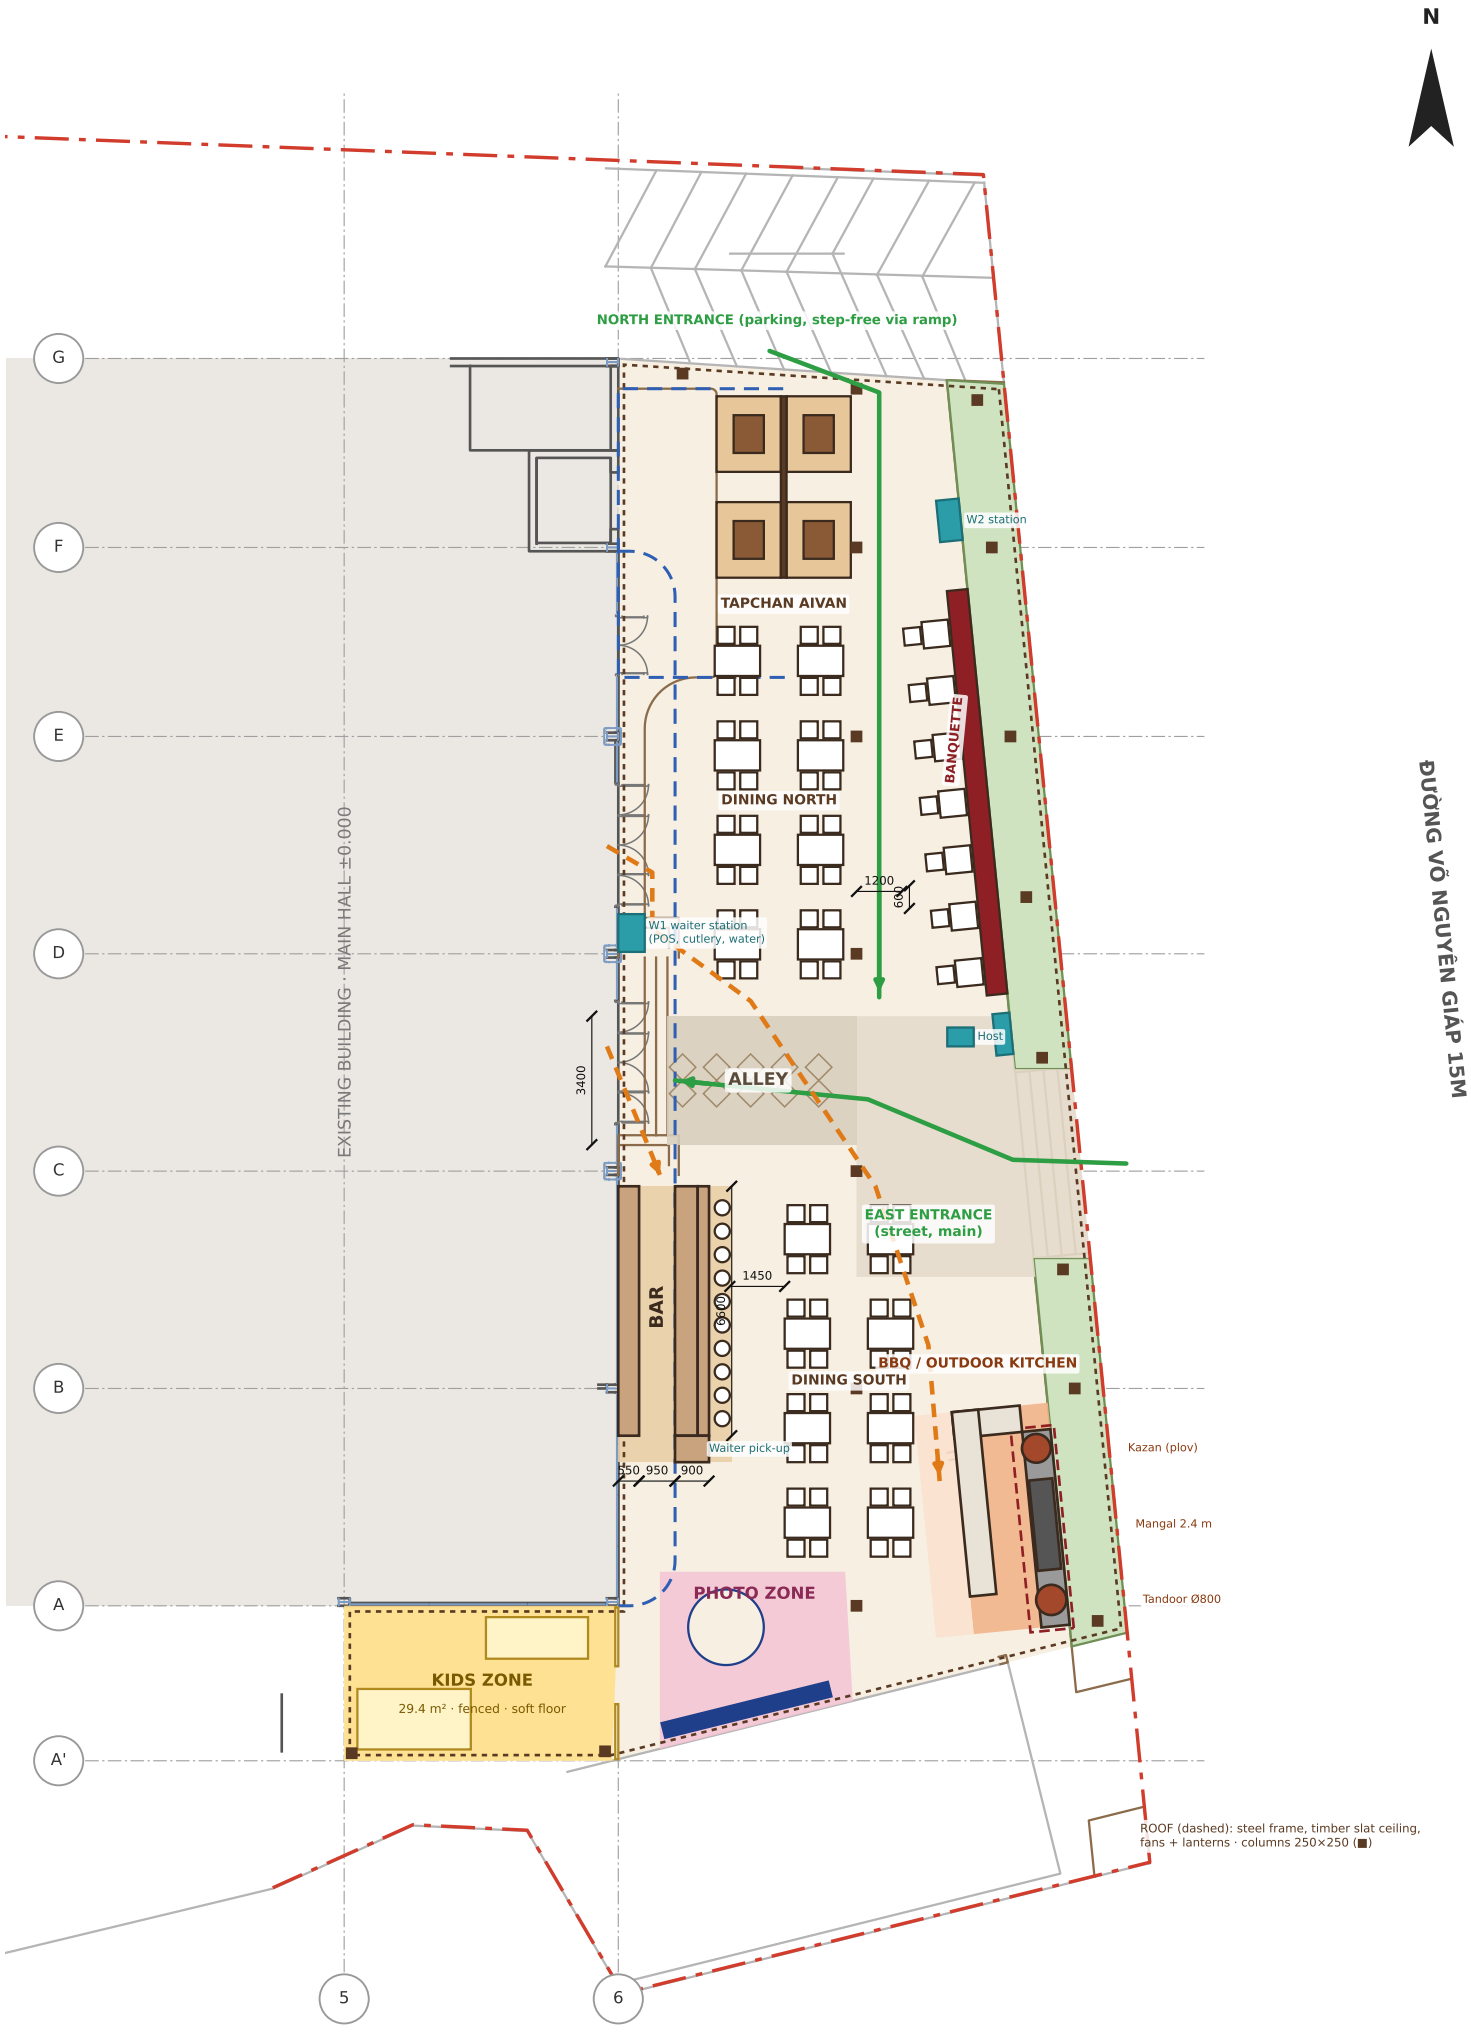

Guest flow · Staff flow · New roof edge · Existing canopy / balcony above · Exhaust hood

SAMARKAND

Covered terrace — layout R1 (zoning, furniture, flows)

254 Võ Nguyên Giáp, Đà Nẵng · base: as-built DWG 10-07-2024

Assumptions: terrace floor stays −0.470 · car ramp kept · planters on boundary kept · old pergola and round elements removed · new roof over the whole zone.

Origin (0,0) = axis 6 × axis A'. Units mm. Scale 1:200 @ A3. 2026-10-22 · R1

Bar counter	**10**
South dining 4-tops	**32**
North dining 4-tops	**32**
Tapchans (hybrid, 6 pax)	**24**
Banquette 2-tops	**14**
TOTAL SEATS	**112**