
SAMARKAND

Крытая терраса · планировка R3

Таджикская и узбекская кухня · Võ Nguyên Giáp, 254, Дананг

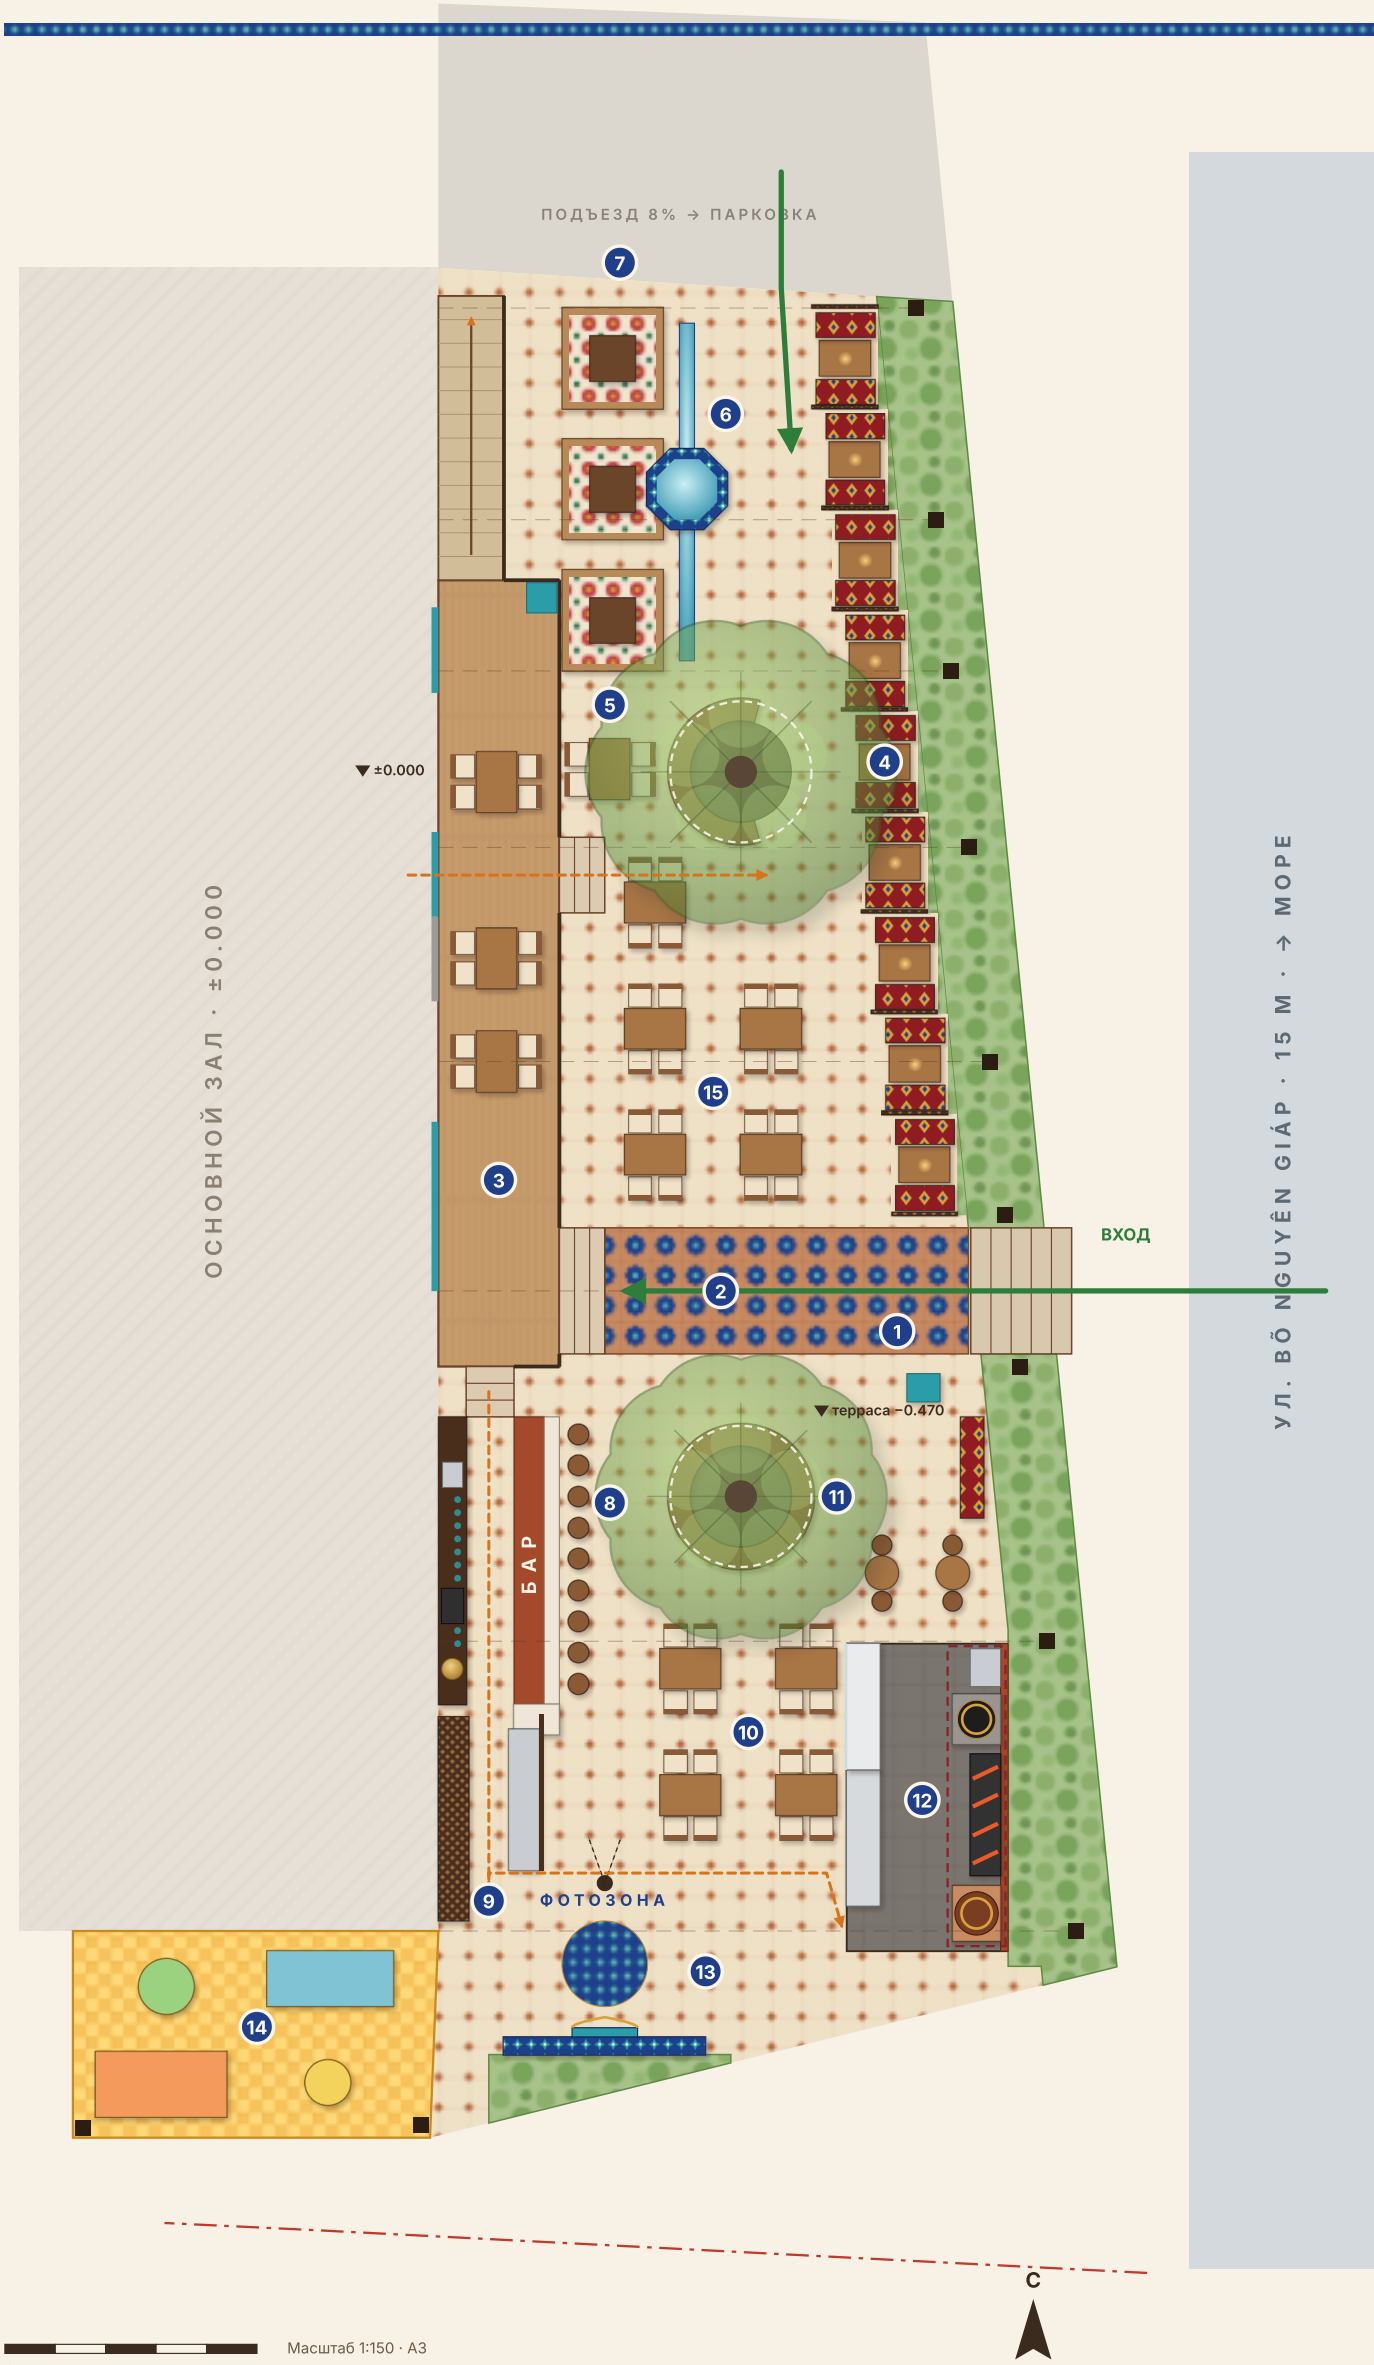

ЗОНЫ

1. **Главный вход с улицы**
   проём 2,5 м, хостес, лавка ожидания
2. **Аллея**
   орнамент-гирих, 2,5 м, к дверям зала
3. **Айван-платформа ±0.000**
   бывшие ступени, 3 стола, перила
4. **Кабинки с видом на море**
   9 кабинок, резные ширмы, фонари
5. **Чинар-дворик (север)**
   дерево сохранено, круглая скамья
6. **Топчаны у арыка и хауза**
   3 топчана, вода, тень
7. **Северный вход + пандус 1:12**
   с парковки, без ступеней
8. **Бар**
   чай, самовар, кофе · 9 стульев
9. **Станция персонала**
   стеллажи, касса, вода, лёд, посуда
10. **Зал юг**
    4 стола на 4
11. **Чинар-дворик (юг)**
    дерево у входа, круглая скамья
12. **Мангальная**
    тандыр · мангал · казан · заготовка · раздача
13. **Фотозона**
    пештак с майоликой, медальон, точка съёмки
14. **Детская зона**
    ограждение, мягкое покрытие
15. **Зал север**
    6 столов на 4


ПОСАДКА

Барная стойка	9
Зал юг	16
Скамья у чинара (юг)	10
Высокие столы у мангала	4
Айван-платформа	12
Кабинки у моря	36
Зал север	24
Скамья у чинара (север)	7
Топчаны	18
Итого мест	**136**

ОБОЗНАЧЕНИЯ

- Колонна навеса (сталь, обшивка деревом)
- Линия фермы навеса
- Вход гостей
- Маршрут персонала
- Дверь зала открыта
- Дверь зала закрыта
- Вытяжной зонт

МАНГАЛЬНАЯ · 1:100

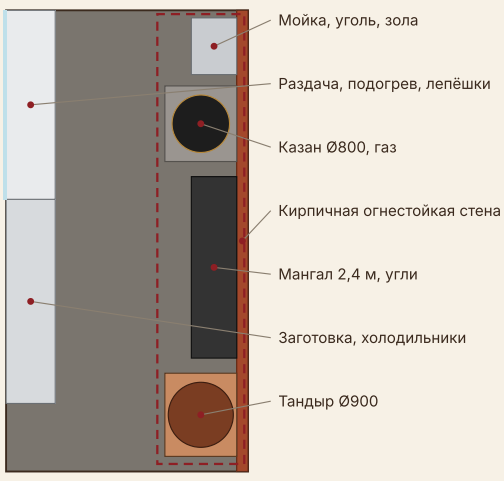

Проход повара 1,45–1,65 м · зонт и труба выше кровли
Огнетушитель, отсекатель газа, трап, сланец

Основа: исполнительный чертёж DWG (Long House, 10.07.2024) в масштабе 1:1. Отметки: терраса −0.470, платформа и зал ±0.000.
Навес: стальные фермы по сетке осей, колонны спрятаны в озеленении у улицы, у фасада опорная балка (проверка инженером).
Внутри обеденной зоны колонн нет. Деревья сохранены и проходят через проёмы в кровле Ø2,8 м.
Одна дверь D–E закрыта (перед ней стол). Северная дверь D–E и задняя дверь у лифта выходят на платформу.