SAMARKAND

Covered terrace · Layout R6

Tajik & Uzbek national cuisine · 254 Võ Nguyên Giáp, Đà Nẵng

R6

2026-10-22

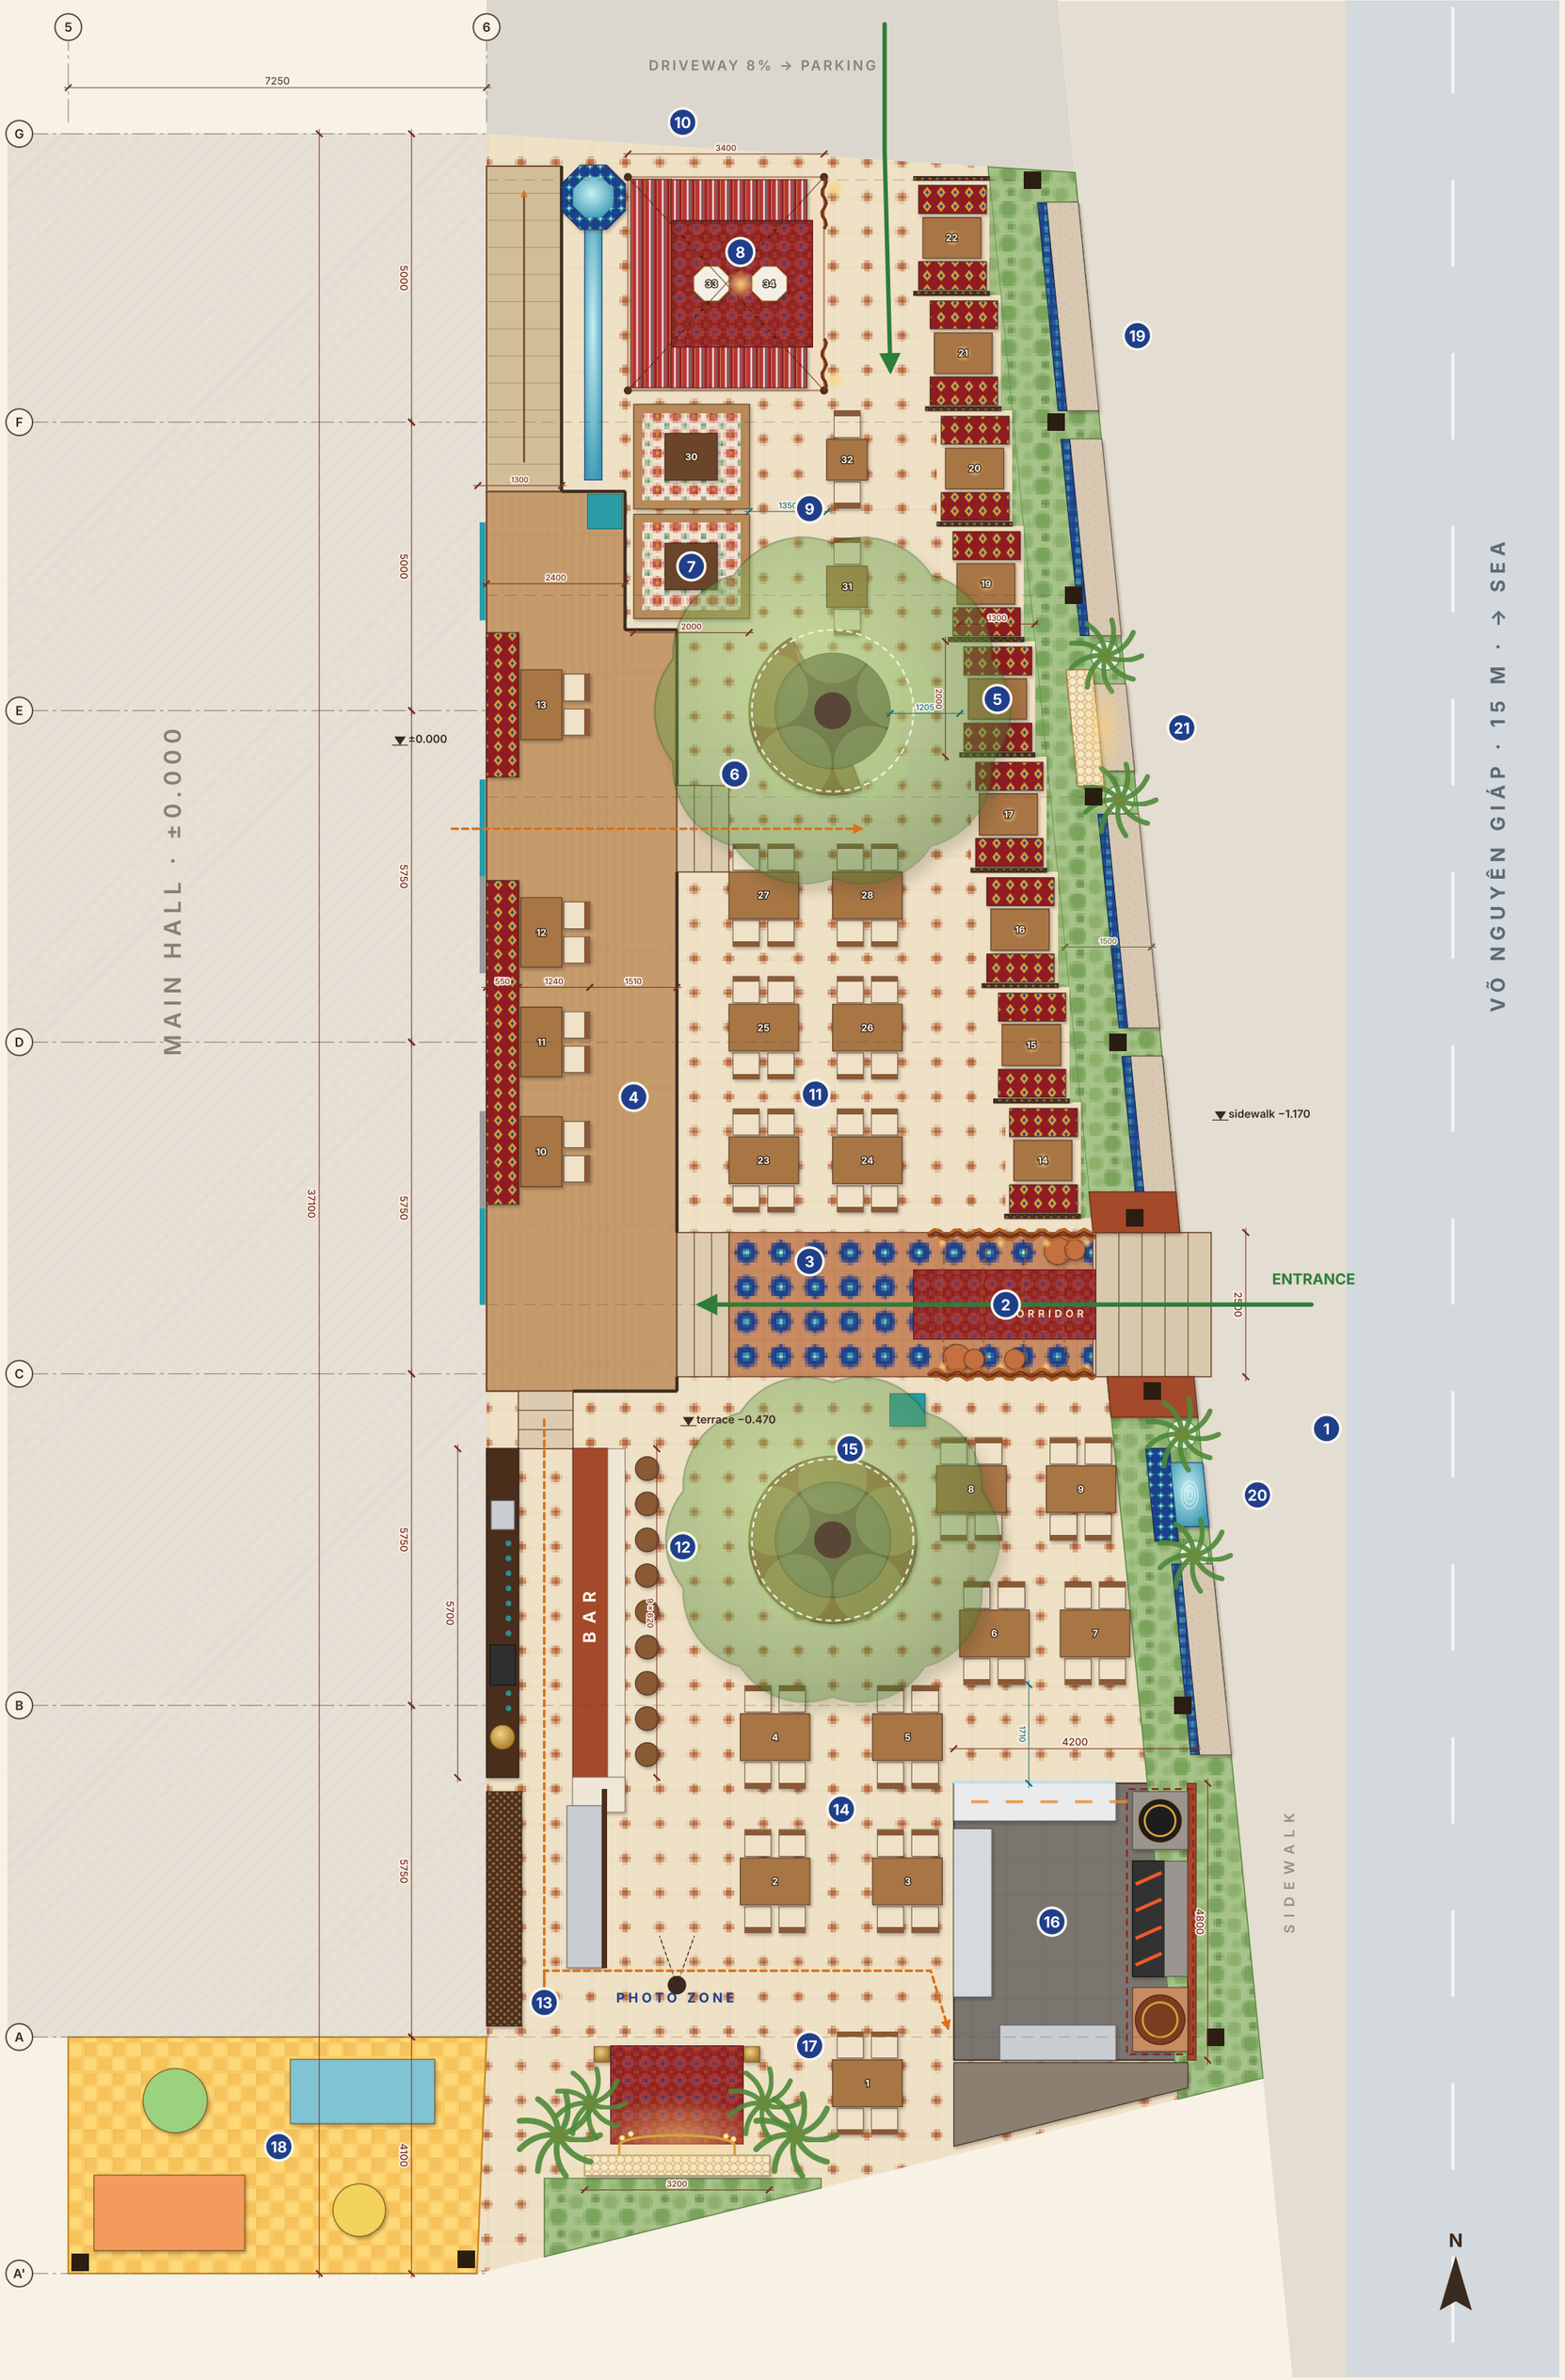

ZONES

1. **Street entrance · pishtaq portal**
   2.5 m opening, 4 steps from the sidewalk
2. **Draped corridor**
   velvet swags, runner, clay jars, lanterns
3. **Alley to the hall**
   girih paving, 2.5 m, host at the exit
4. **Aivan platform ±0.000**
   one row: wall banquette, 4 tables, 1.5 m aisle
5. **Street-view booths**
   9 booths, carved screens, lanterns
6. **Chinar court north**
   tree kept, half-ring bench
7. **Tapchans by the aryk**
   2 tapchans, open to the path
8. **Majlis tent**
   U-sofa, carpet, 2 tables, 10 guests
9. **Tables at the north entrance**
   2 tables for 2
10. **North entrance + ramp 1:12**
    from parking, step-free, hauz
11. **Dining north**
    6 tables for 4
12. **Bar**
    tea, samovar, coffee · 9 stools
13. **Staff station**
    shelving, POS, water, ice, dishes
14. **Dining south**
    4 tables for 4
15. **Chinar court south + entrance tables**
    round bench, 4 tables facing the mangal
16. **Mangal kitchen 4.2 × 4.8 m**
    tandoor · mangal · kazan · pass to guests
17. **Photo zone**
    backlit jali arch, palms, rug, candles
18. **Kids zone**
    fenced, soft floor
19. **Street benches**
    cast concrete in the planter wall, majolica
20. **Sebil fountain**
    majolica wall, brass spout, basin
21. **Street photo arch**
    bench niche, uplight, palms

SEATS

Entrance tables	16
Chinar bench south	10
Dining south	16
Table by the photo zone	4
Bar counter	9
Aivan platform	16
Dining north	24
Chinar bench north	6
Booths	36
Tapchans (2)	12
Majlis tent	10
Tables at the north entrance	4
Total restaurant seats	**163**
+ street benches (not counted)	~35

ERGONOMICS · standard / as planned

Main path / alley	≥1500	**2500**
Path to the booths	≥1200	**1205**
Path by the tapchans	≥1200	**1350**
Aivan aisle	≥1200	**1510**
Table edge → chair back	450–600	**490**
Chair back to back (no path)	≥450	**450**
Bar counter: height / overhang	1050 / 250–300	**1050 / 300**
Bar stool pitch	600–650	**620**
Cook work aisle	≥1200	**2450**
Pass → guests	≥1500	**1710**
Ramp: slope / width	1:12 / ≥1200	**1:12 / 1300**
Street bench: h / depth	420–460 / ≥450	**450 / 550**

KEY

- Roof column (steel, wood-clad)
- Building axis
- Staff route
- Hall door, closed
- Dimension, mm
- Roof truss line
- Guest entrance
- Hall door, open
- Exhaust hood
- Table no.

· Base: as-built DWG (Long House, 10-07-2024) 1:1. Levels: sidewalk −1.170, terrace −0.470, aivan and hall ±0.000.

· Roof: steel trusses on the grid; street-side columns cast into the planter wall behind the benches. No columns in the dining.

· Trees kept, through Ø2.8 m roof oculi. The tent is fabric under the roof, fire-retardant treated.

· Doors: C–D south open; C–D north and D–E south closed (banquette); D–E north and E–F by the lift open.

· Benches and sebil stay inside the lot line, nothing projects onto the sidewalk. Mangal: hood + stack above the roof.

MANGAL KITCHEN · 1:75

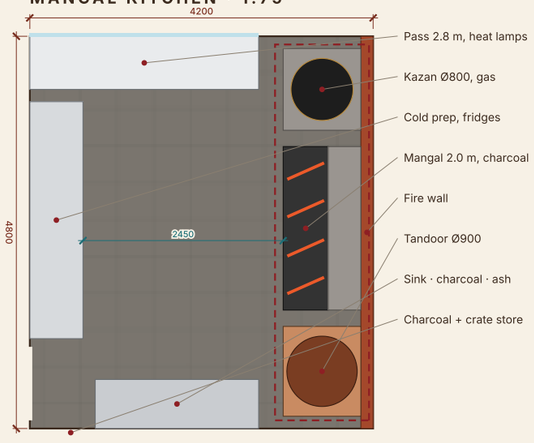

MAJLIS TENT · 1:75

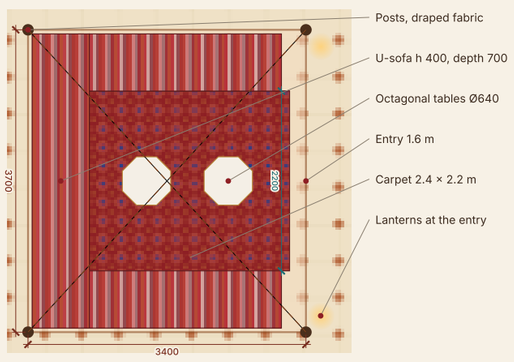

STREET BENCH · SECTION 1:60

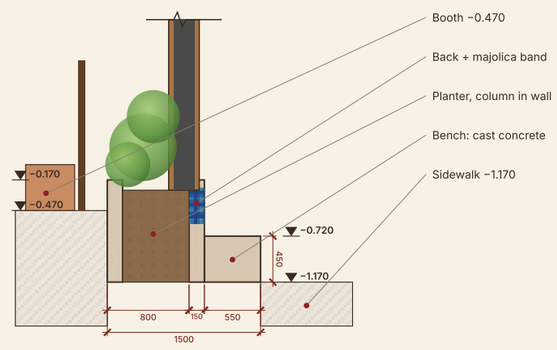

AIVAN · SECTION 1:60

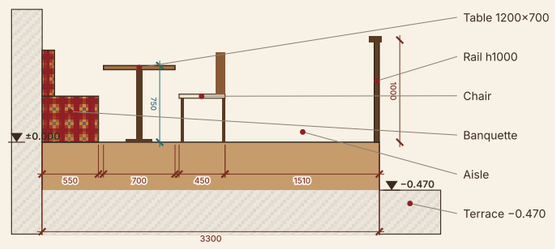

Concept for client review · dimensions to verify on site

designed by Nomad Group