

KEY PLAN — whole lot, design zone in green

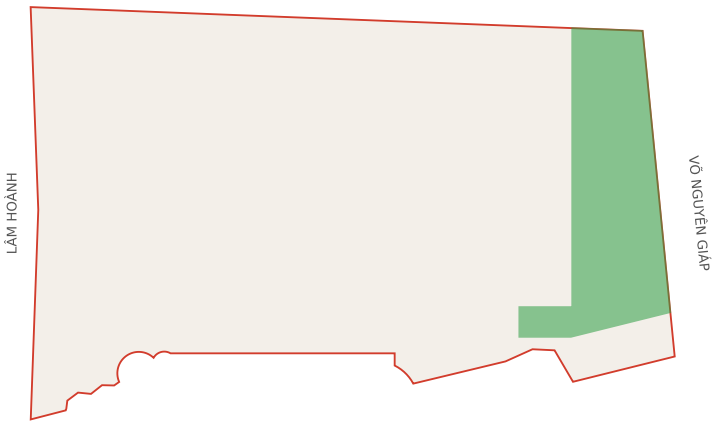

VERIFY ON SITE BEFORE DESIGN FREEZE

1. Entrance canopy: F1 plan 4404 × 7638, site plan shows 5000 × 9200 — measure.
2. Floor-2 balcony edge (≤1502 from façade) — confirm soffit height.
3. Two round elements Ø2.0 — what are they (planter / fountain / tree)?
4. Pergola 6.0 × 5.8: west side open in DWG — keep, rebuild or remove?
5. Bay 5–6 / A–A': open to sky in F2 plan; F3 / roof not checked.
6. Levels from DWG: ±0.000 hall, −0.470 forecourt, −1.170 sidewalk.
7. Drainage, power, water points in the zone are not in the DWG.
8. North strip Z1–Z2 is the 8% car ramp to parking: keep, or relocate access?

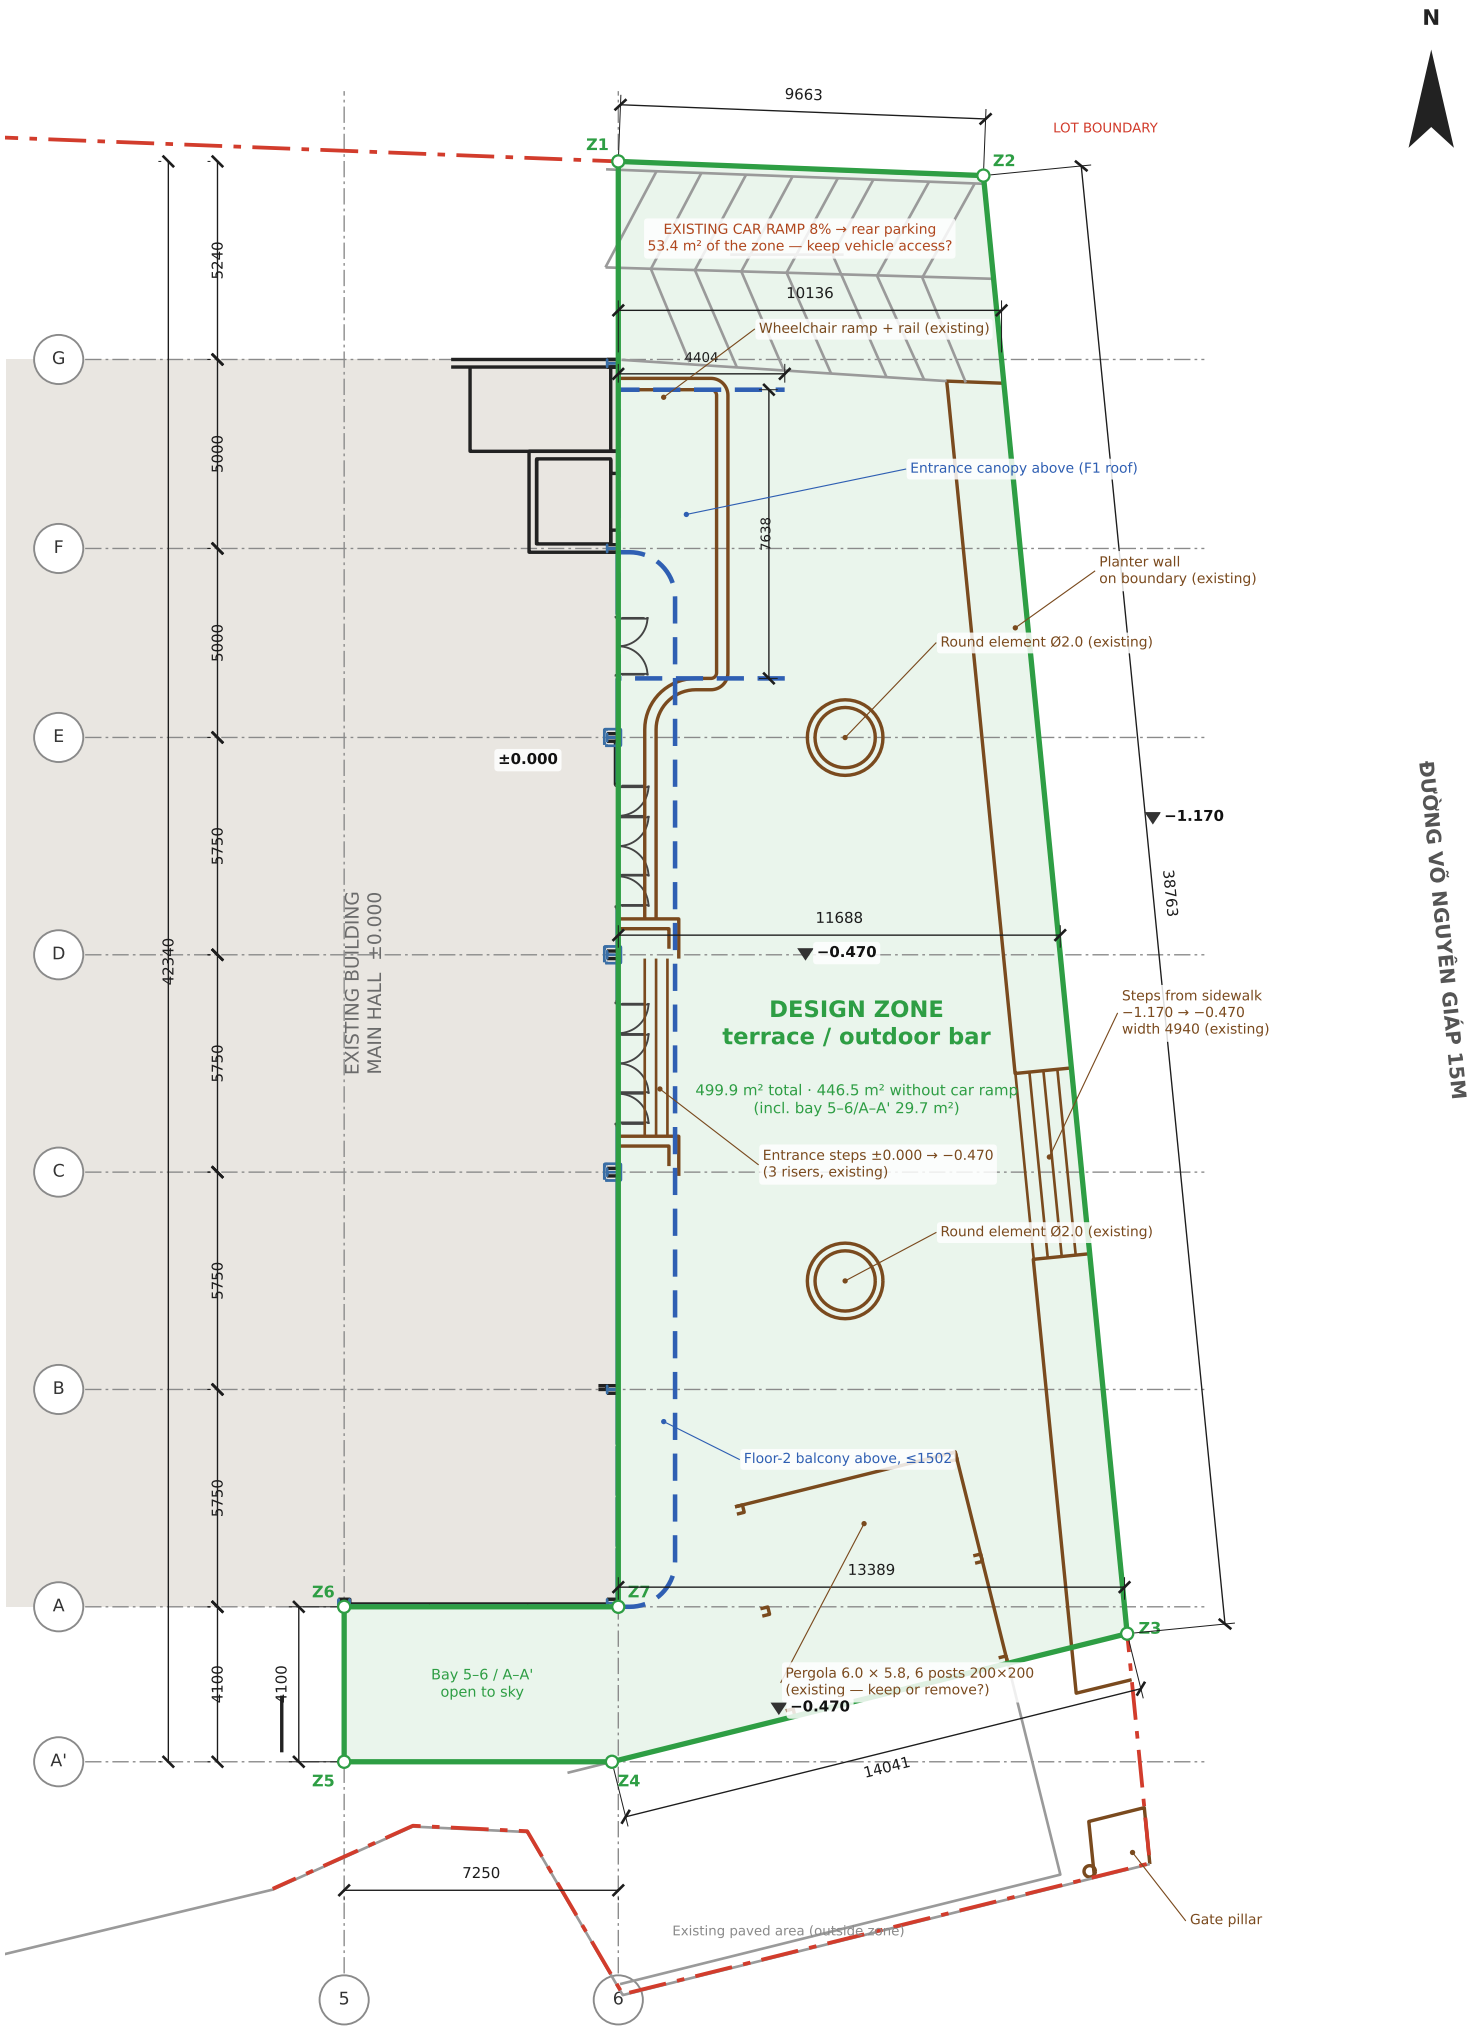

Design zone · Lot boundary · Above (canopy / balcony) · Existing site elements · Context

SAMARKAND

Design zone — base plan (existing conditions)

254 Võ Nguyên Giáp, P. Phước Mỹ, Q. Sơn Trà, Đà Nẵng

Source: BV hoàn công 10-07-2024 (Long House) — DWG, sheets "Tổng mặt bằng tầng 1", "Mặt bằng bố trí tầng 1/2". Sheets aligned on grid 6×G; geometry taken 1:1 in mm.

Origin (0,0) = axis 6 × axis A'. Units: mm. Levels: building ±0.000.

Scale	**1:200 @ A3**
Zone area	**499.9 m² (446.5 w/o ramp)**
Façade A–G	**33 000**
Depth at G / D / A	**10136 / 11688 / 13389**
East boundary	**38763, 5.63° off N**
Date / rev	**2026-10-22 / R0**