SAMARKAND

R12

Крытая терраса · планировка R12

2026-10-28

Таджикская и узбекская кухня · Võ Nguyên Giáp, 254, Дананг

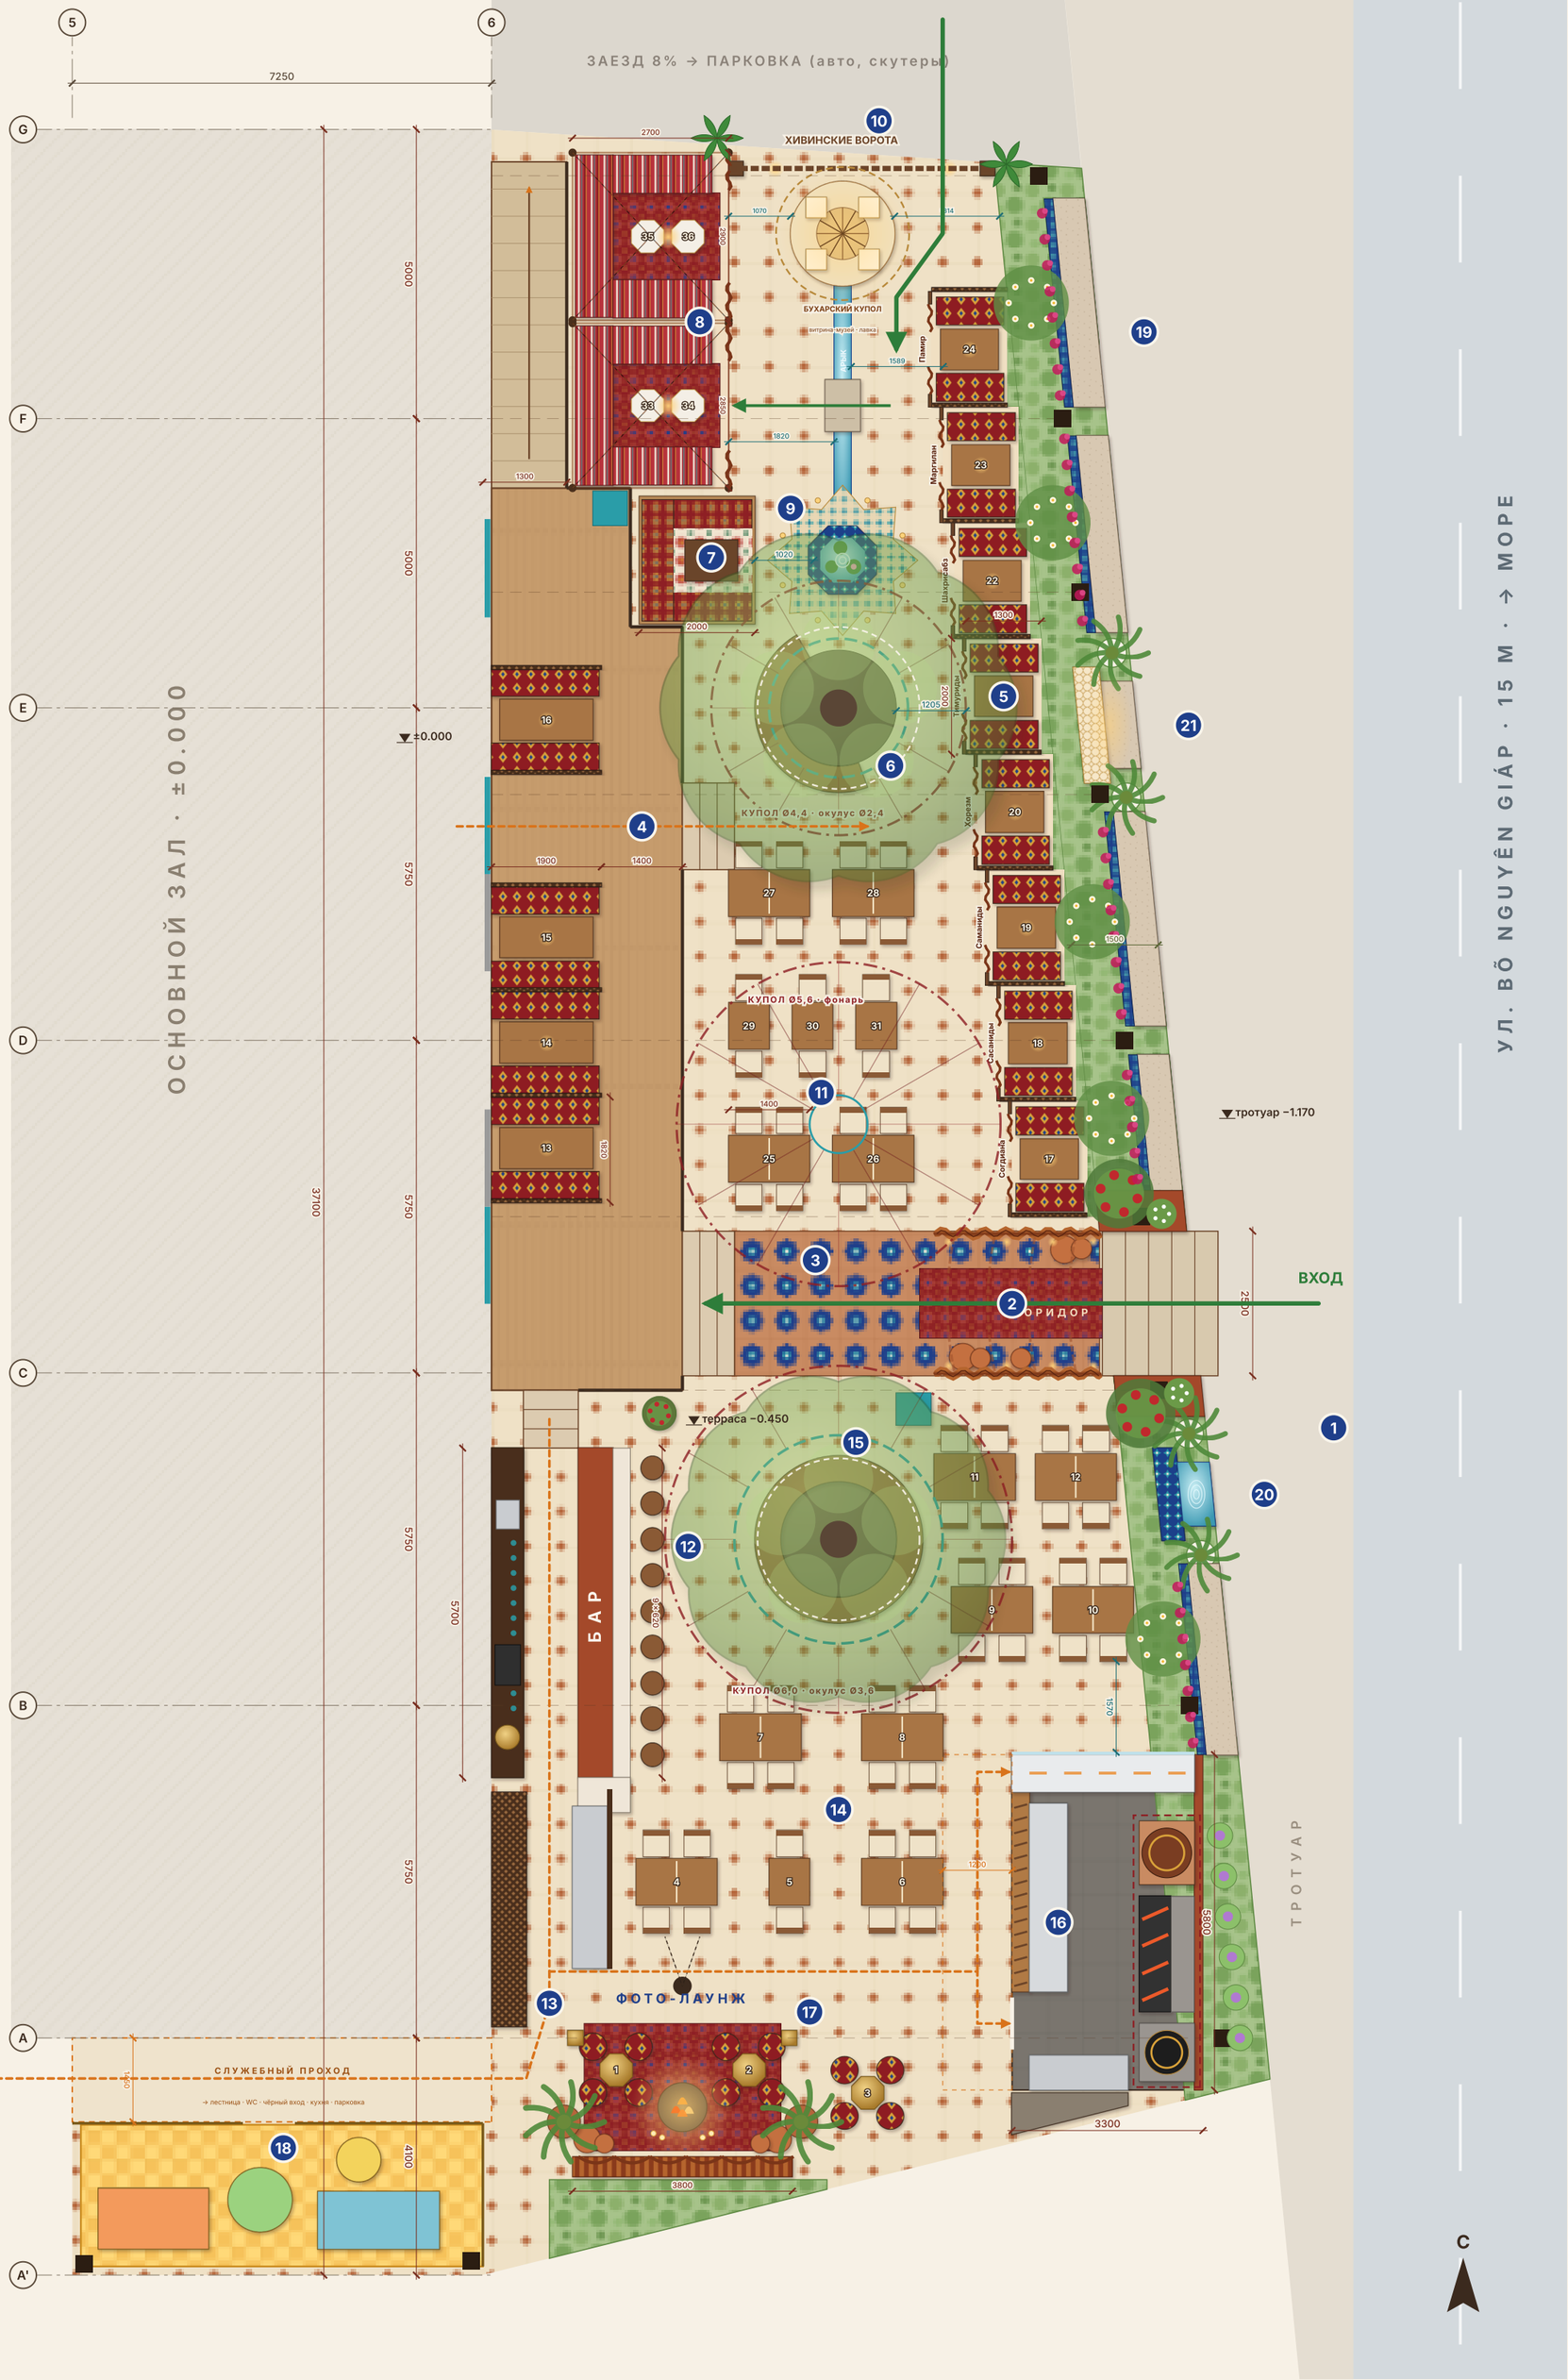

ЗОНЫ

1. **Главный вход · портал-пештак** — проём 2,5 м, 4 ступени с тротуара
2. **Коридор-драпировка** — бархат, ковровая дорожка, хумы, фонари
3. **Аллея к залу** — гирих, 2,5 м, хостес у выхода
4. **Айван-платформа ±0.000** — 4 седир-кабинки на 6 у стены, проход 1,4 м
5. **Тематические кабинки** — 8 закрытых залов: эпохи и города, шторы-порталы
6. **Чинар-дворик (север)** — купол с окулусом, крона выходит наружу
7. **Топчан 2,0 × 2,2 м** — 6 гостей, курпачи с 3 сторон, у фонтана
8. **Два шатра-маджлиса 2,6 × 2,75 м** — по 8 гостей, вход по мостику через арык
9. **Фонтан-хауз и арык** — хауз Ø1,2 м, арык 0,3 м ведёт от северного входа
10. **Северный вход · «Хивинские ворота»** — ворота 4,1 м, Бухарский купол — витрина и лавка, пандус 1:12
11. **Зал север** — ряды по 4 + средний ряд из 3 столов на 2
12. **Бар** — чай, самовар, кофе · 9 стульев
13. **Станция персонала** — стеллажи, касса, вода, лёд, посуда
14. **Зал юг** — ряд 4 + 2 + 4 и ряд 4 + 4
15. **Чинар-дворик (юг) + столы у входа** — купол Ø6 с окулусом; 4 стола у мангала
16. **Мангальная 4,2 × 4,8 м** — тандыр · мангал · казан · раздача к гостям
17. **Фото-лаунж «Очаг»** — драпировки, ковры, огонь-чаша, 3 столика, 12 пуфов
18. **Детская зона** — ограждение, мягкое покрытие
19. **Уличные скамьи** — литой бетон в стенке клумбы, майолика
20. **Фонтан-себиль** — майоликовая стена, латунный носик, чаша
21. **Уличная фото-арка** — ниша со скамьёй, подсветка, пальмы

ПОСАДКА

Столы у входа	16
Скамья у чинара (юг)	10
Зал юг	18
Фото-лаунж (пуфы)	12
Барная стойка	9
Айван: седир-кабинки (4 × 6)	24
Зал север	22
Скамья у чинара (север)	6
Тематические кабинки	32
Топчан	6
Шатры-маджлисы (2 × 8)	16
Итого мест в ресторане	**171**
+ уличные скамьи (вне счёта)	~35

Столы: на 2 — 4, на 4 — 12 (каждый делится на 2 × 2), кабинки на 6 — 4

ЭРГОНОМИКА · норма / по плану

Главный проход / аллея	≥1500	**2500**
Проход к кабинкам	≥1200	**1205**
Проход топчан ↔ фонтан	≥900	**932**
Проход на айване	≥1200	**1400**
Модуль стола: на 1 гостя / глубина	600–700 / 750–800	**700 / 800**
Край стола → спинка стула	450–600	**490**
Спинка–спинка (без прохода)	≥450	**520**
Барная стойка: высота / вынос	1050 / 250–300	**1050 / 300**
Шаг барных стульев	600–650	**620**
Рабочая зона повара	≥1200	**2450**
Раздача → гости	≥1500	**1570**
Пандус: уклон / ширина	1:12 / ≥1200	**1:12 / 1300**
Топчан: высота / на 1 гостя	400–450 / ≥600	**450 / 700**

ОБОЗНАЧЕНИЯ

- Колонна навеса (сталь, обшивка деревом)
- Ось здания
- Маршрут персонала
- Дверь зала закрыта
- Размер, мм
- Купол над головой, окулус открыт к небу
- Балка навеса
- Вход гостей
- Дверь зала открыта
- Вытяжной зонт
- № стола
- Стык модулей стола

· Основа: исполнительный DWG (Long House, 10.07.2024) 1:1. Отметки: тротуар −1.170, терраса −0.450, айван и зал ±0.000.

· Навес: стальные балки по осям, сэндвич-панель 50 мм, уклон 5% к улице, желоб вдоль улицы; низ плиты балкона +3.850, волна-ламели демонтируются.

· Три купола в кровле: над чинарами Ø6,0 и Ø4,4 с открытым окулусом Ø3,6 / Ø2,4 (крона выходит наружу), между ними глухой Ø5,6 с фонарём. Под окулусами только всепогодные скамьи.

· Все отдельно стоящие столы — модули 700 × 800: пары разъединяются на 2-местные или сдвигаются в столы на 6–8 (ряды выровнены).

· Двери: C–D южная открыта; C–D северная и D–E южная закрыты (банкетка); D–E северная и E–F у лифта открыты.

ОЗЕЛЕНЕНИЕ

- **Гранат (анор) — символ Самарканда** — у входа в клумбе и в кадке у бара
- **Плюмерия (франжипани)** — в уличной клумбе, аромат вечером
- **Бугенвиллия** — по спинкам скамей и колоннам
- **Жасмин самбак** — у портала входа
- **Пальма арека** — кадки в фото-лаунже
- **Банан, стрелиция Николая** — зелёная рамка Хивинских ворот
- **Райхон, мята, базилик** — грядка у мангальной — к столу
- **Лотос, кувшинка** — в хаузе
- **Чинары (существующие)** — выходят через окулусы куполов, подсветка снизу

Масштаб 1:100 · А2

0 — 5 м

МАНГАЛЬНАЯ · 1:100

ШАТЁР-МАДЖЛИС (×2) · 1:75

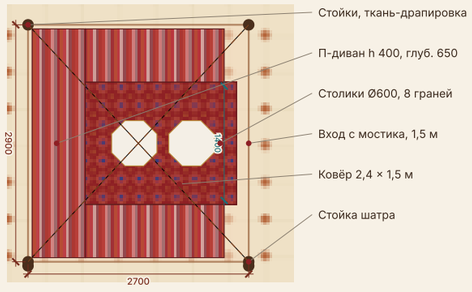

АЙВАН: СЕДИР-КАБИНКИ · 1:75

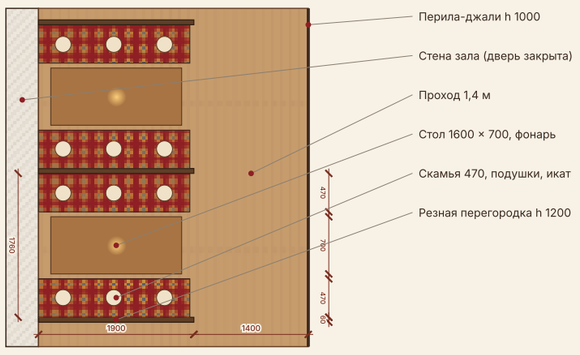

СТОЛЫ-МОДУЛИ · 1:100

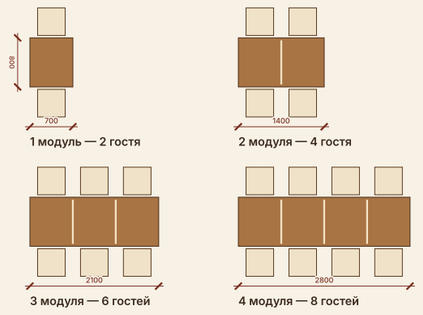

Столешница 700 × 800, h 750; стык на скрытых стяжках

Концепция для согласования с заказчиком · размеры уточнить на месте